

ДИЗАЙН - ПРОЕКТ

квартиры по адресу ул. Волынская, д. 10



дизайн студия Clearline
г. Киев, 2021 г.

clear
line

Ведомость визуализаций

№ листа	Перечень чертежей	Примечания
1	Общие данные	
2	Планировка помещения	
3	Демонтаж стен	
4	Монтаж стен	
5	Ванная комната общий вид	
6-8	Ванная комната сан.тех. выводы, электрика	
9	Кухня общий вид	
10-11	Кухня сан.тех. выводы, электрика	
12	Спальня общий вид	
13-15	Спальня электрика	
16-17	Гостиная электрика	
18	Детская комната общий вид	
19-21	Детская комната электрика	

Согласовано


Инв. № подп. Подп. и дата
Бзм.инв. №

Ведомость чертежей

№ листа	Перечень чертежей	Примечания
22	План обмеров	
23	План расстановки мебели	
24	План демонтажа	
25	План возводимых конструкций	
26	План напольных покрытий	
27	План подогрева полов	
28	План потолочных конструкций	
29	План размещения кондиционеров	
30	Схема размещения осветительных приборов	
31	Схема размещения выключателей по группам и электропроводов для дополнительного оборудования	
32	Схема размещения розеток	
33	План-схема отделочных материалов	
34	Раскладка стен. Раскладка плитки пола. Прихожая	
35	Раскладка стен. Гостиная	
36	Раскладка стен. Раскладка плитки пола. Кухня	
37	Раскладка стен. Спальня	
38	Раскладка стен. Детская	
39	Раскладка стен. Раскладка пола. Гардеробная-Кладовка	
40	Раскладка стен. Раскладка полов. Санузел	

Изм.	Кол.уч	Лист	№док	Подпись	Дата	Общие данные		
						Квартира		
Н.контр			План			clear line		
						P.П.	1	40

Перепланировка помещения с расстановкой мебели

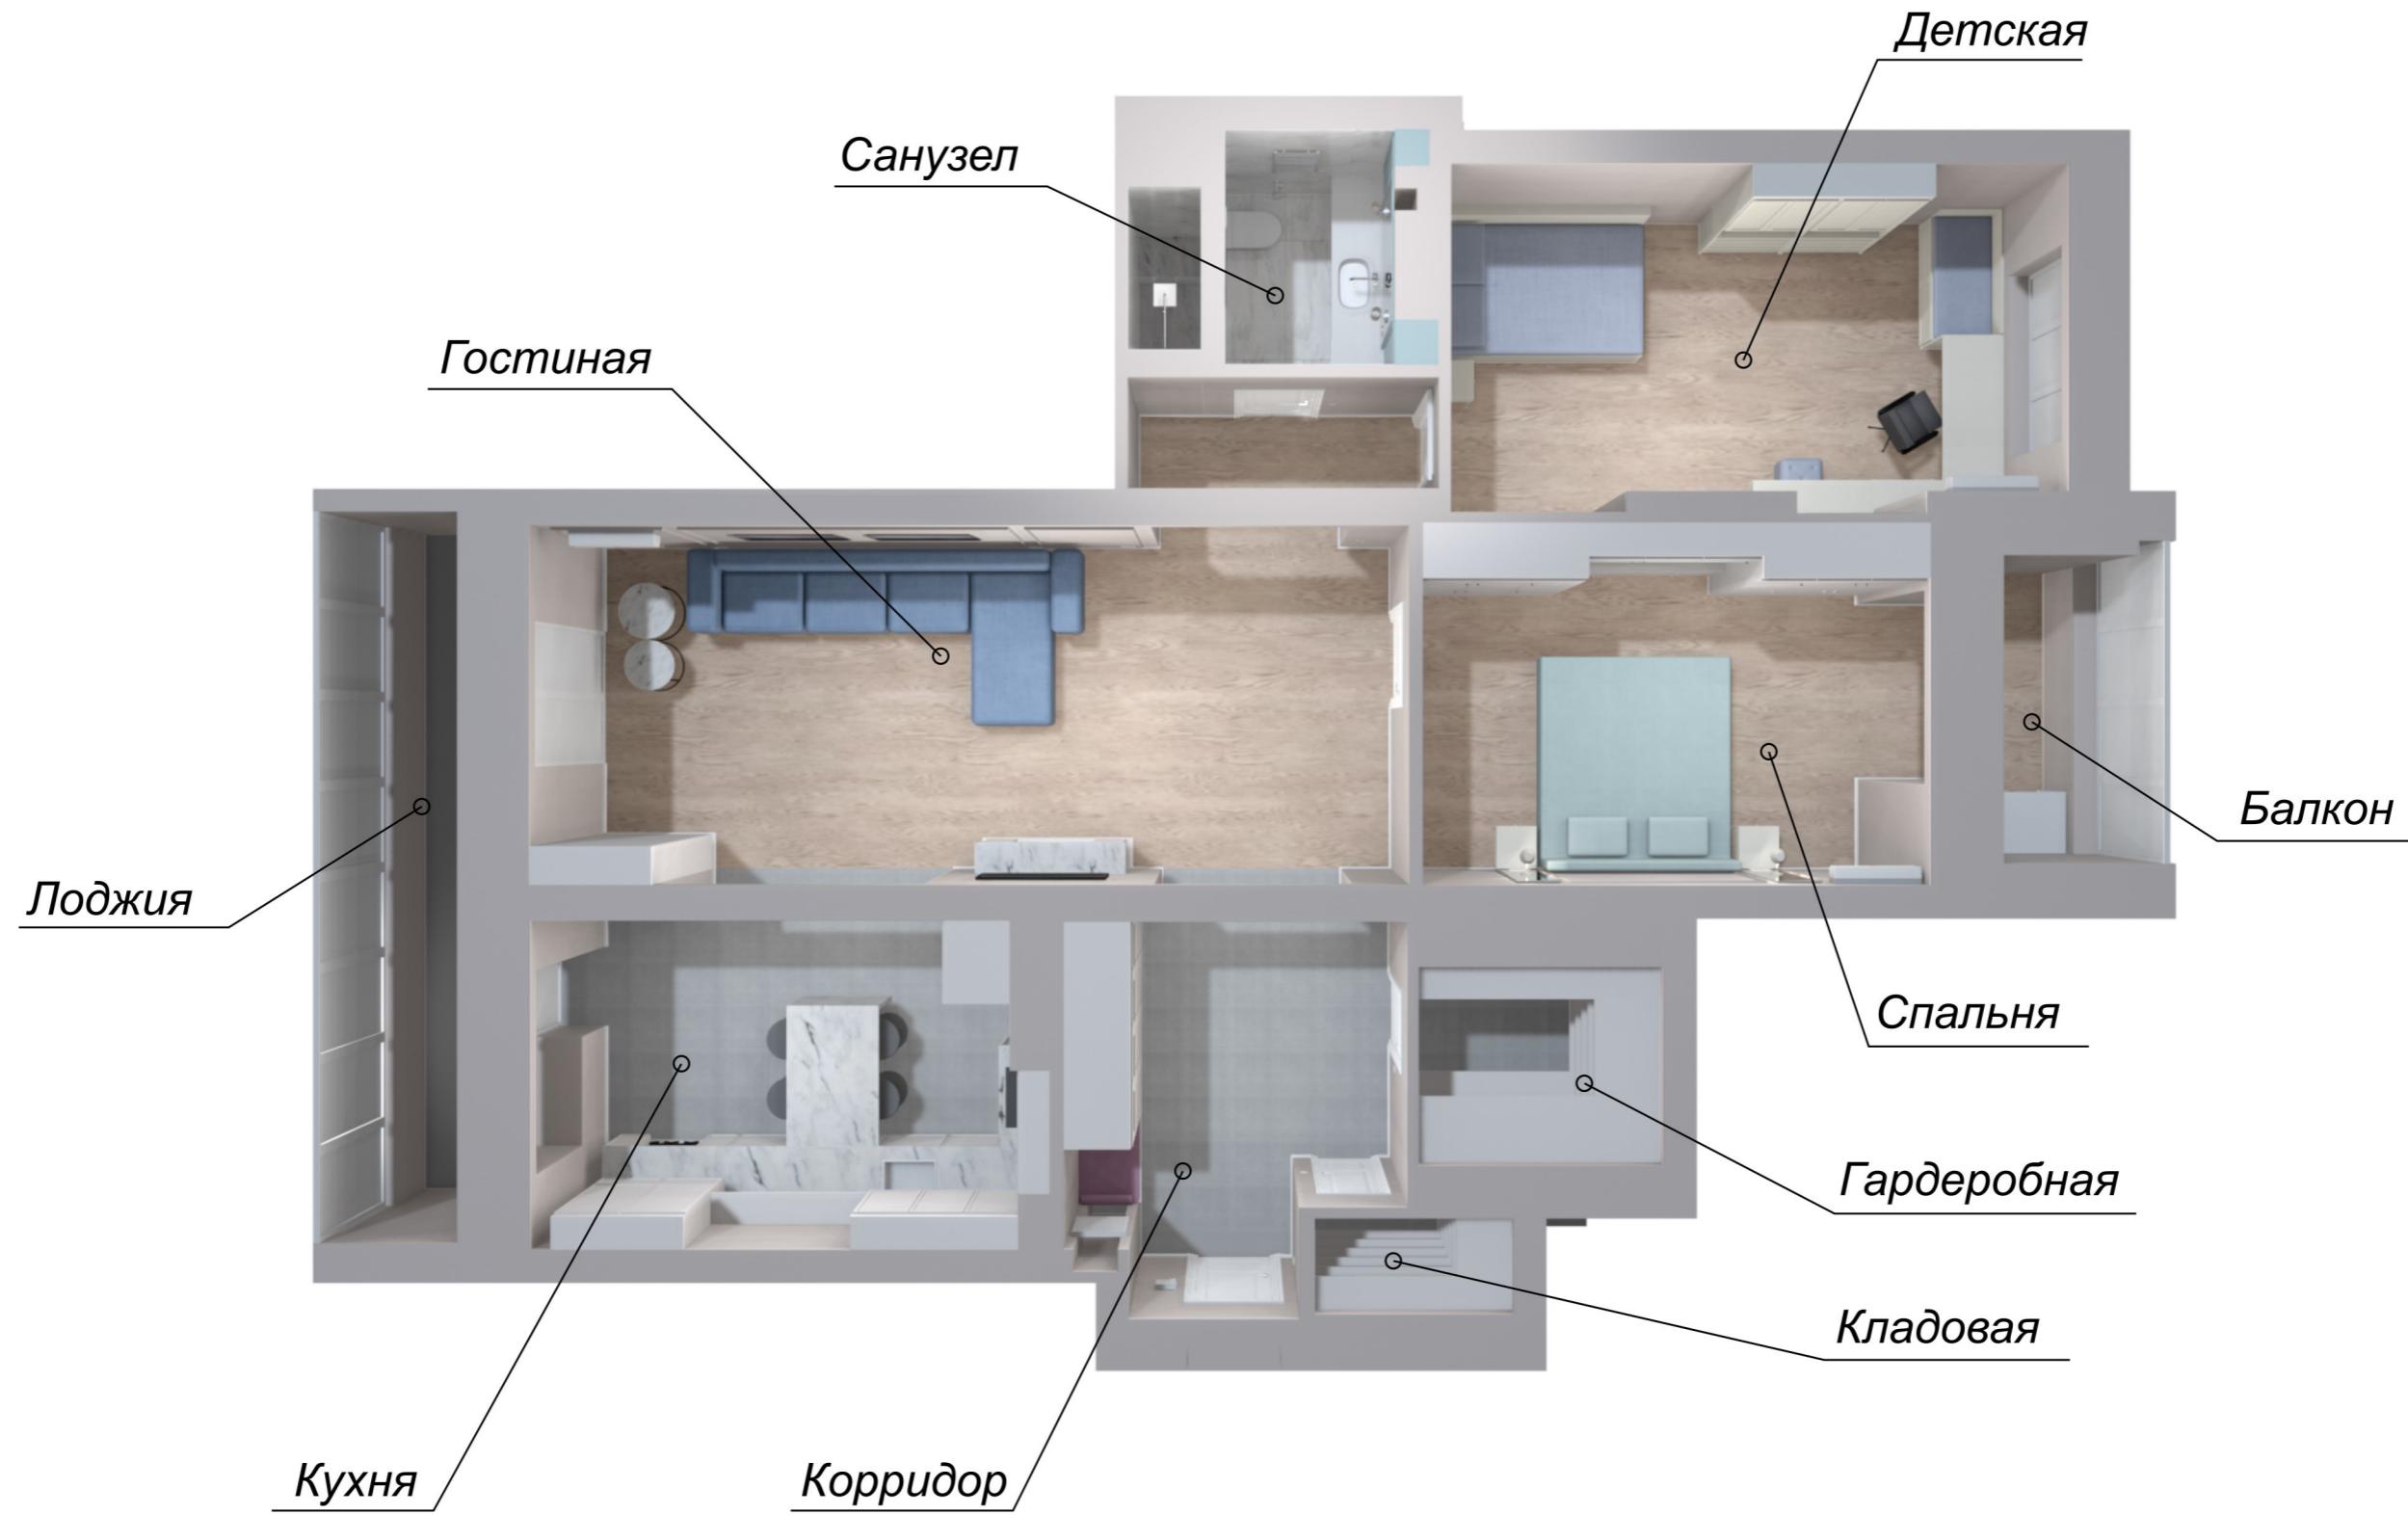


Демонтаж стен


Вид сверху



Вид в перспективе

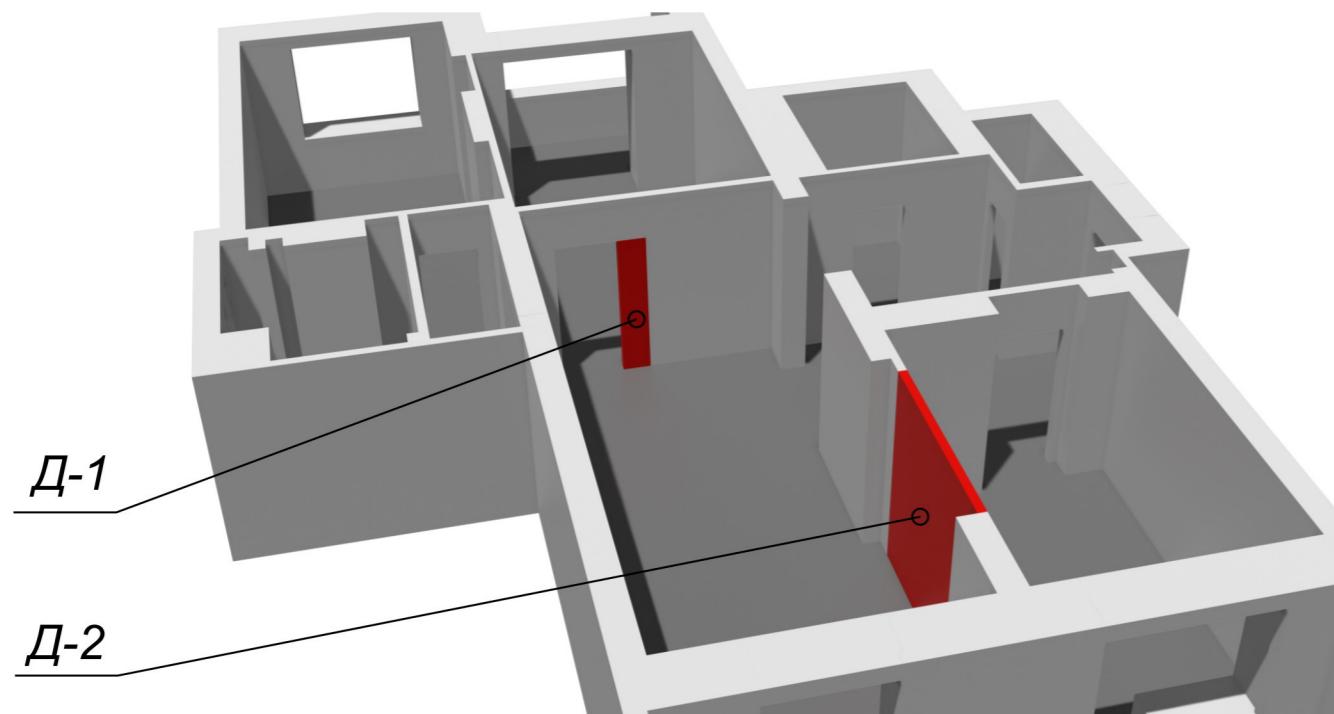

Стена Д-1

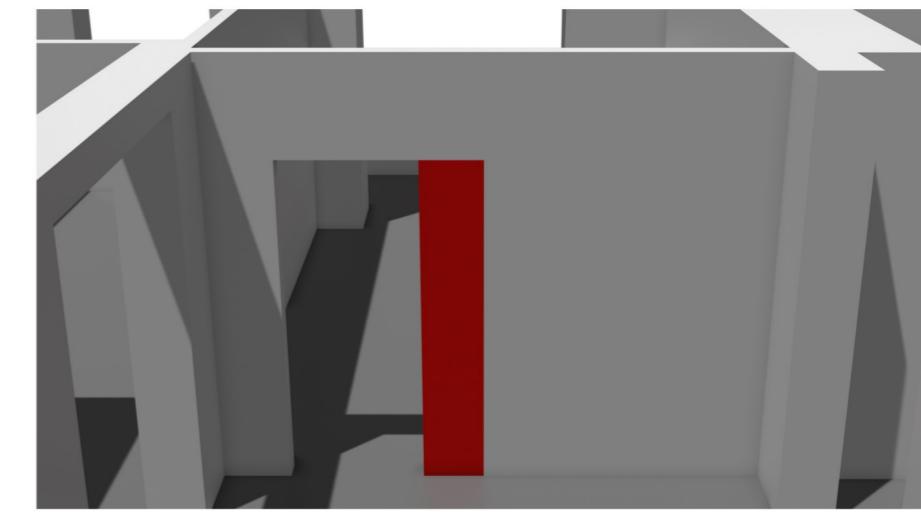

Стена Д-2


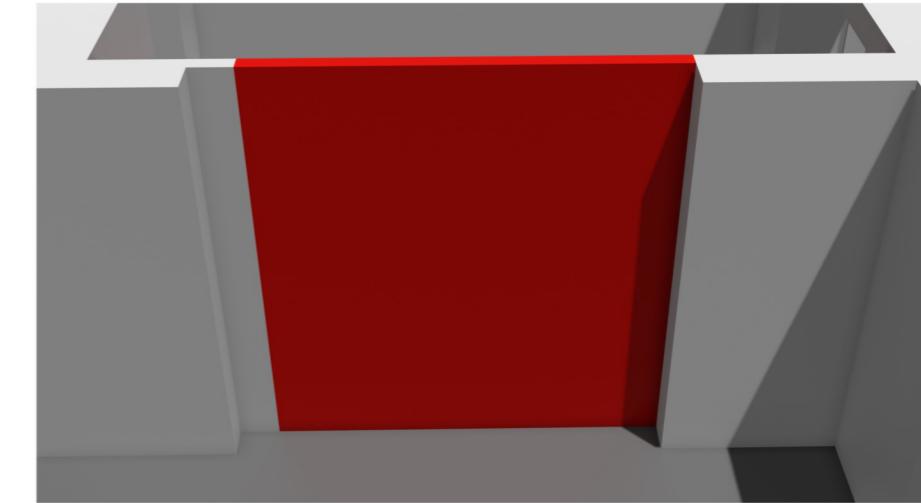


Таблица площадей демонтируемых стен

Д1	0,73 м ²
Д2	6,5 м ²

Монтаж стен

Вид 1 в перспективе

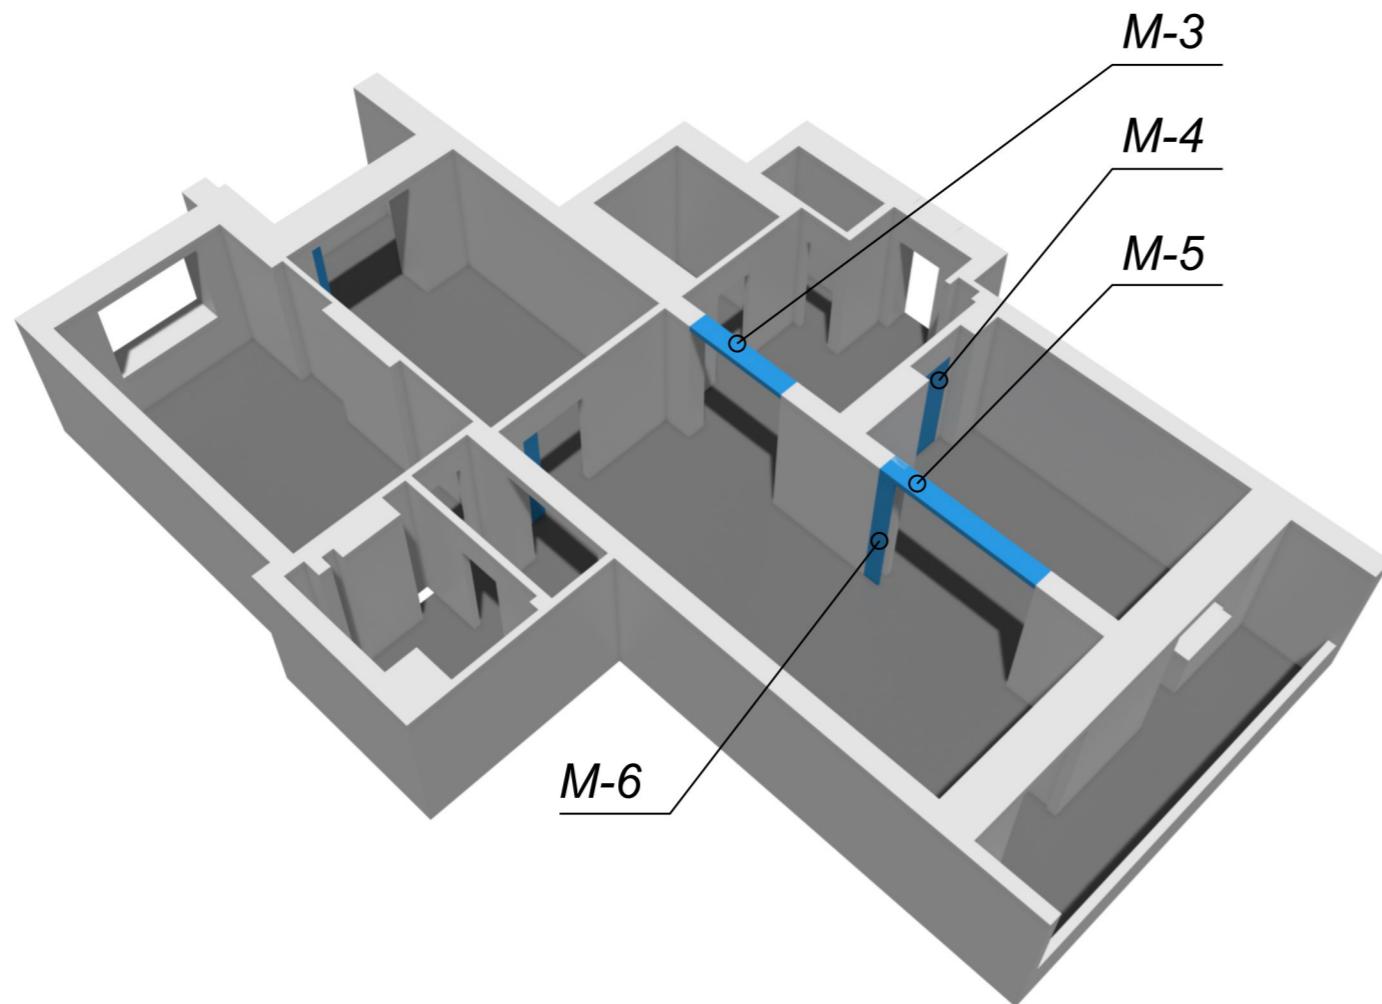

Вид 2 в перспективе

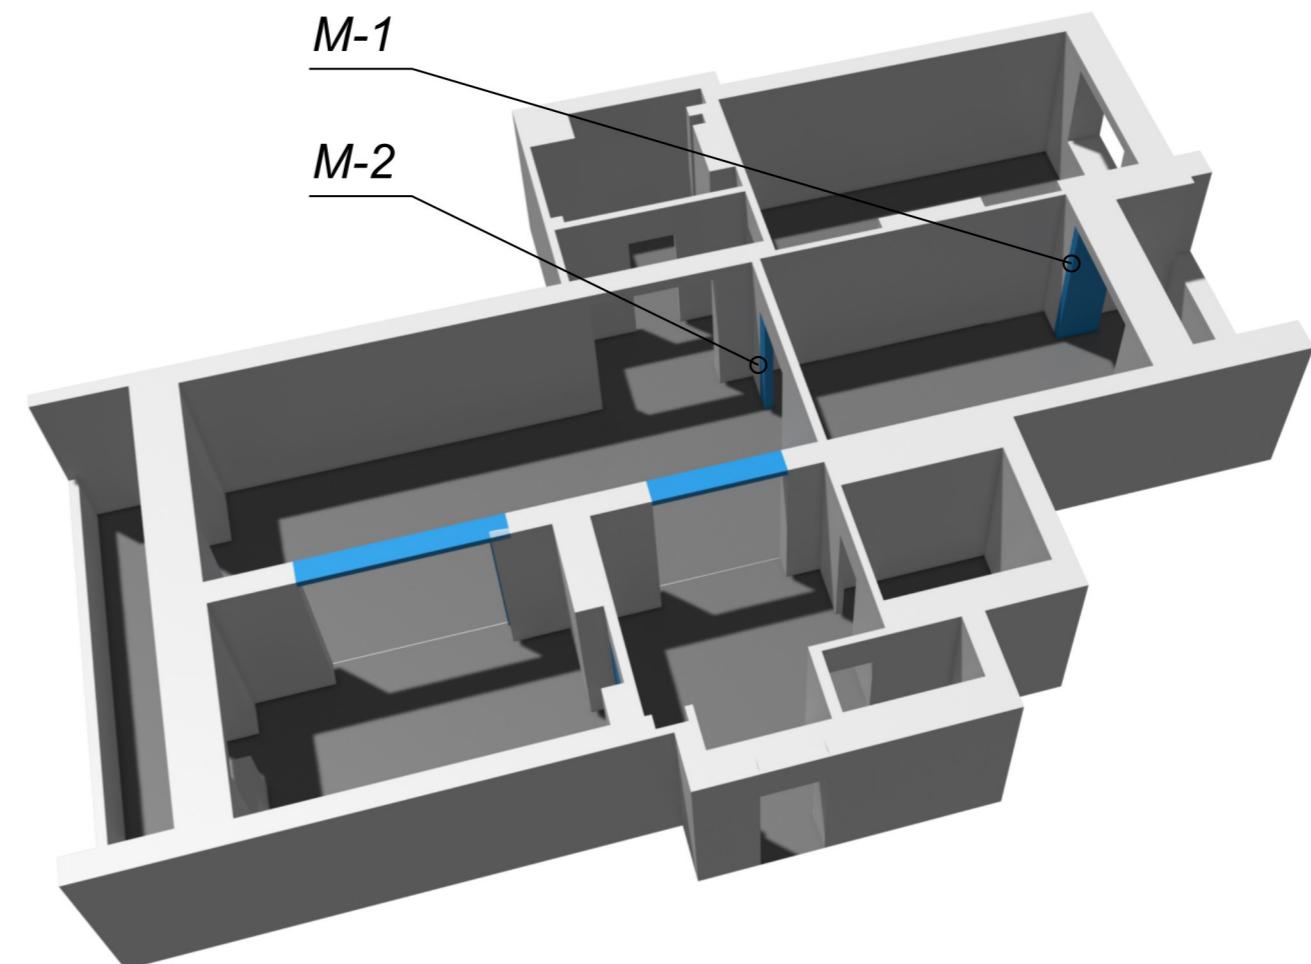


Таблица площадей монтируемых стен

Инв. № подл.	Подлп. и дата	Взам. инв. №
M1	1,58 м ²	
M2	0,54 м ²	
M3	0,6 м ²	
M4	1,8 м ²	
M5	0,87 м ²	
M6	0,67 м ²	

Ванная комната

Ванная комната общий вид



Инв. № подл.	Подл. и дата	Взам. инв. №	Согласовано

Ванная комната

лист


5

Ванная комната

Расположение розеток и выключателей,
сантехнических выводов стена 3-2



Расположение розеток и выключателей,
стена 2-1

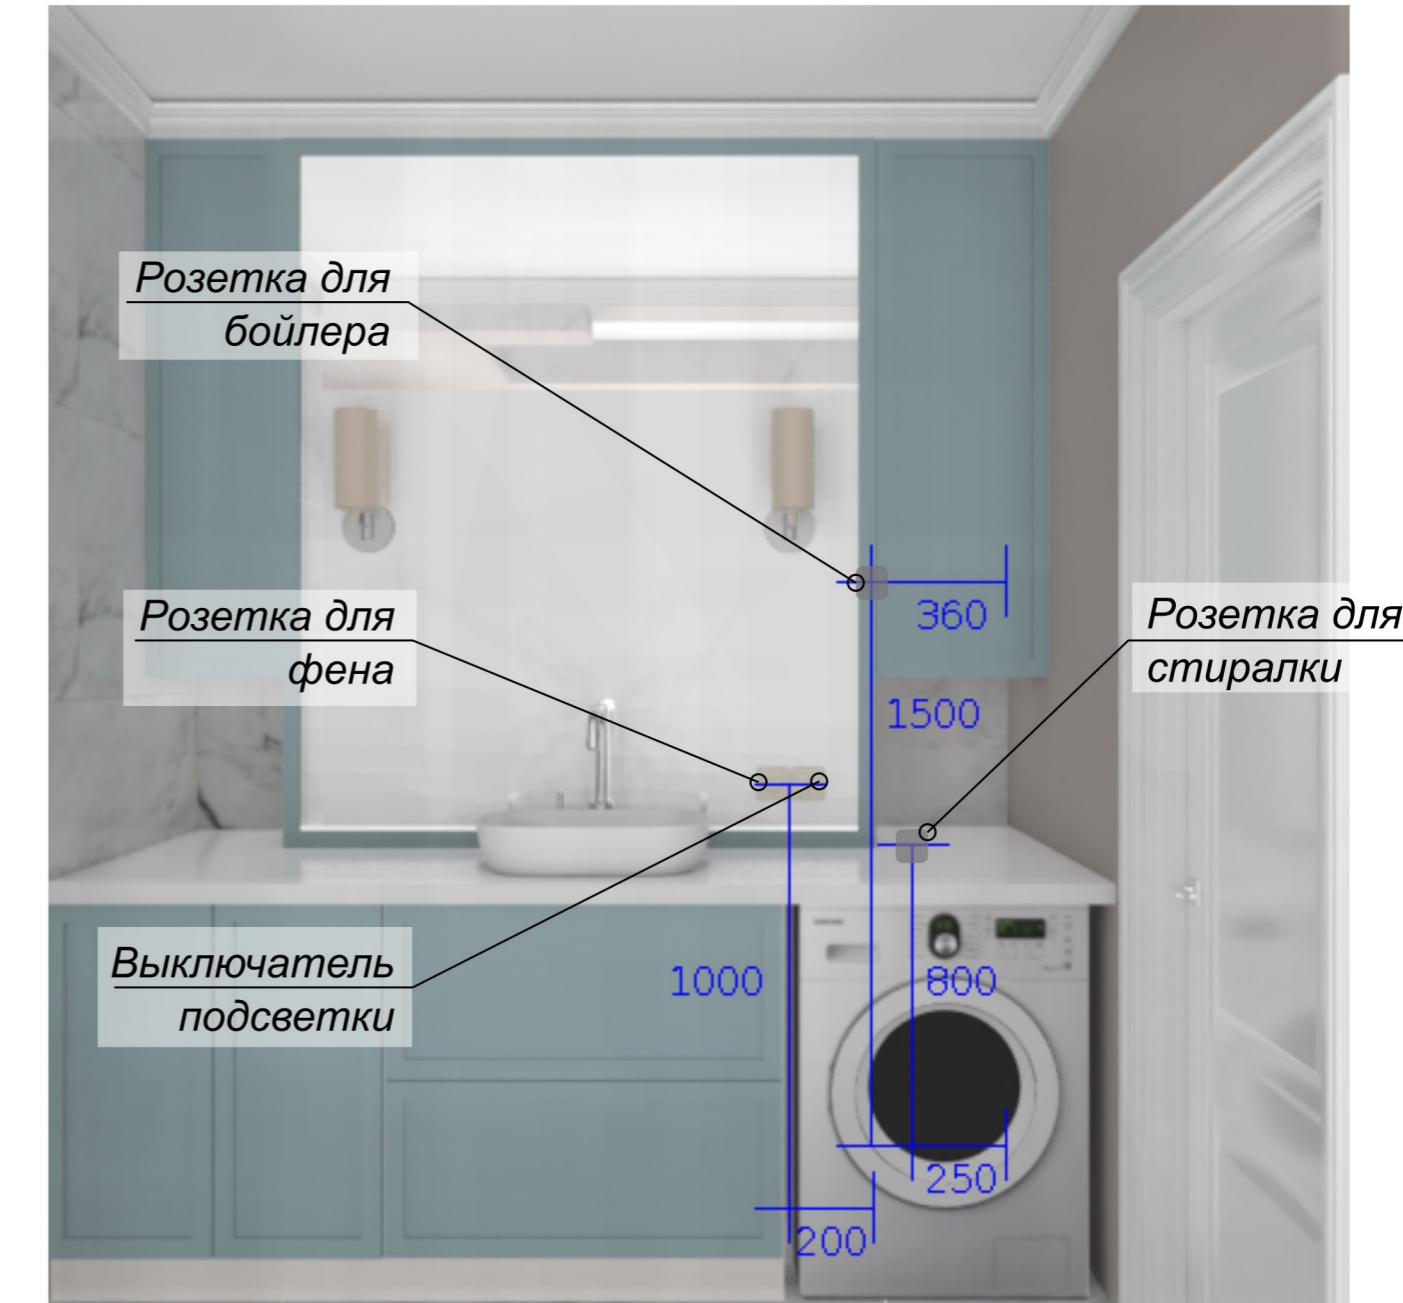

Условные обозначения


- - выводы горячей воды
- - выводы холодной воды
- - слив воды

Ванная комната

Расположение сантехнических выводов
стена 6-6.1



Расположение сантехнических выводов
стена 2-1

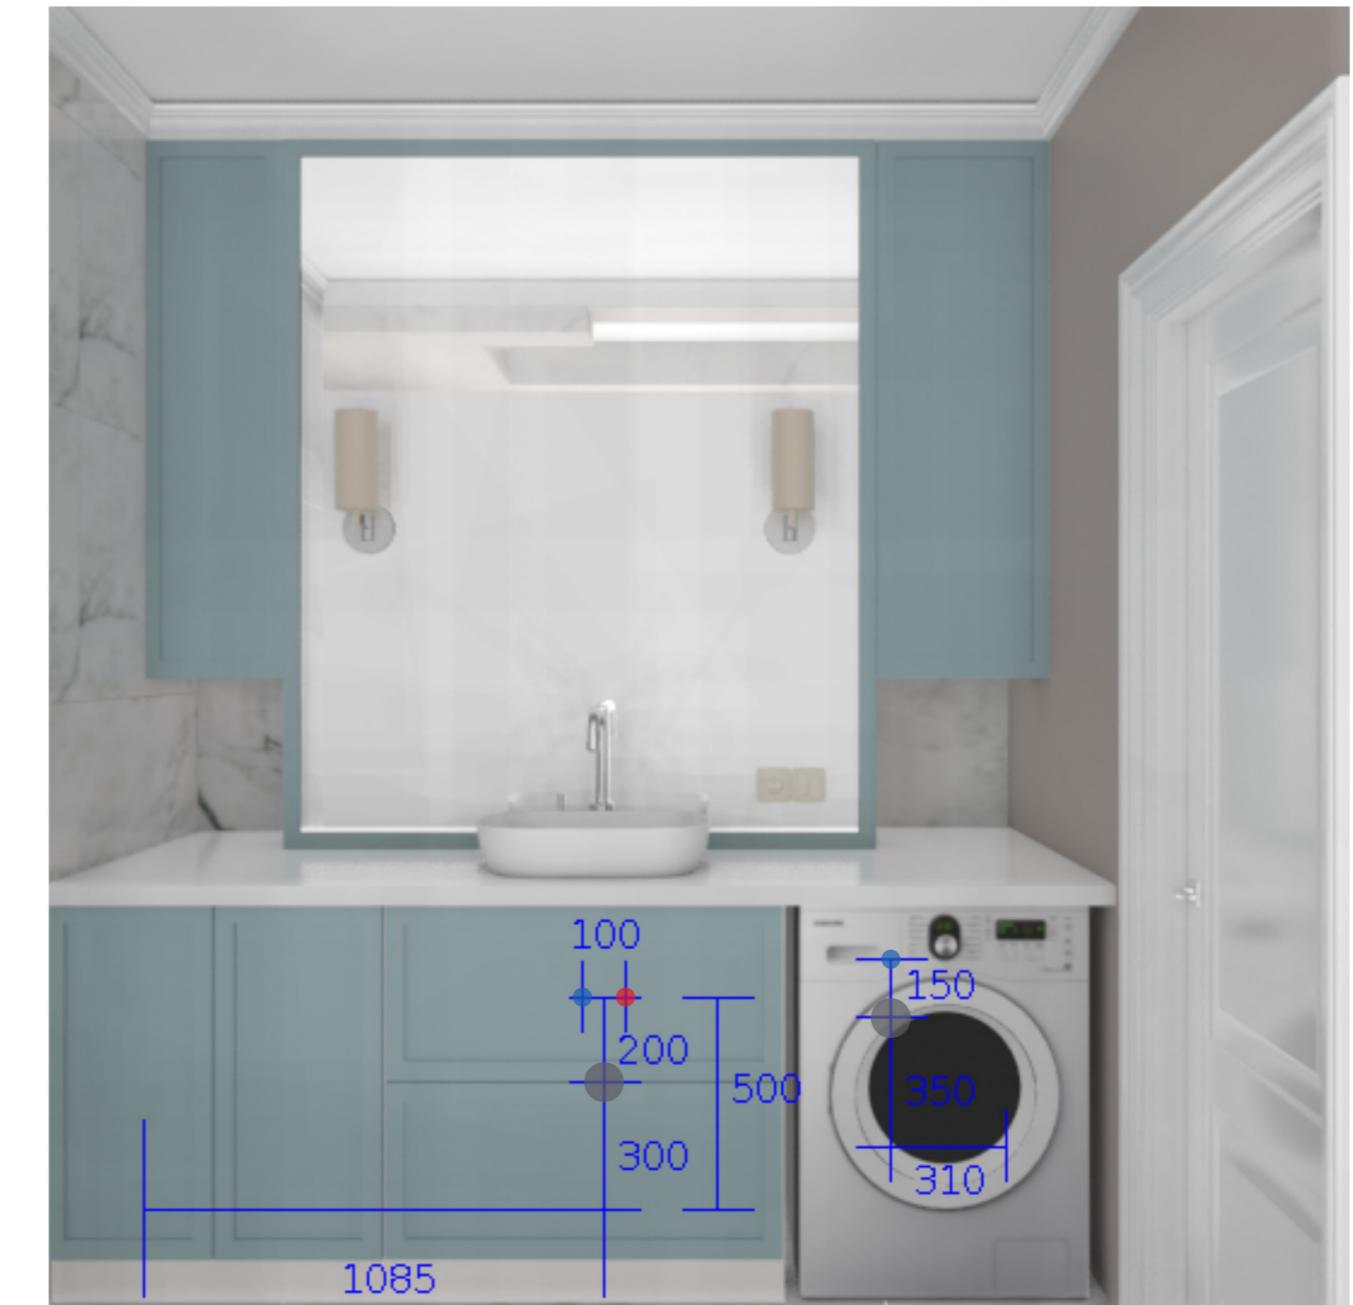

Условные обозначения

- - выводы горячей воды
- - выводы холодной воды
- - слив воды

Ванная комната

Расположение сантехнических выводов
стена 4-3



Условные обозначения

- - выводы горячей воды
- - выводы холодной воды
- - слив воды

Кухня

Кухня общий вид




Инв. № подл.	Подл. и дата	Взам. инв. №	Согласовано

Кухня общий вид

лист

Кухня

Расположение розеток и выключателей стена 13-14

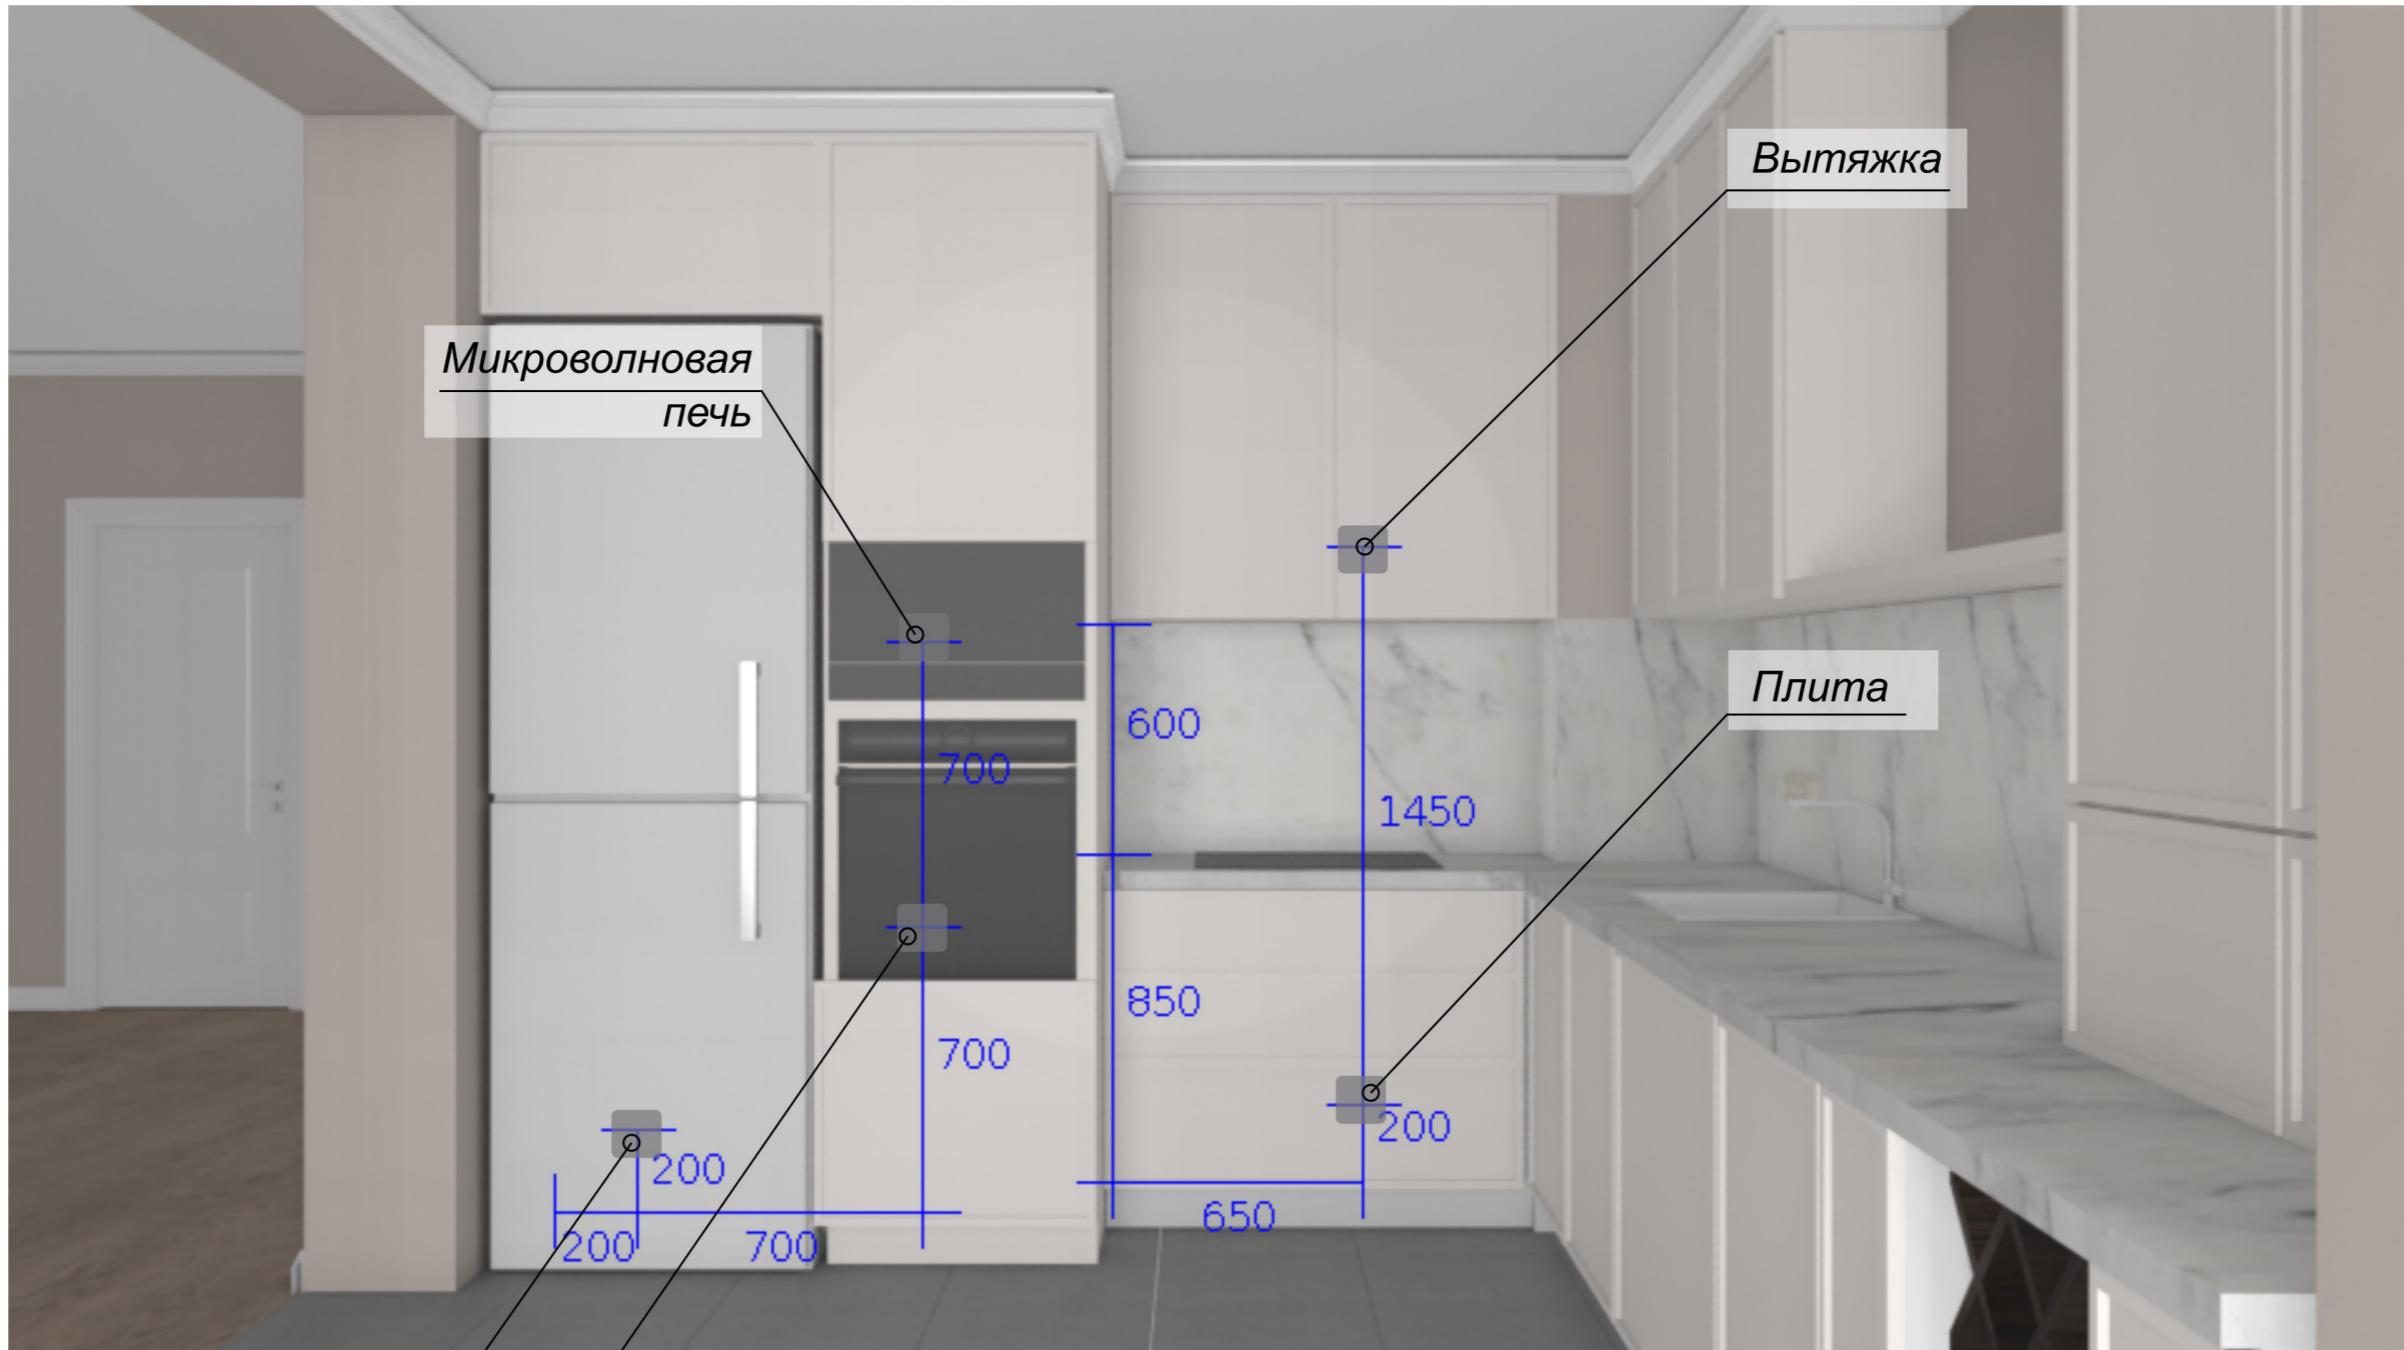

Согласовано

Инв. № подп. Подп. и дата Взам. инв. №

Холодильник

Духовой шкаф


Кухня сан.тех. выводы, электрика

лист

10

Кухня

Расположение розеток и выключателей, сантехнических выводов стена 14-11

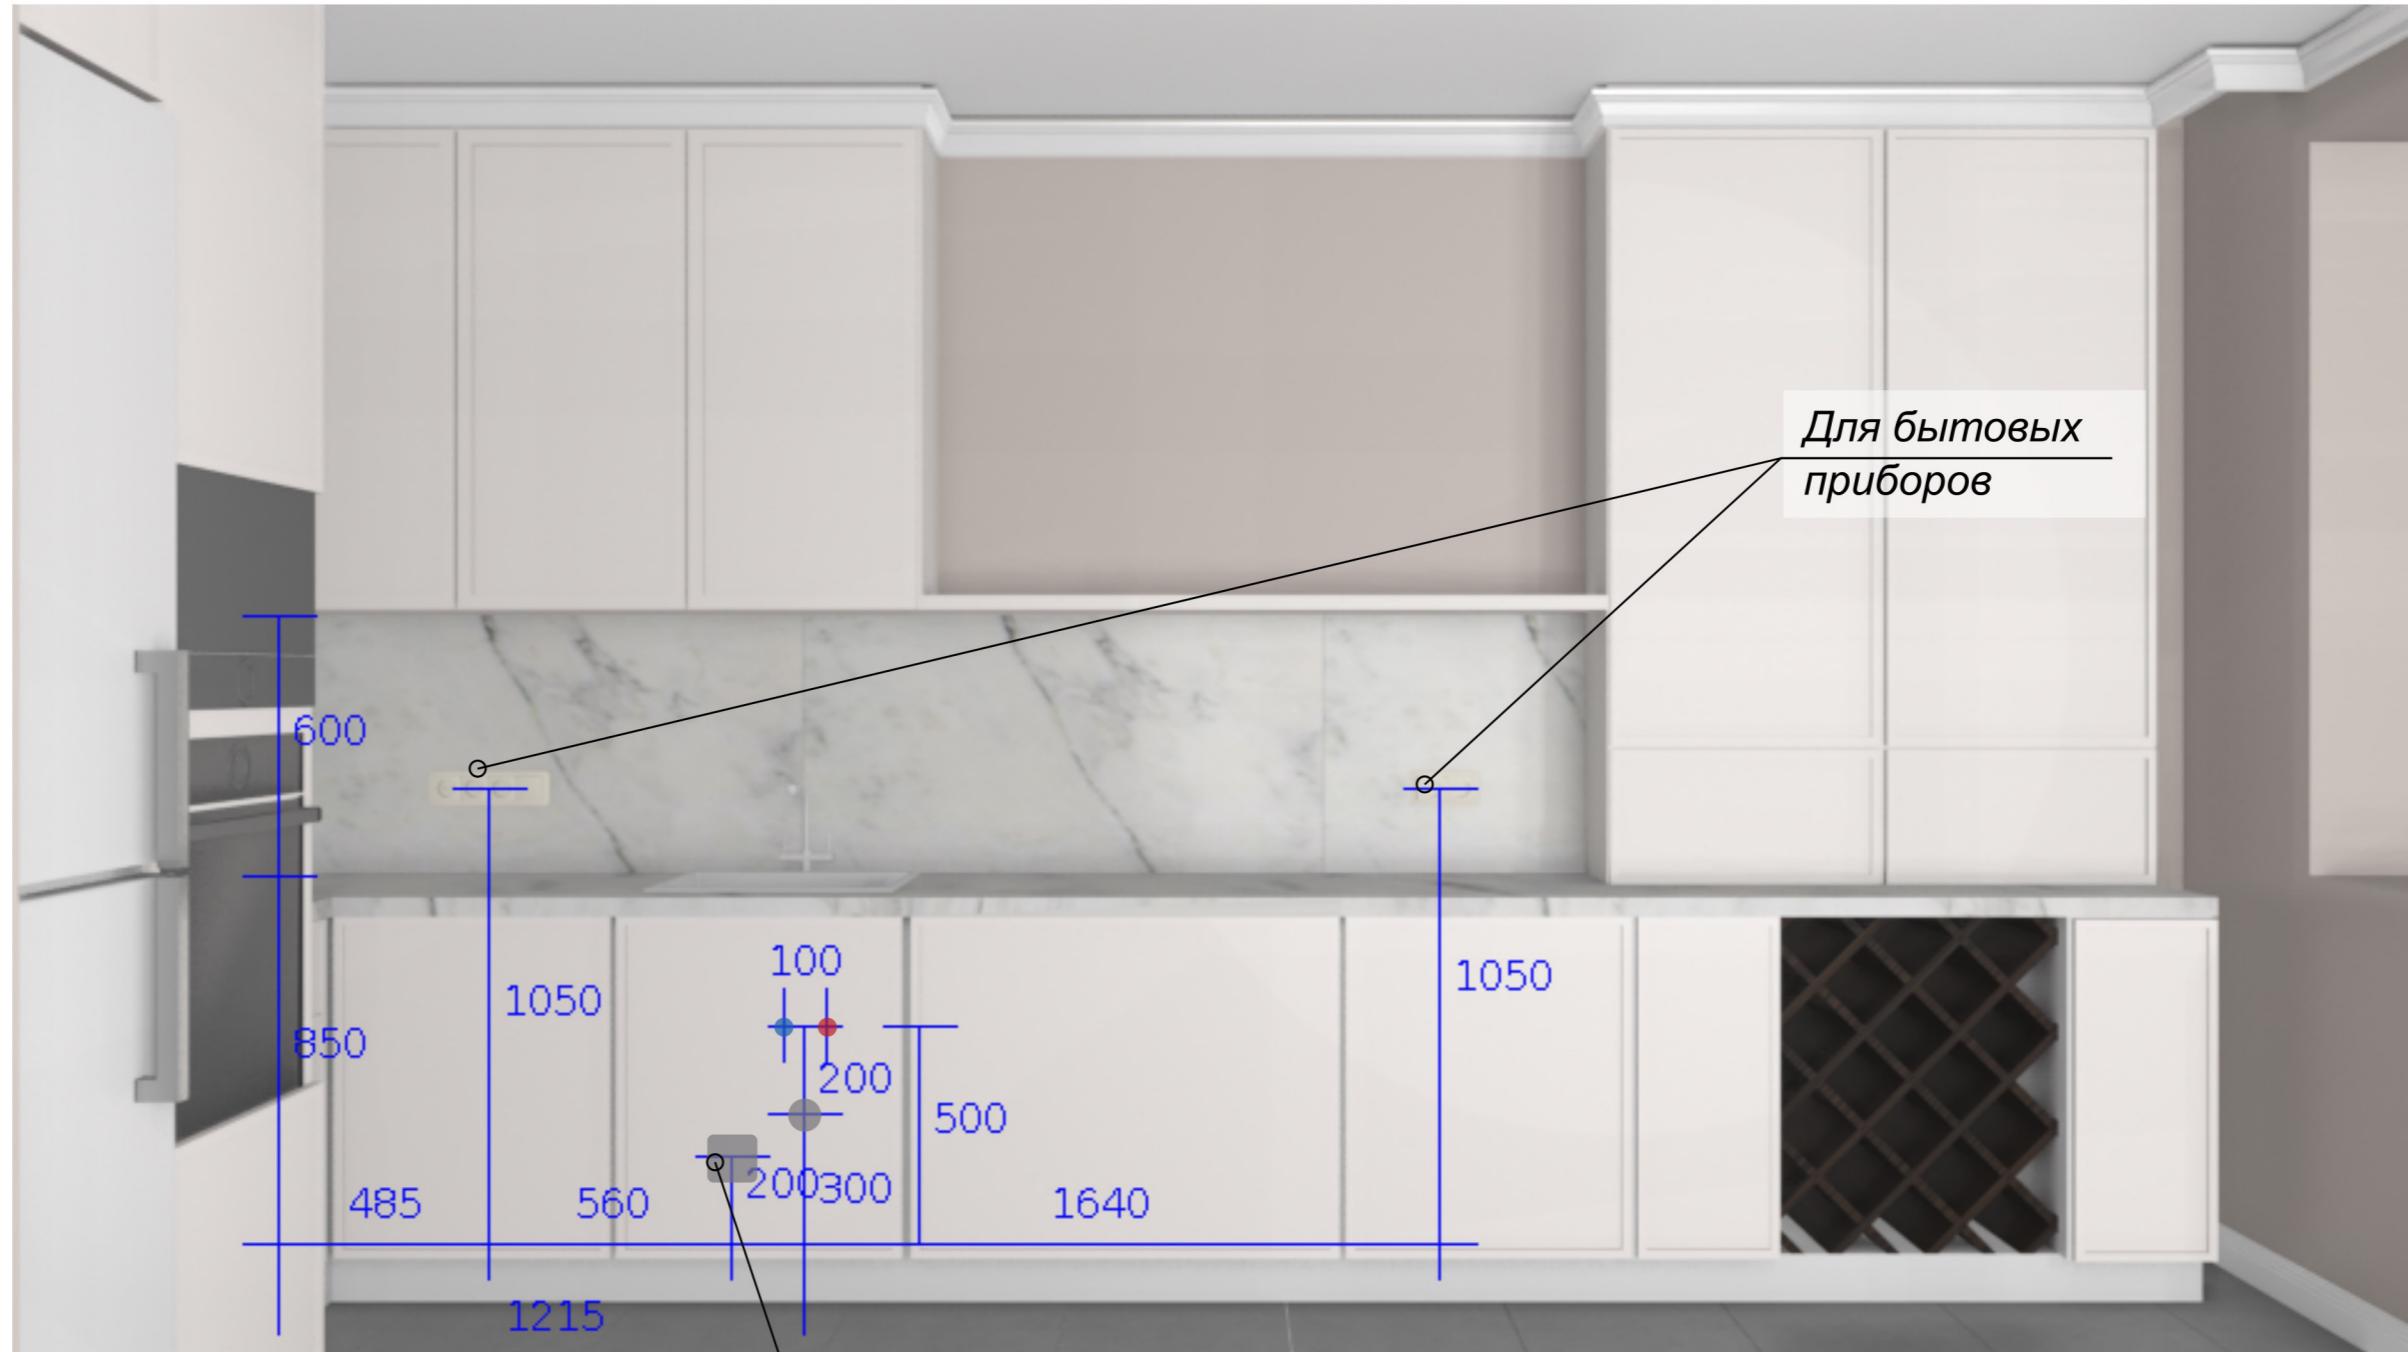

Условные обозначения

- - выводы горячей воды
- - выводы холодной воды
- - слив воды

Спальня


Спальня общий вид



Инв. № подл.	Подл. и дата	Взам. инв. №	Согласовано

Спальня

Расположение розеток и выключателей стена 4-1

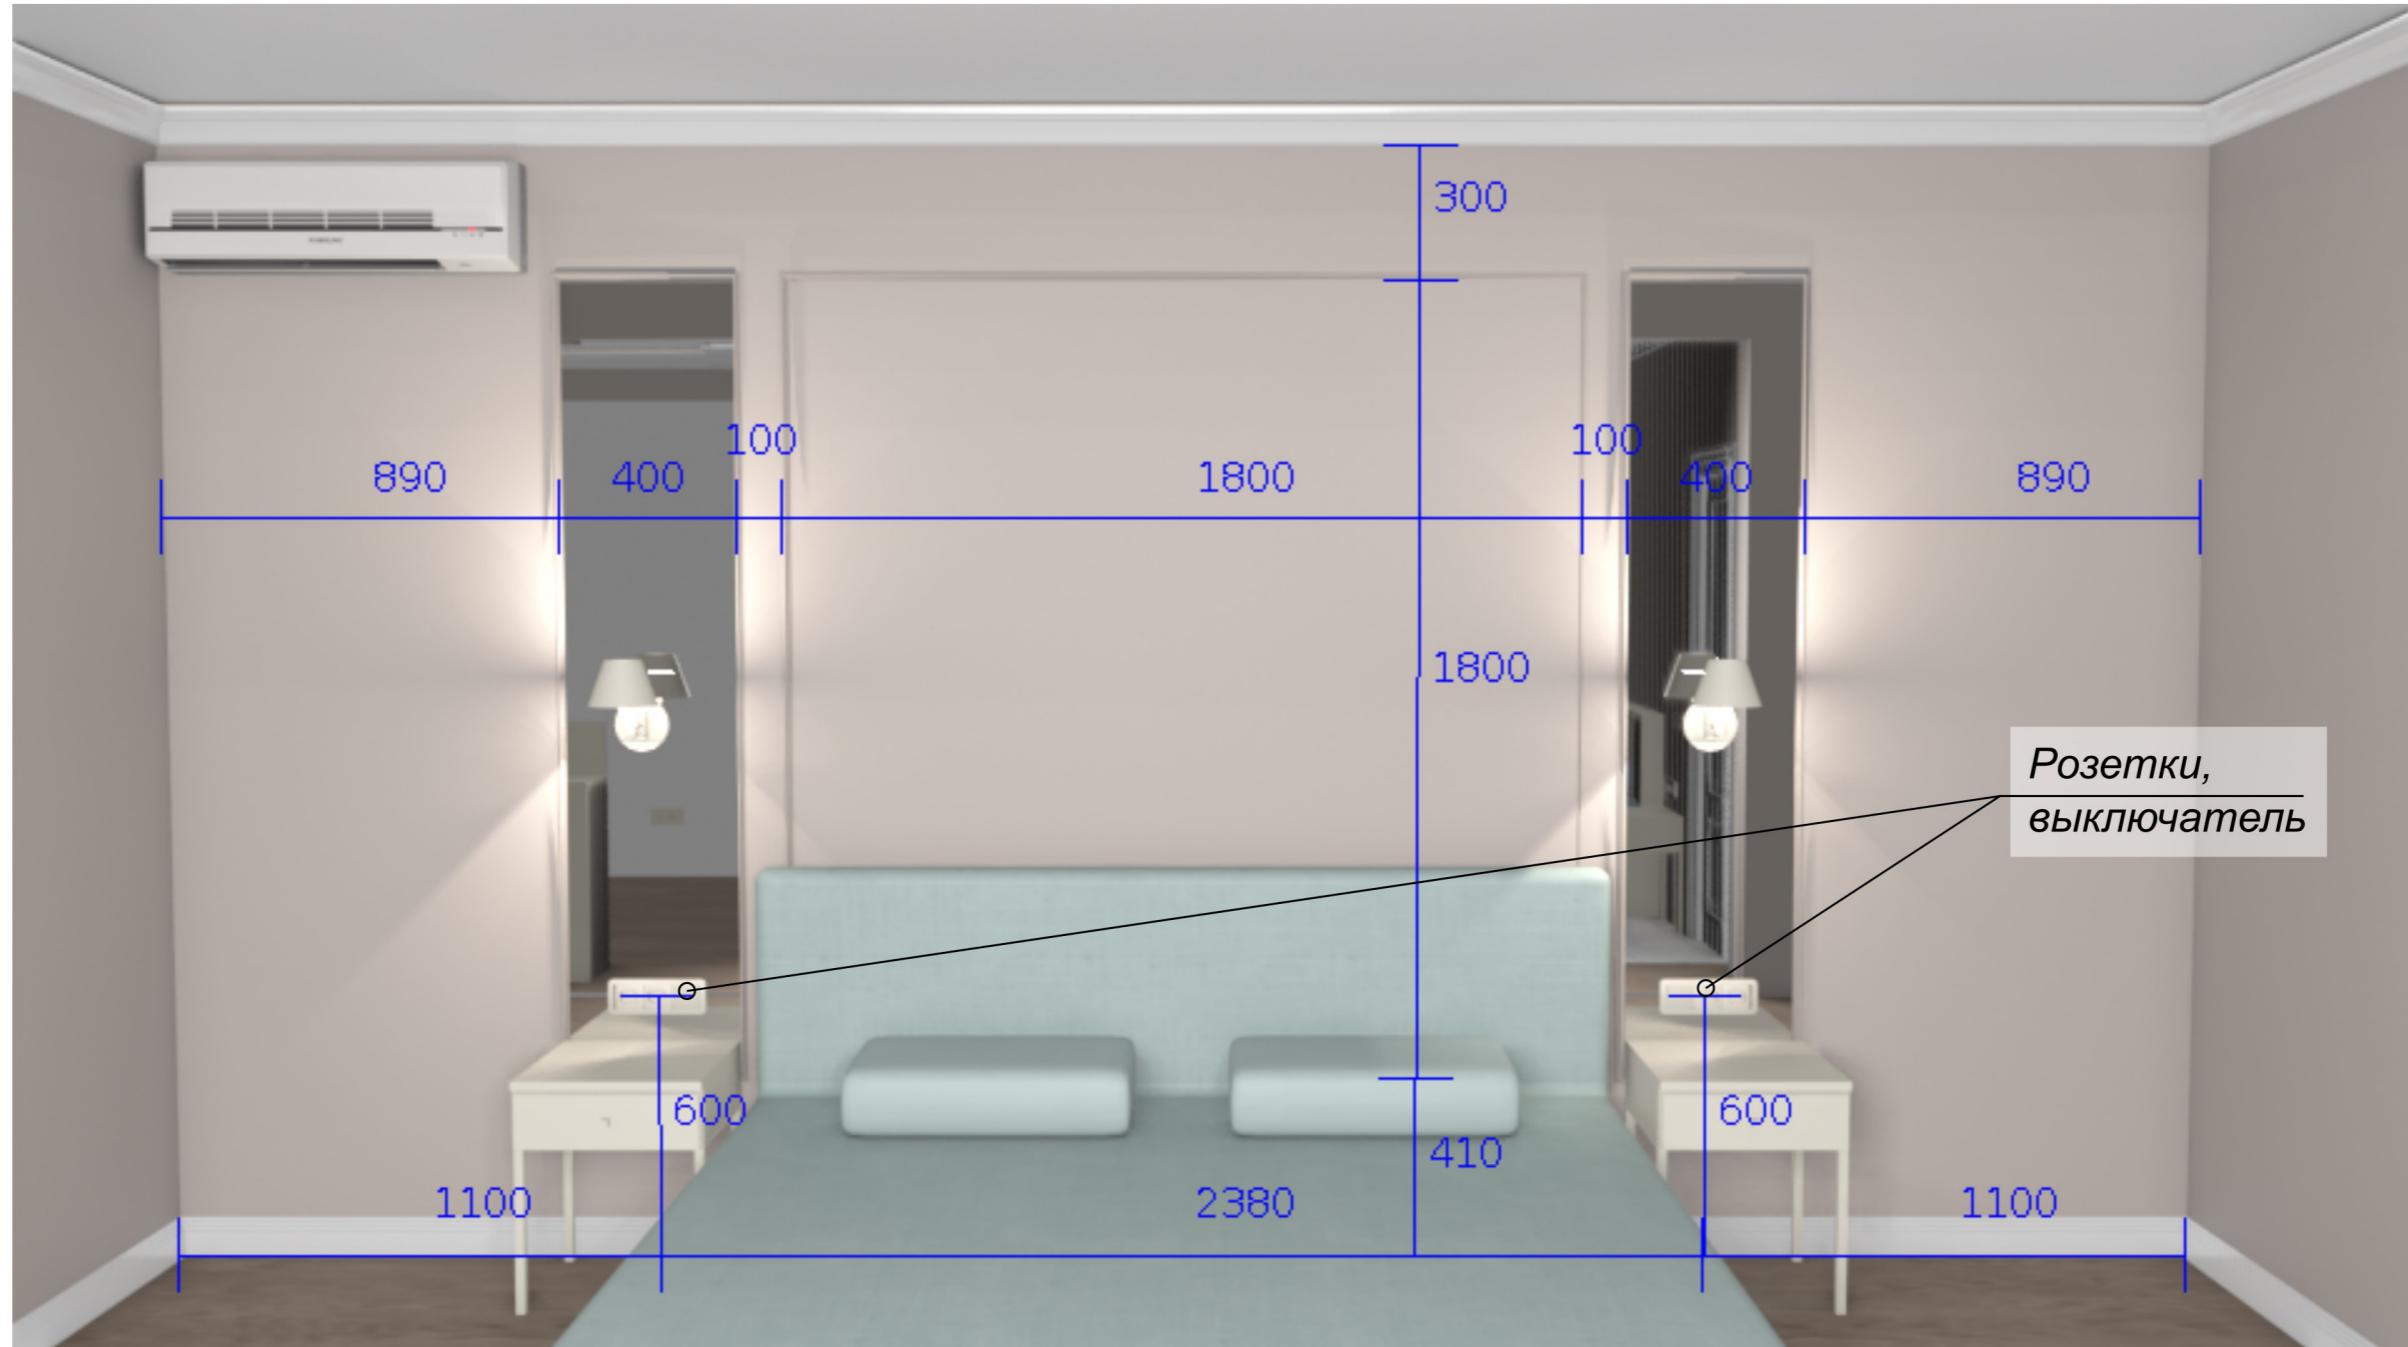

Согласовано

Инв. № подл.

Подл. и дата


Взам. инв. №

лист

13

Спальня


Расположение розеток и выключателей стена 2-3

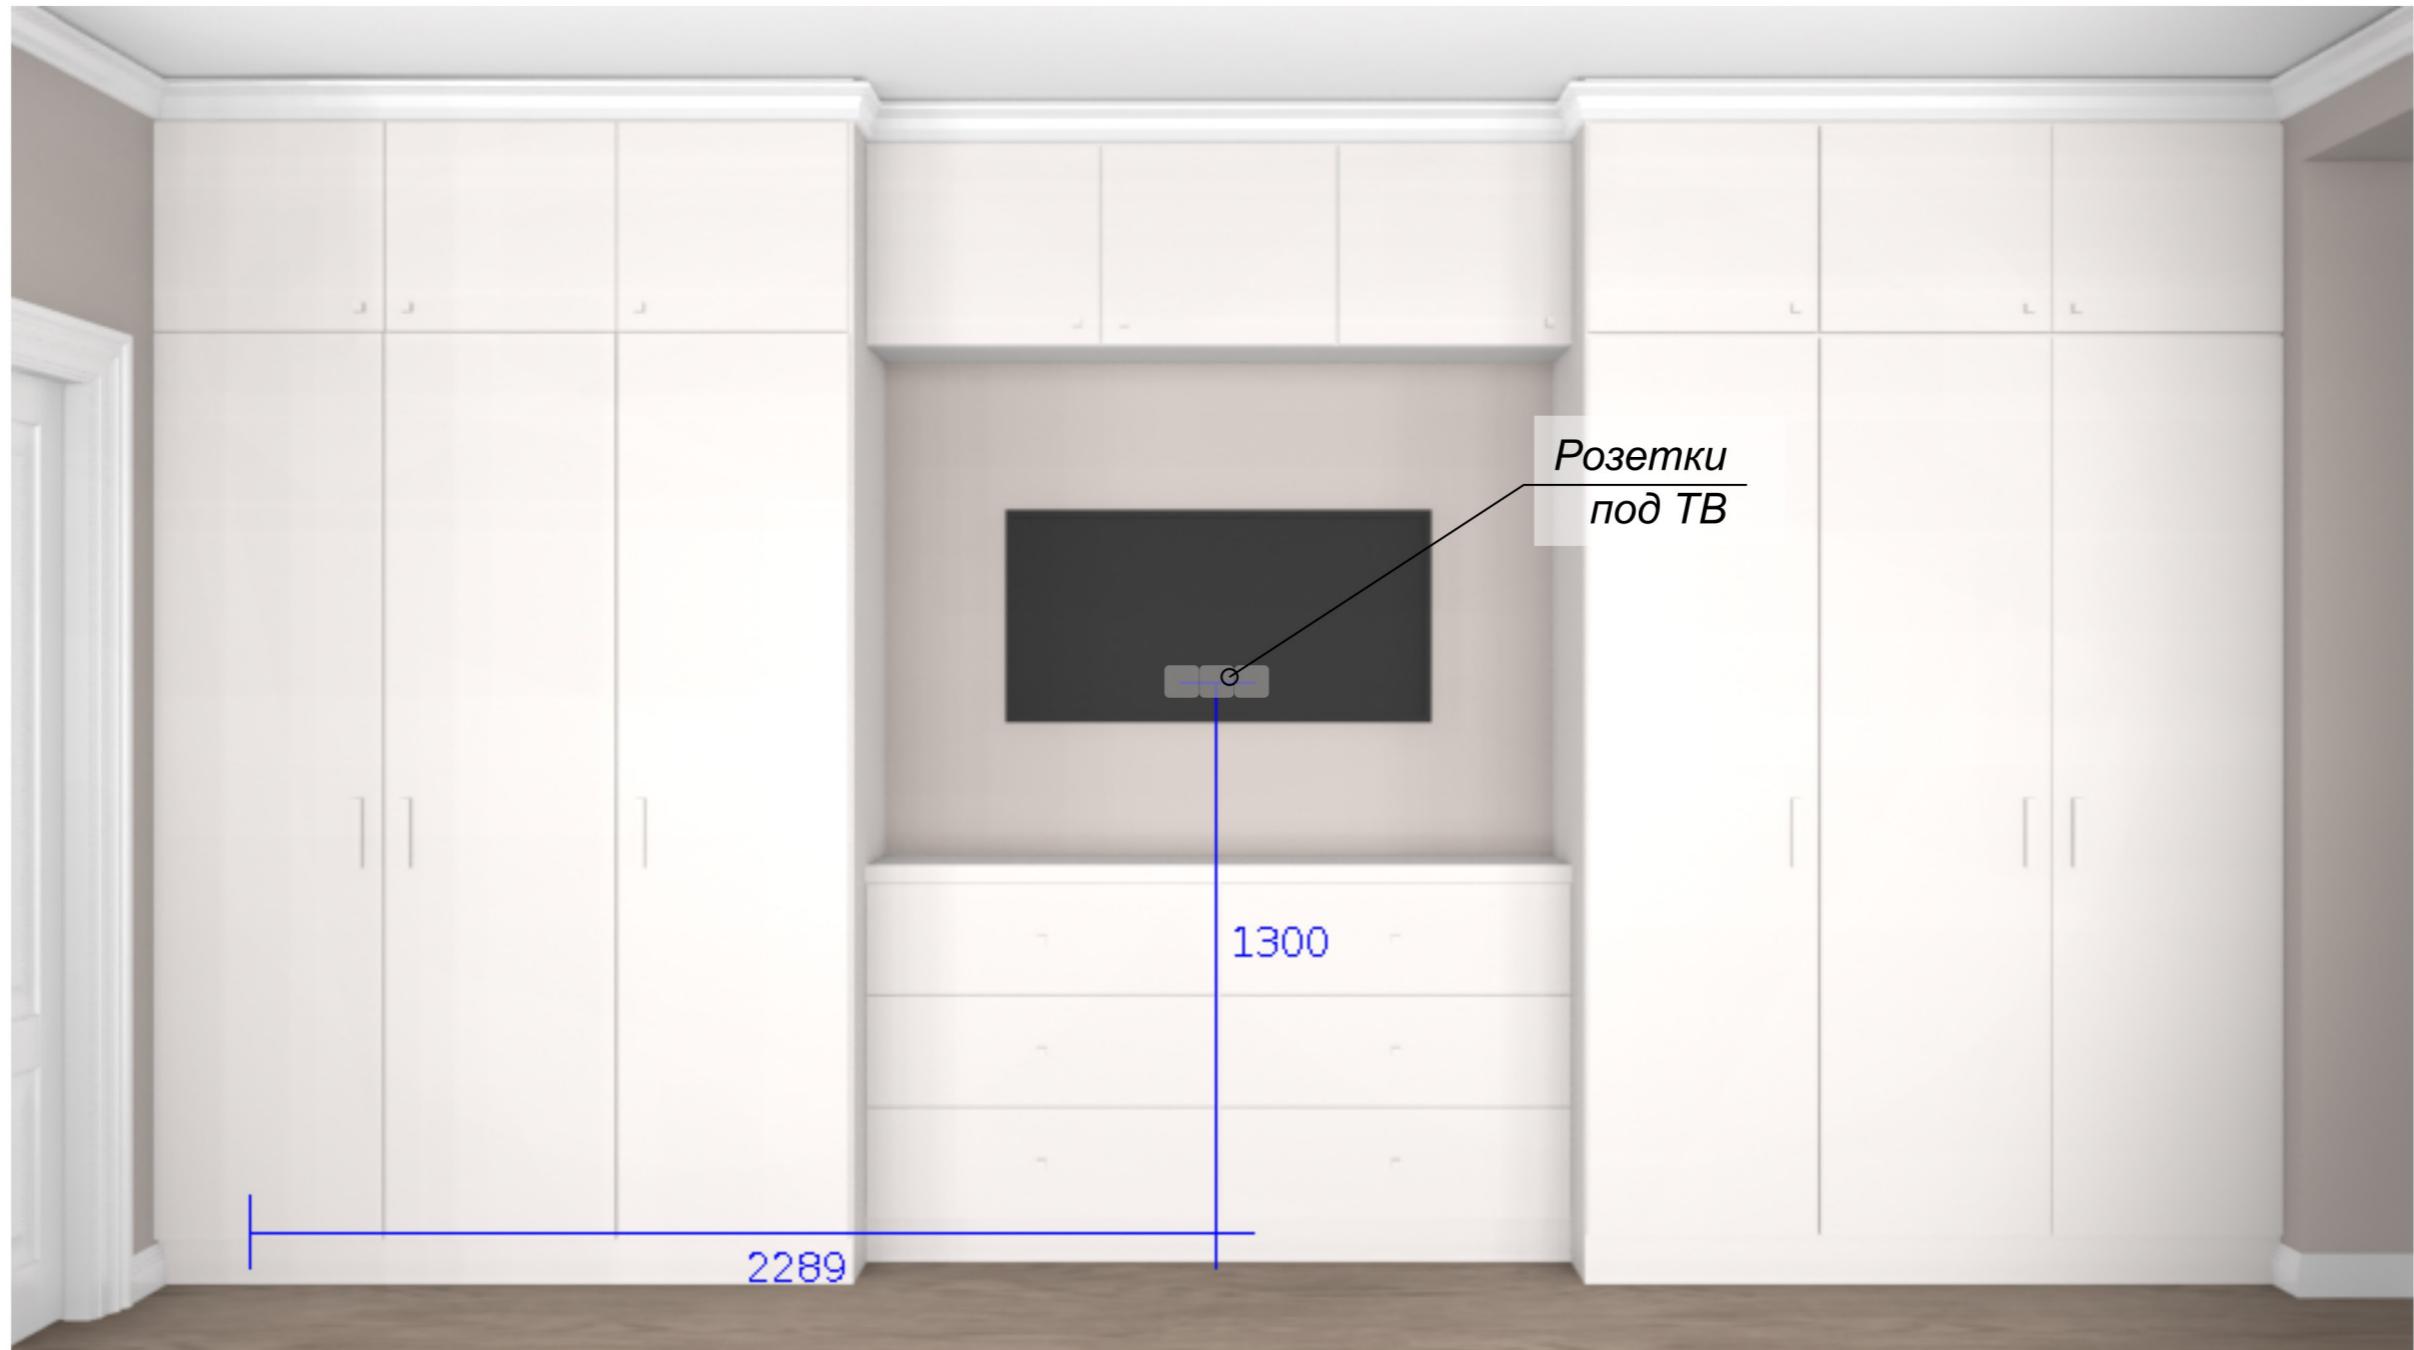

Инв. № подл.	Подл. и дата	Взам. инв. №	Согласовано

Спальня


Расположение розеток и выключателей стена 1-2

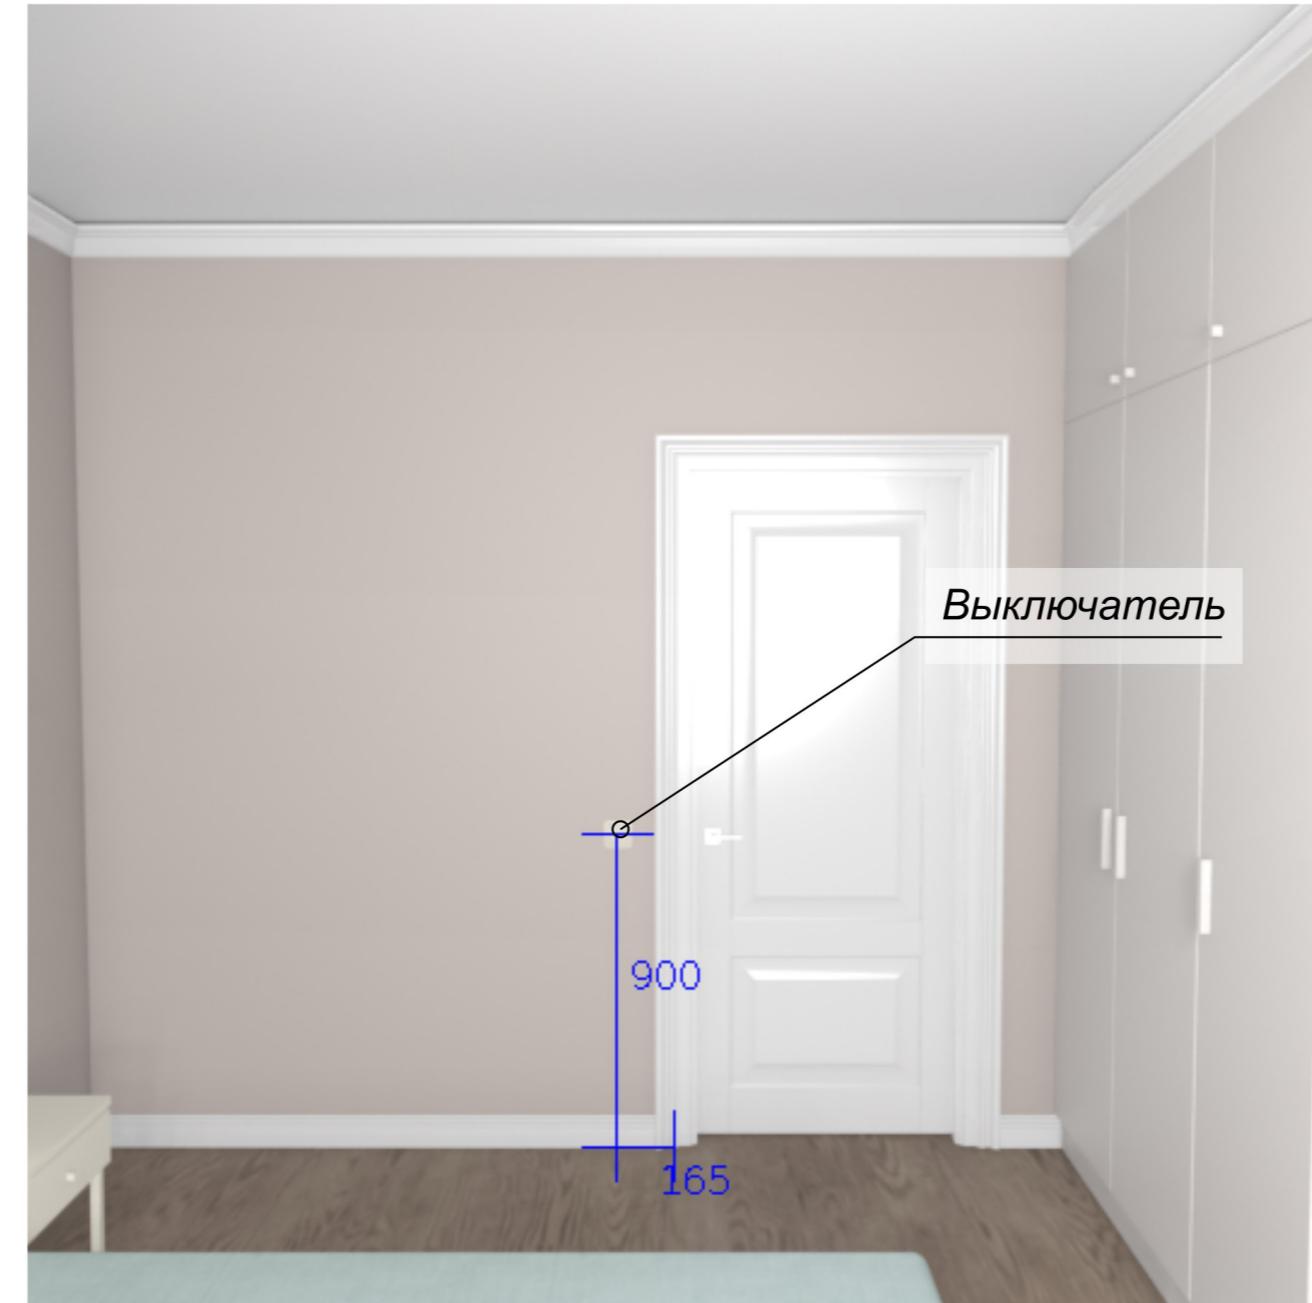

Инв. № подл.	Подл. и дата	Взам. инв. №	Согласовано

Гостиная


Расположение розеток и выключателей стена 7-8

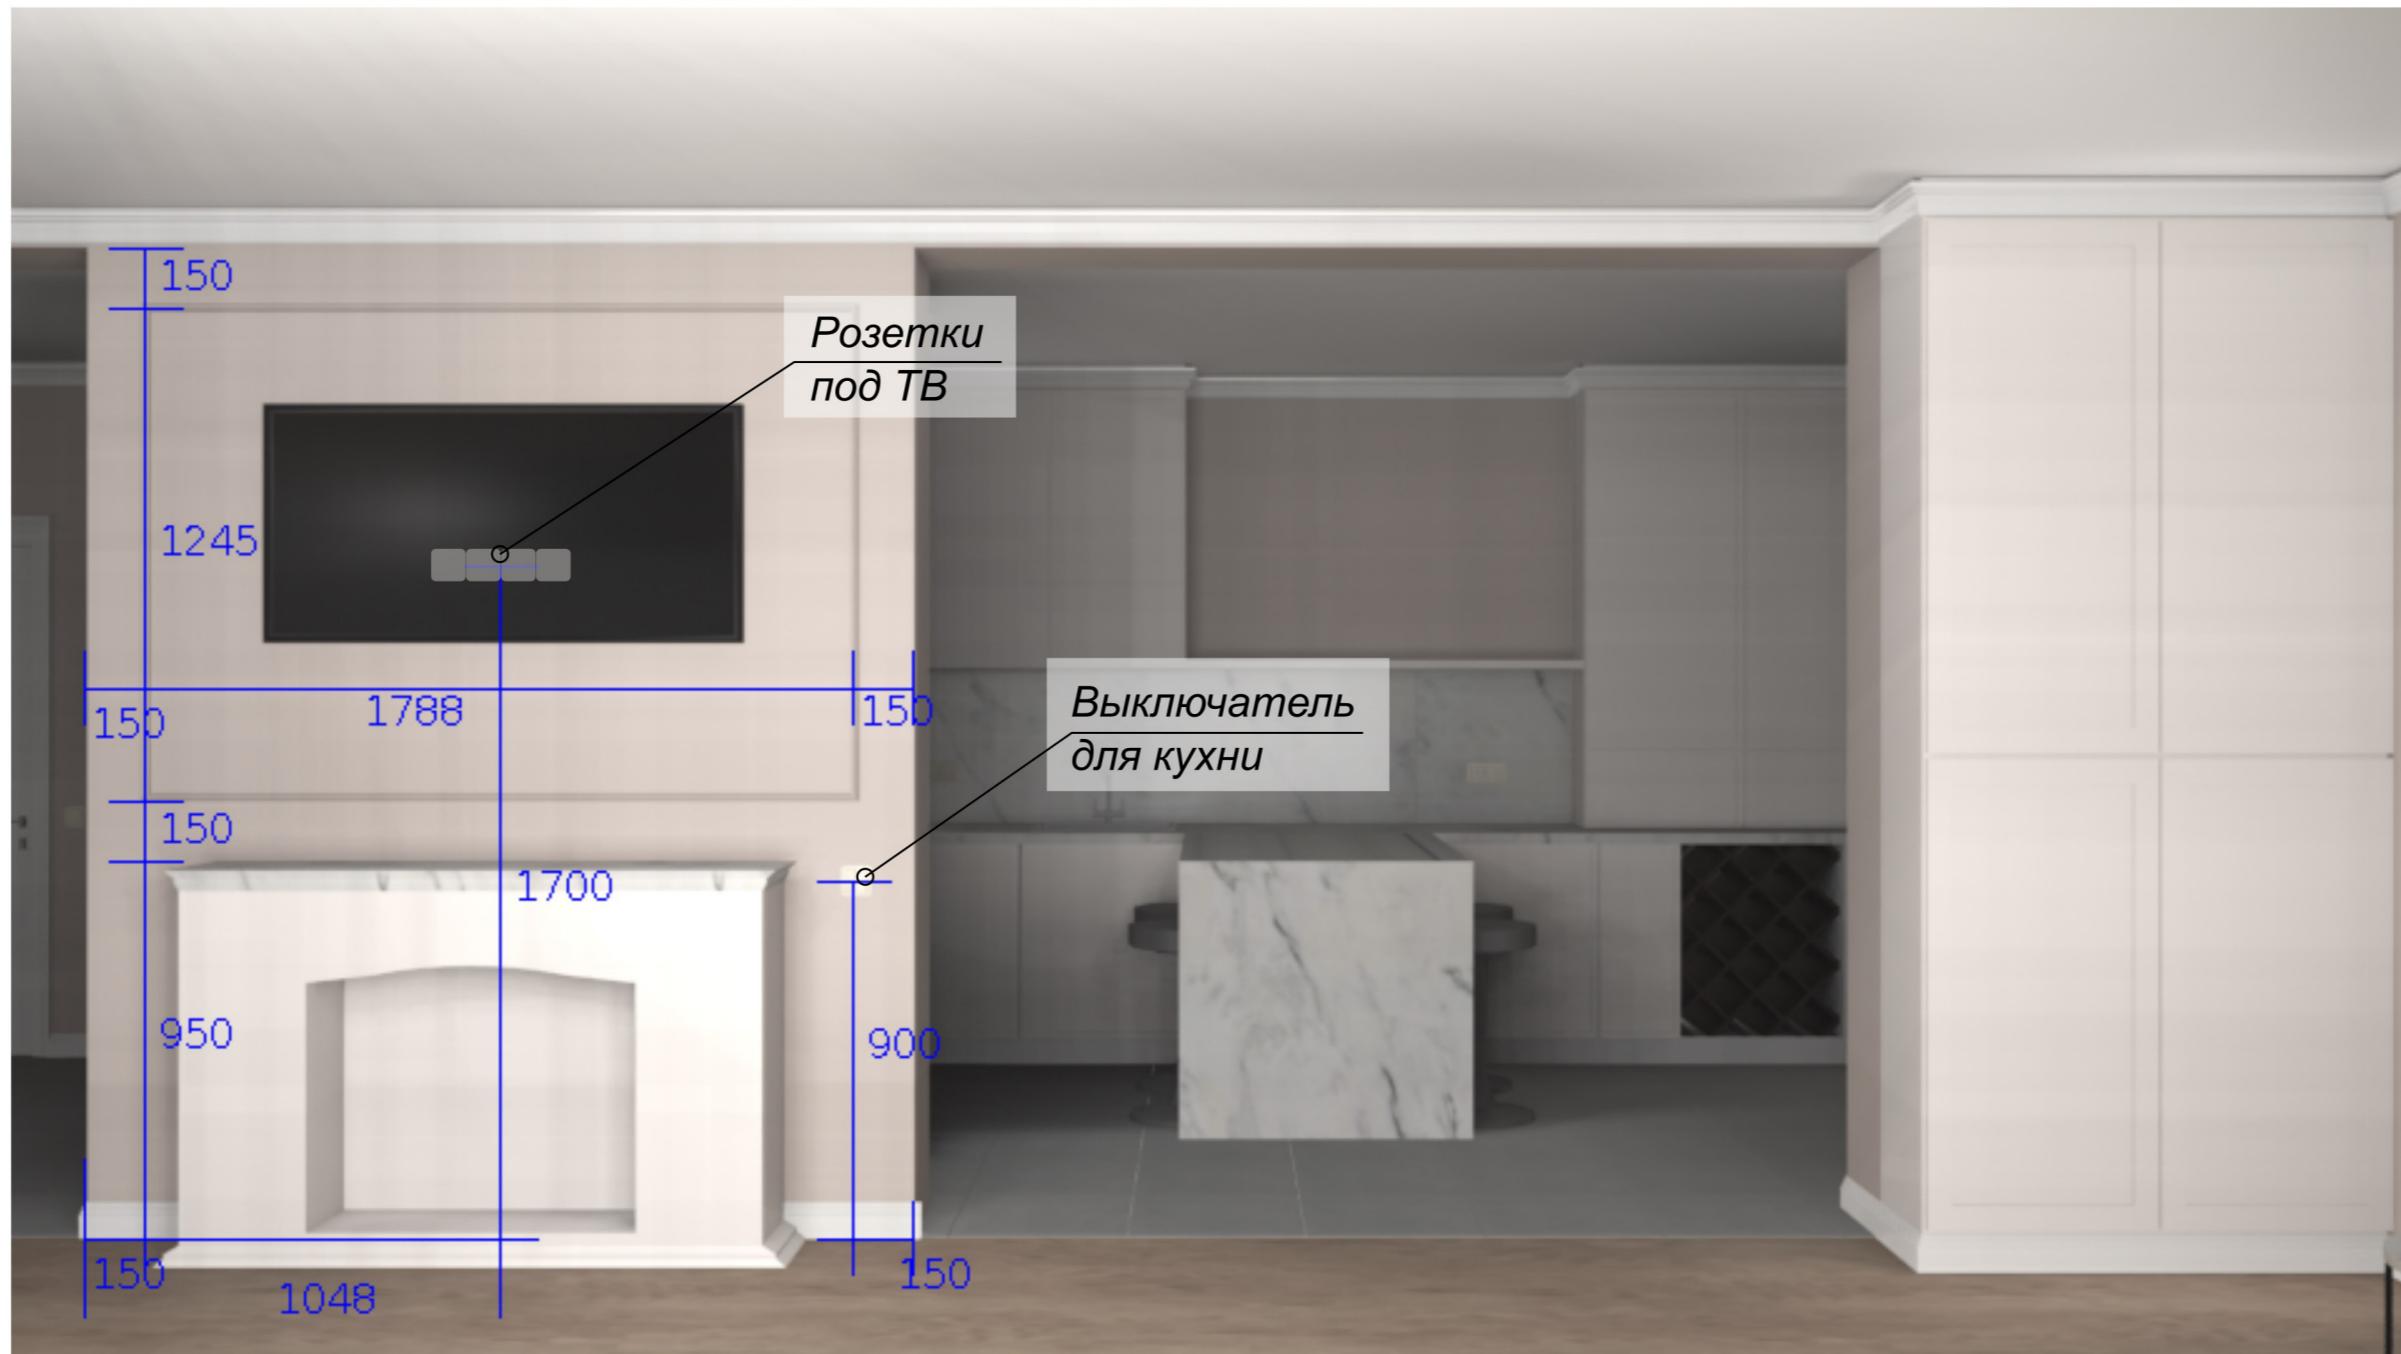

Согласовано		
Инв. № подп.	Подп. и дата	Взам. инв. №

Гостиная

Гостиная расположение розеток и выключателей стена 9-10

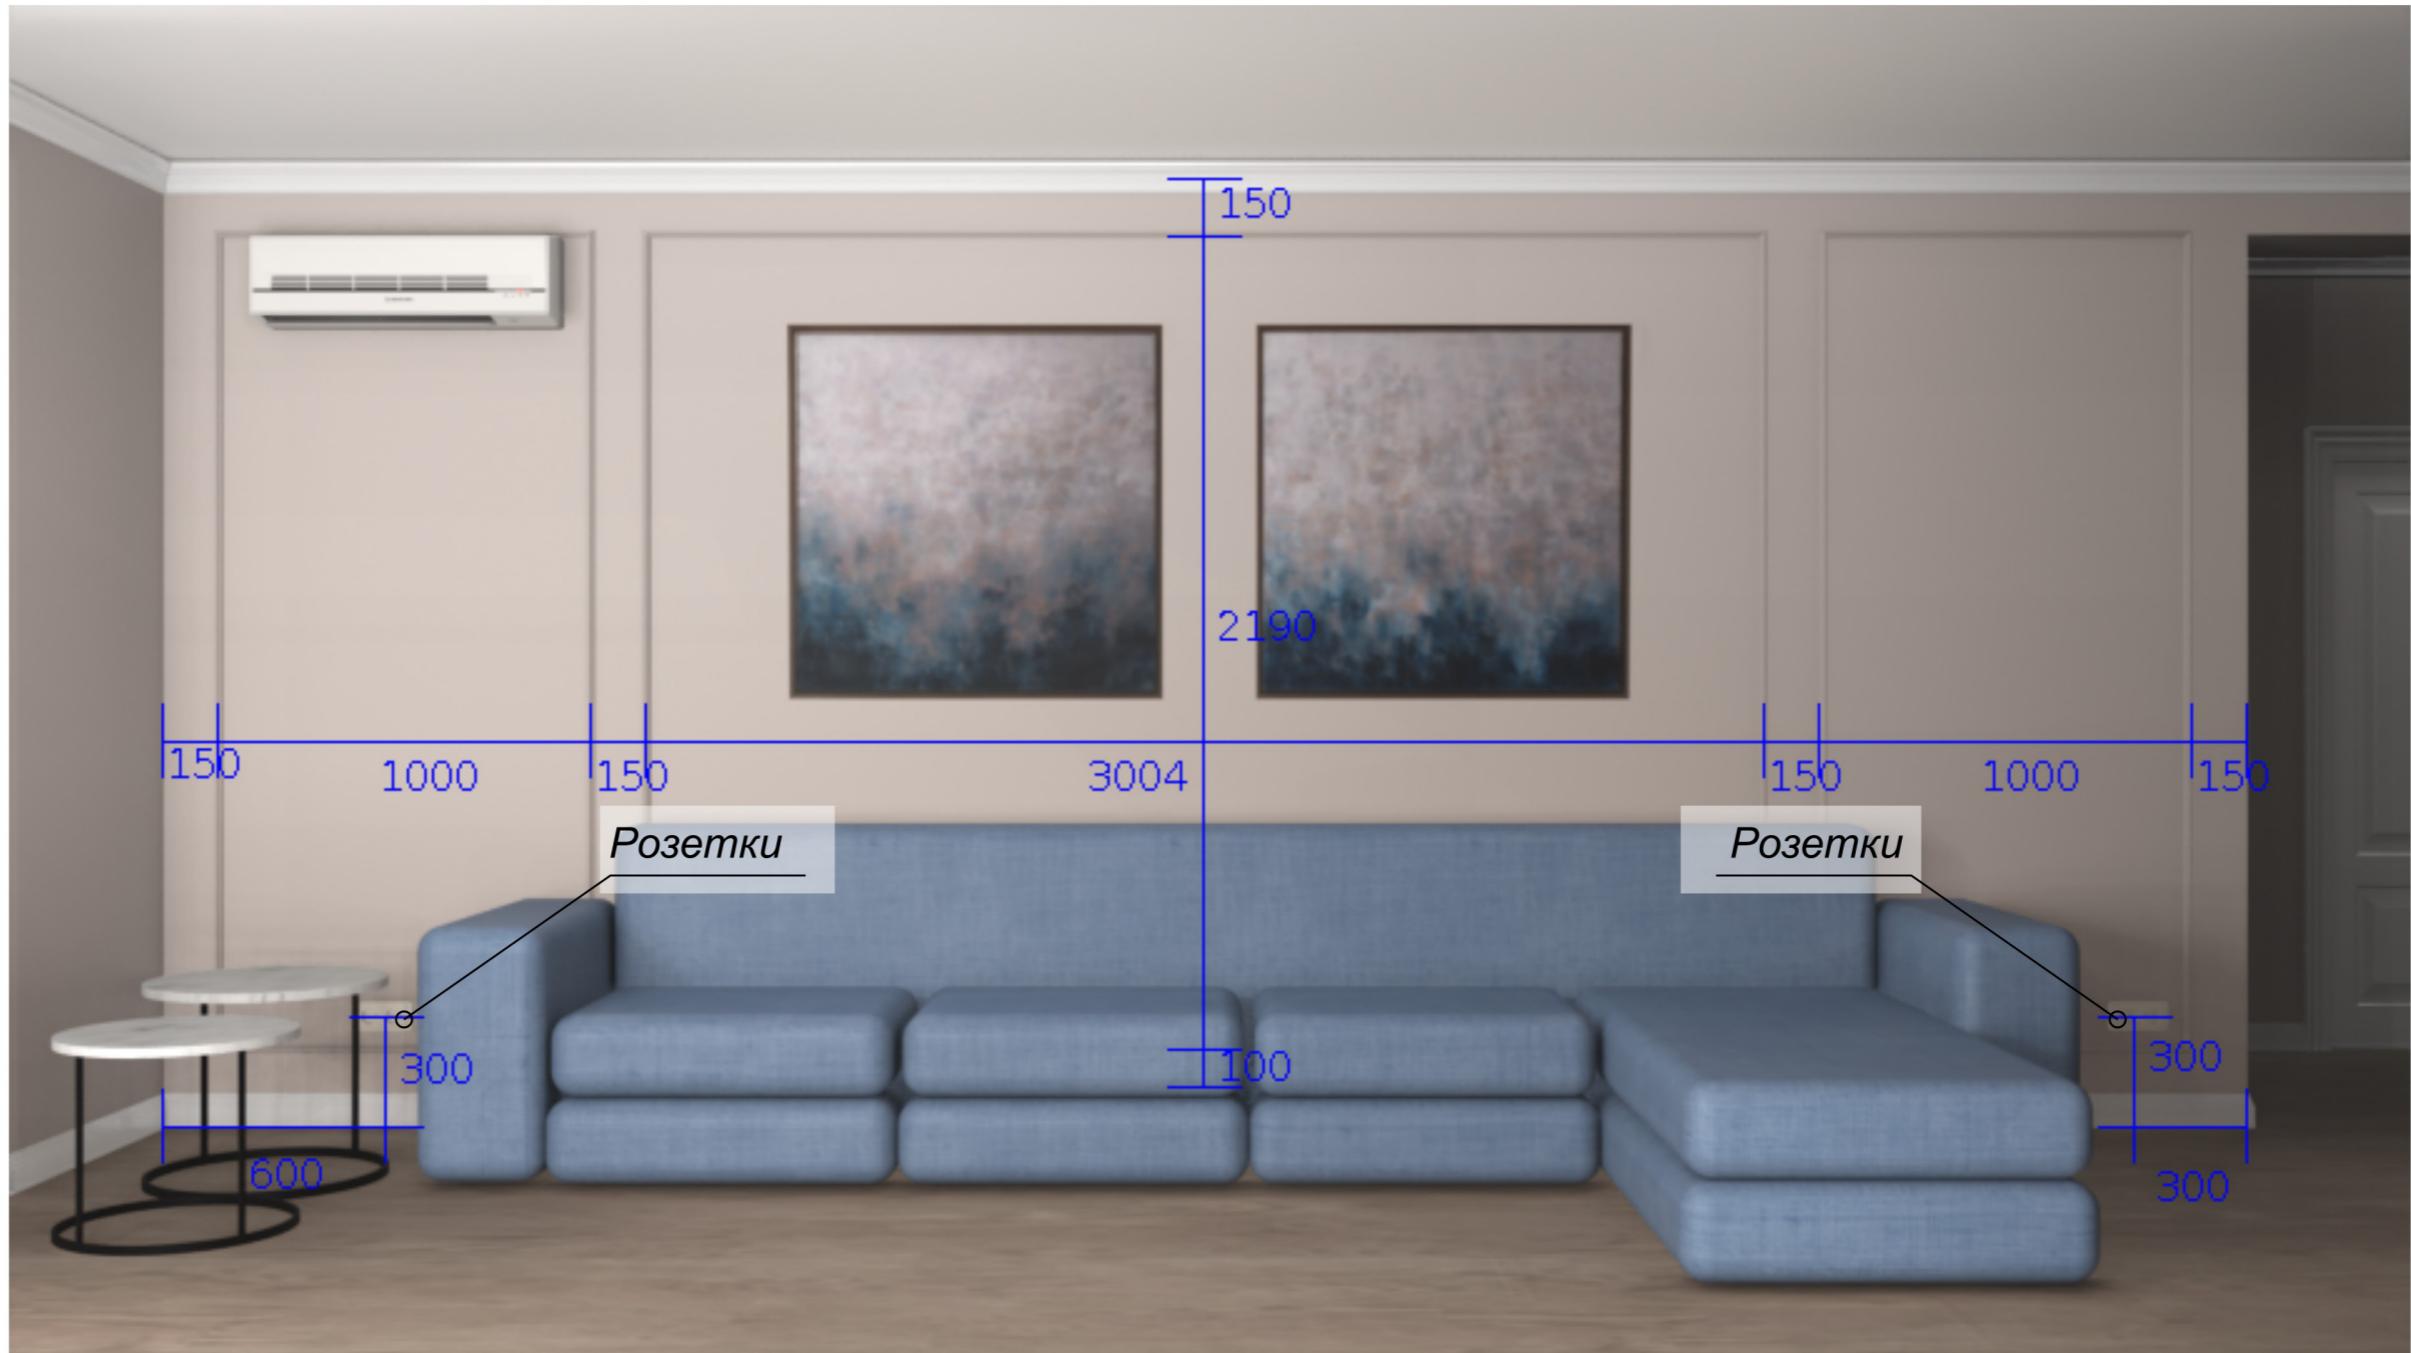

Согласовано

Инв. № подл. Подп. и дата Взам. инв. №

Детская

Детская комната общий вид




Согласовано

Инв. № подл. Подп. и дата Взам. инв. №

Детская

Детская расположение розеток и выключателей стена 4-1

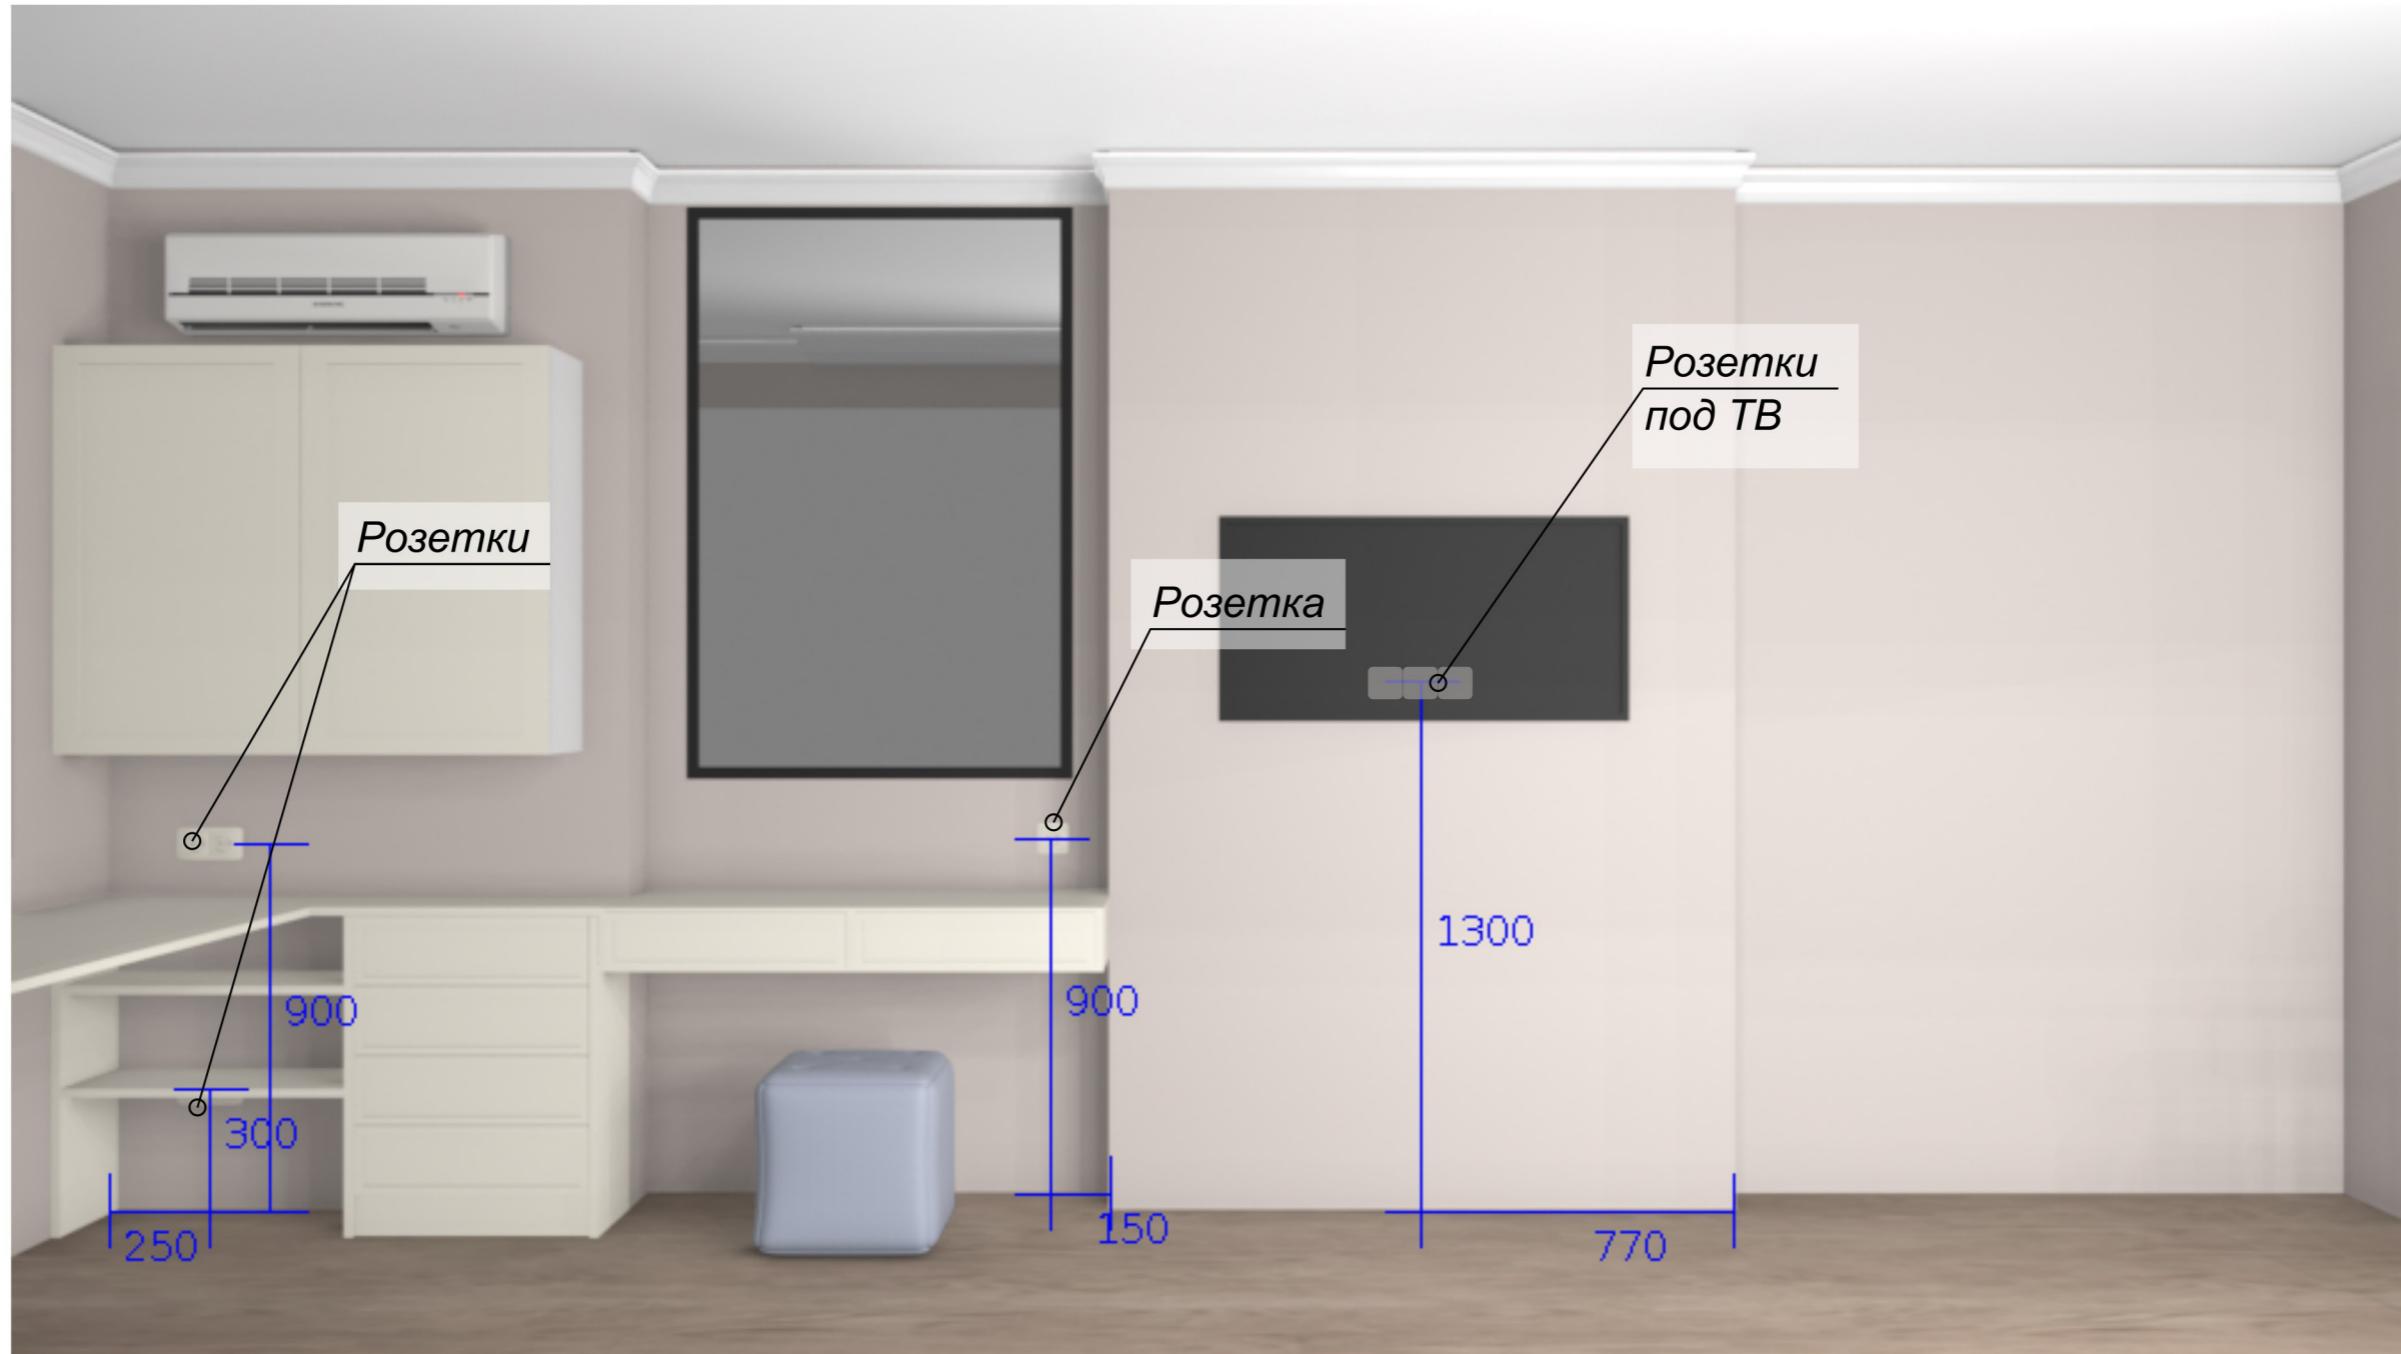

Инв. № подп.	Подп. и дата	Взам. инв. №	Согласовано


Детская

Детская расположение розеток и выключателей стена 2-3



Детская

Детская расположение розеток и выключателей стена 1-2

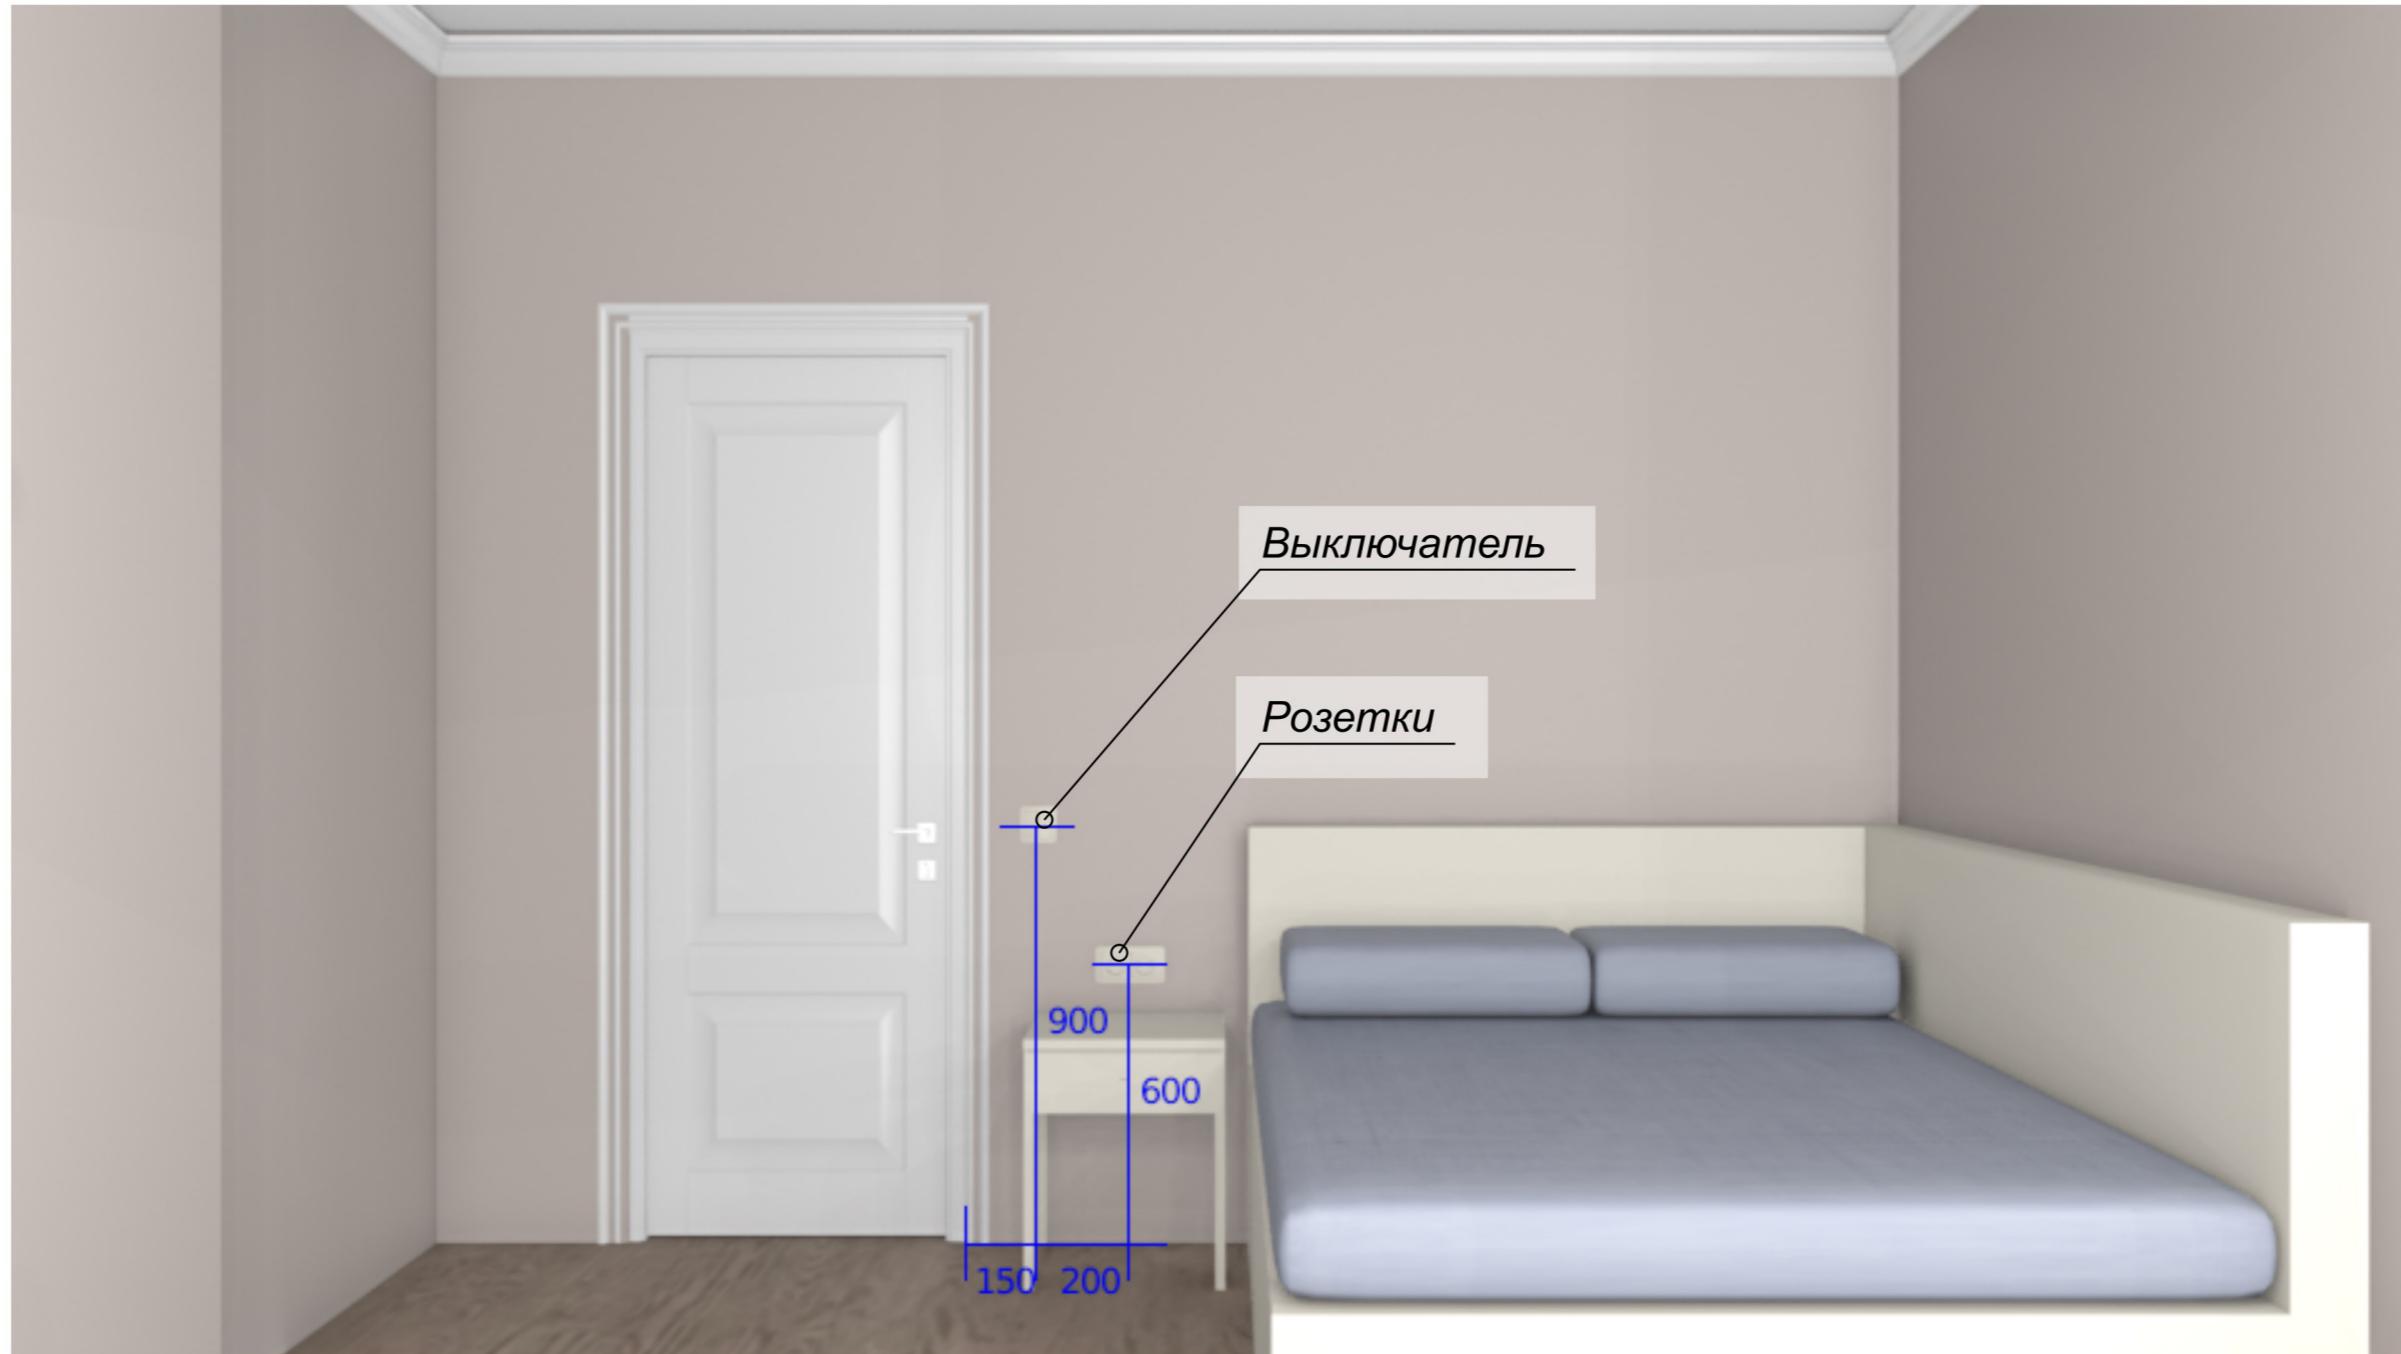

<i>Инв. № подл.</i>	<i>Подп. и дата</i>	<i>Взам. инв. №</i>

Условные обозначени

- отметка потолка
- отметка пола

- отметки верха проема;
- отметки низа проема;


- отметки верха проема


- канализационный стояк
- вентиляция

ПРИМЕЧАНИЯ

Съемка выполнена в условной системе координат X, Y и системе высот

Размеры на чертеже показаны в миллиметрах, отметки в метрах

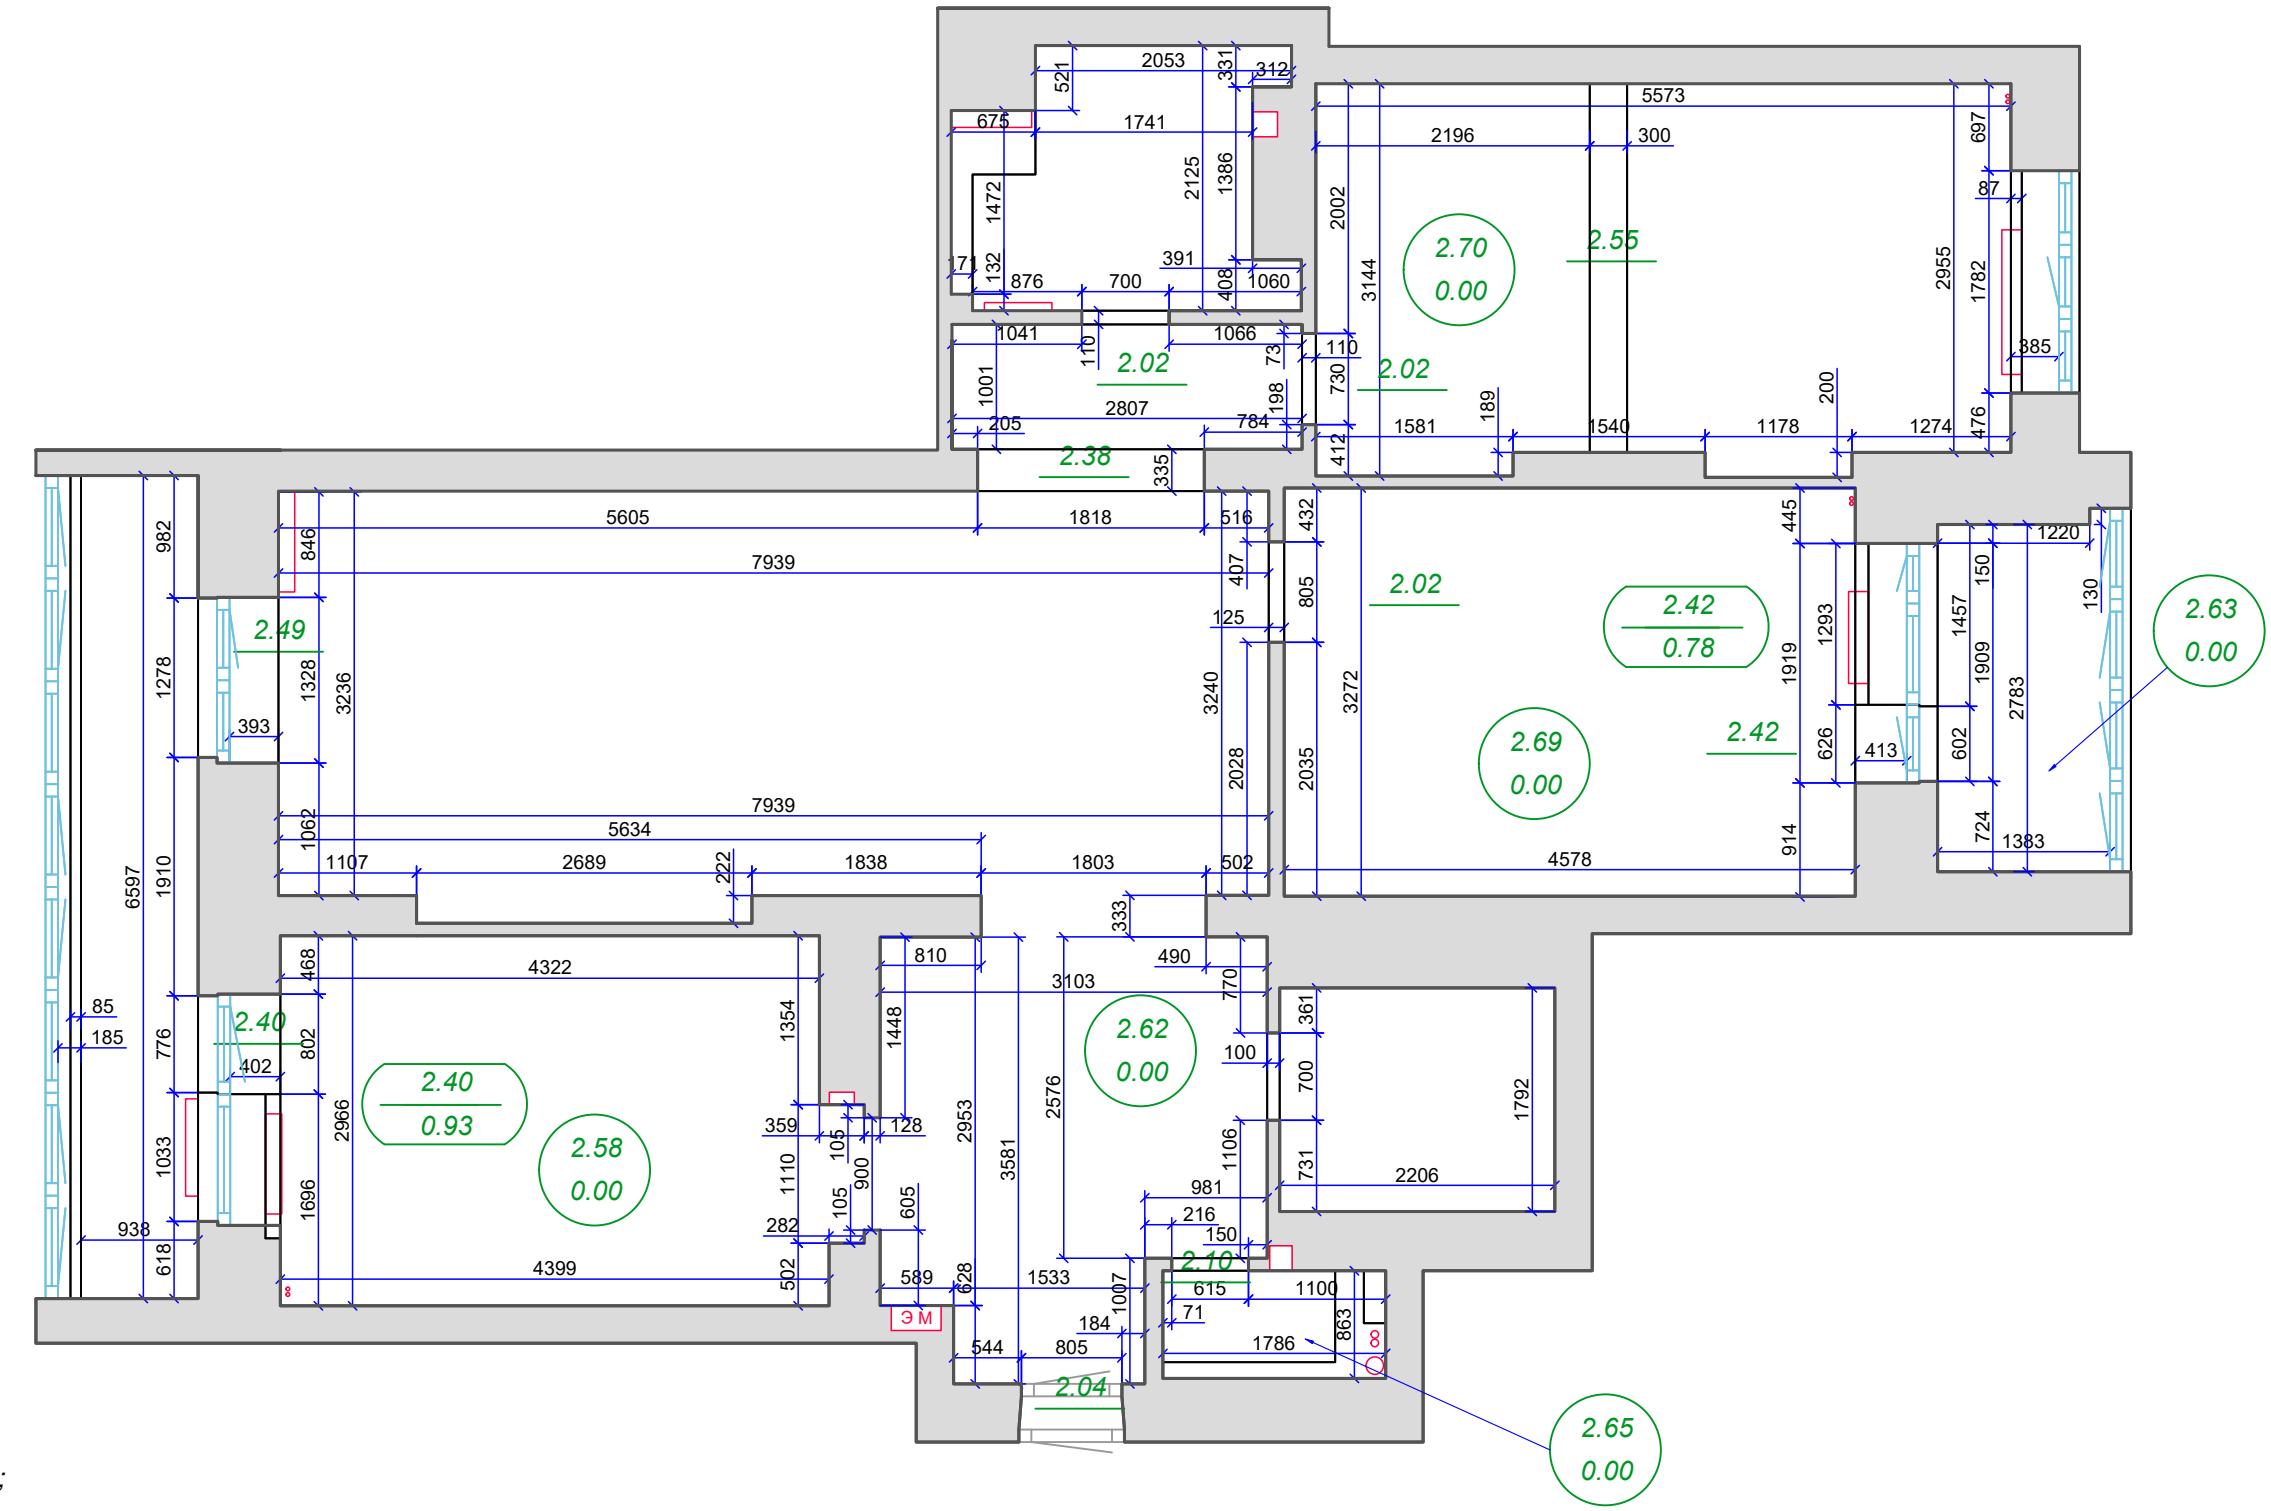

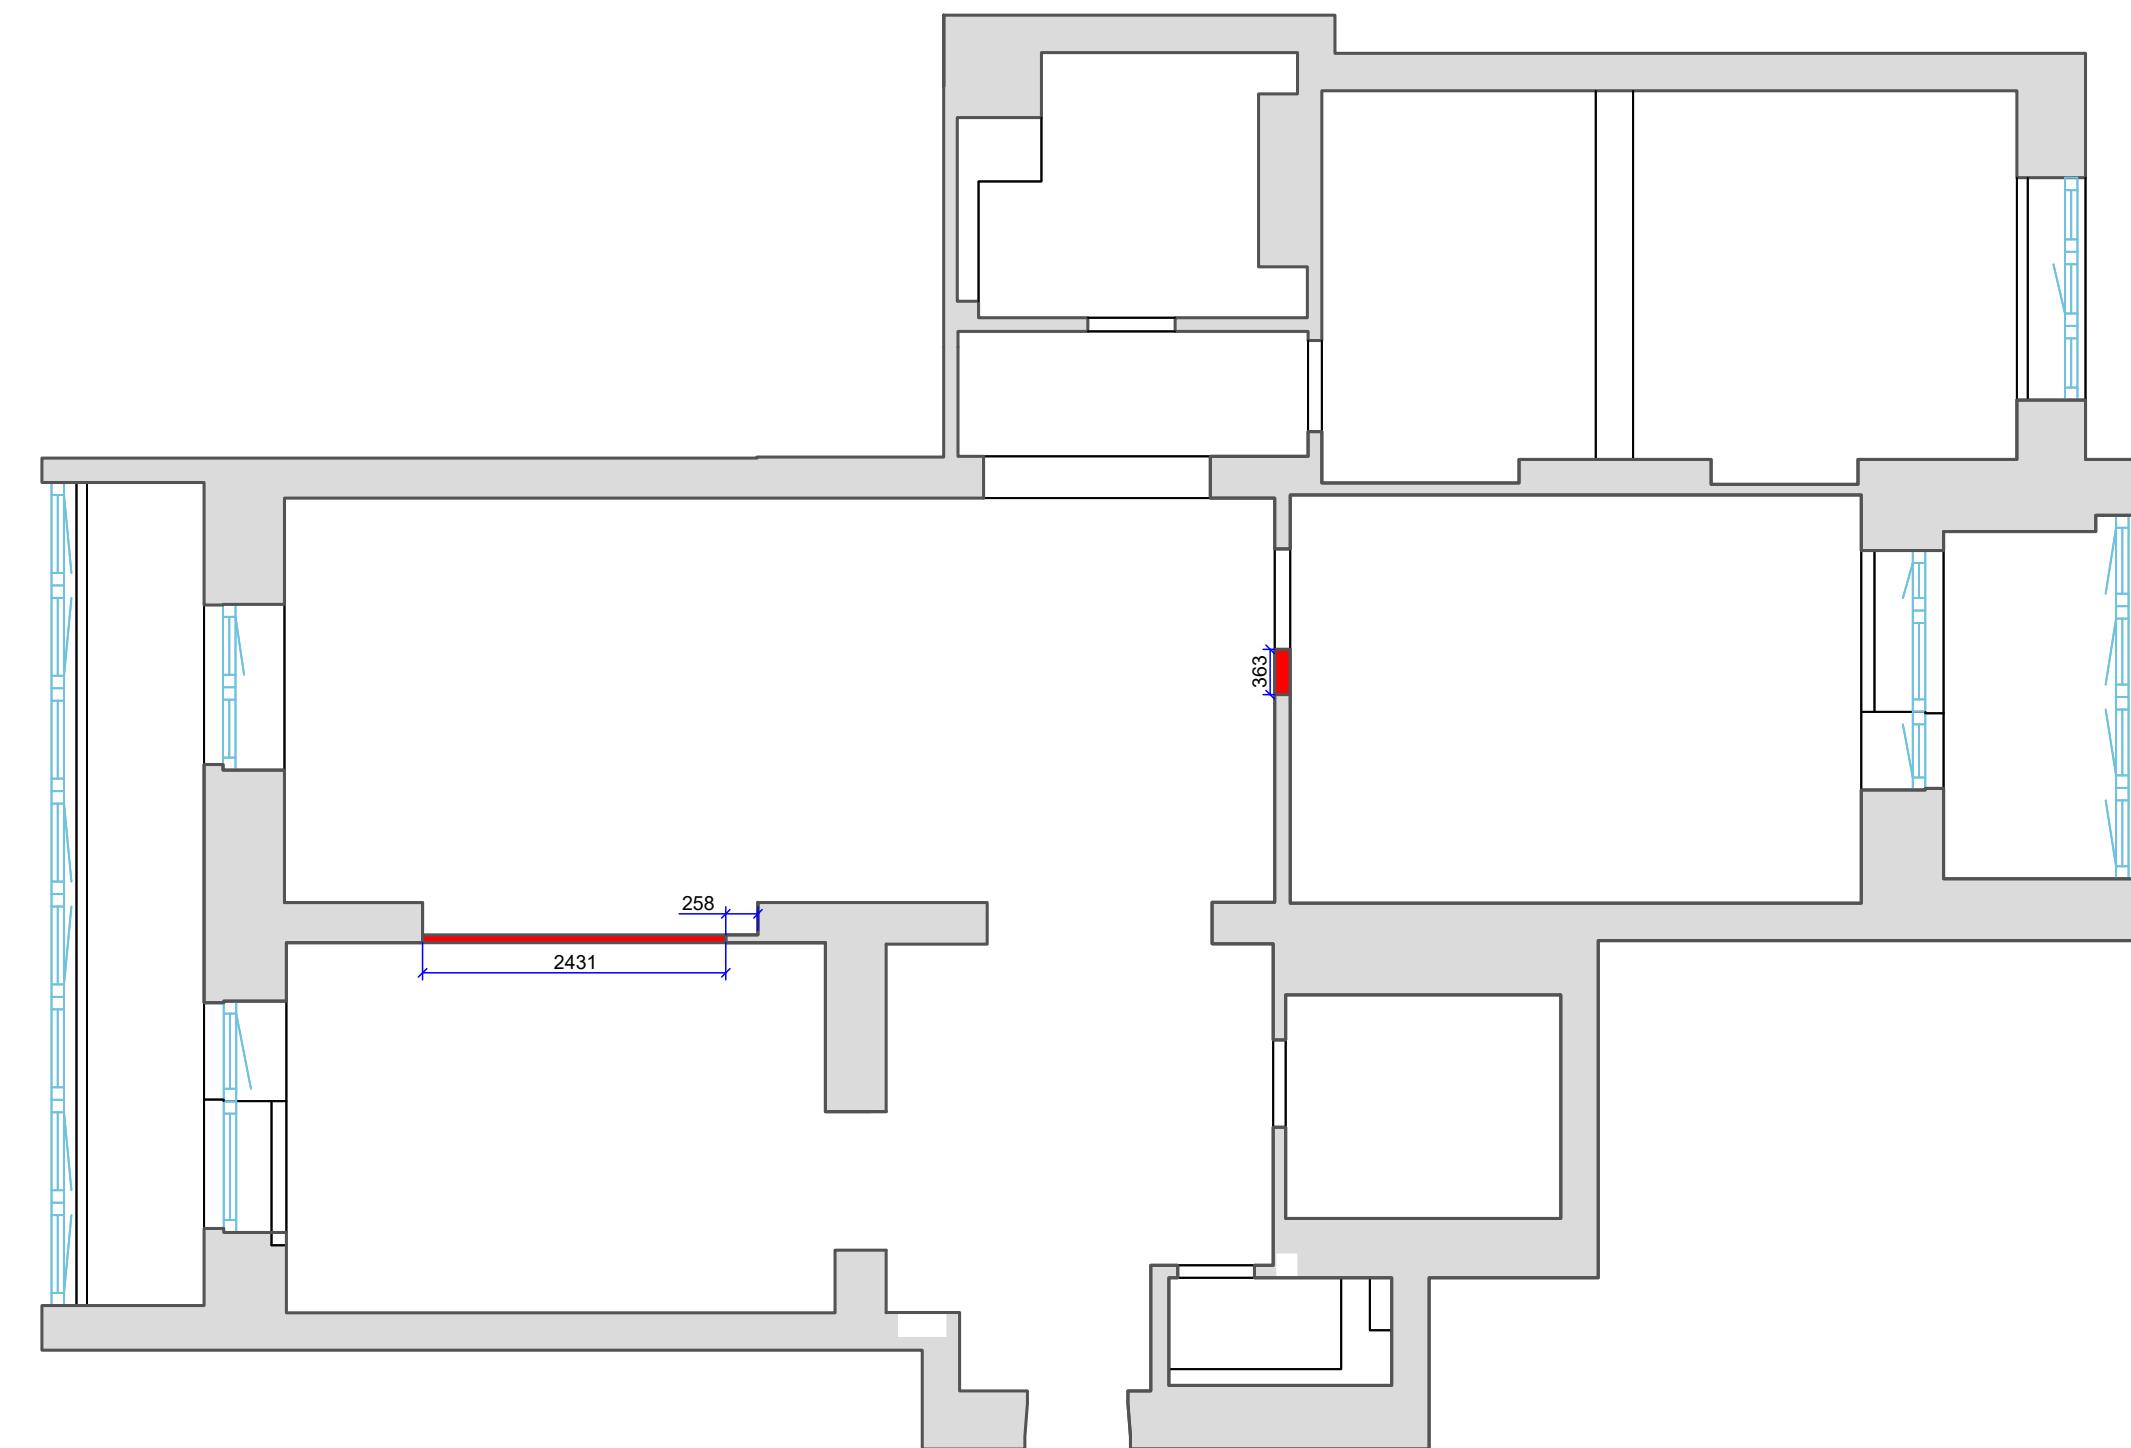

Условные обозначения

- демонтаж

Согласовано			
Инв. № подл.	Подп. и дата	Взам.инв.№	

Изм.	Кол.уч	Лист	№док	Подпись Дата
Н.контр				




Условные обозначения

- возводимые конструкции

<i>2000</i>	- отметки верха проема ниши
<i>800</i>	- отметки низа проема ниши

2.10 - отметки верха проема

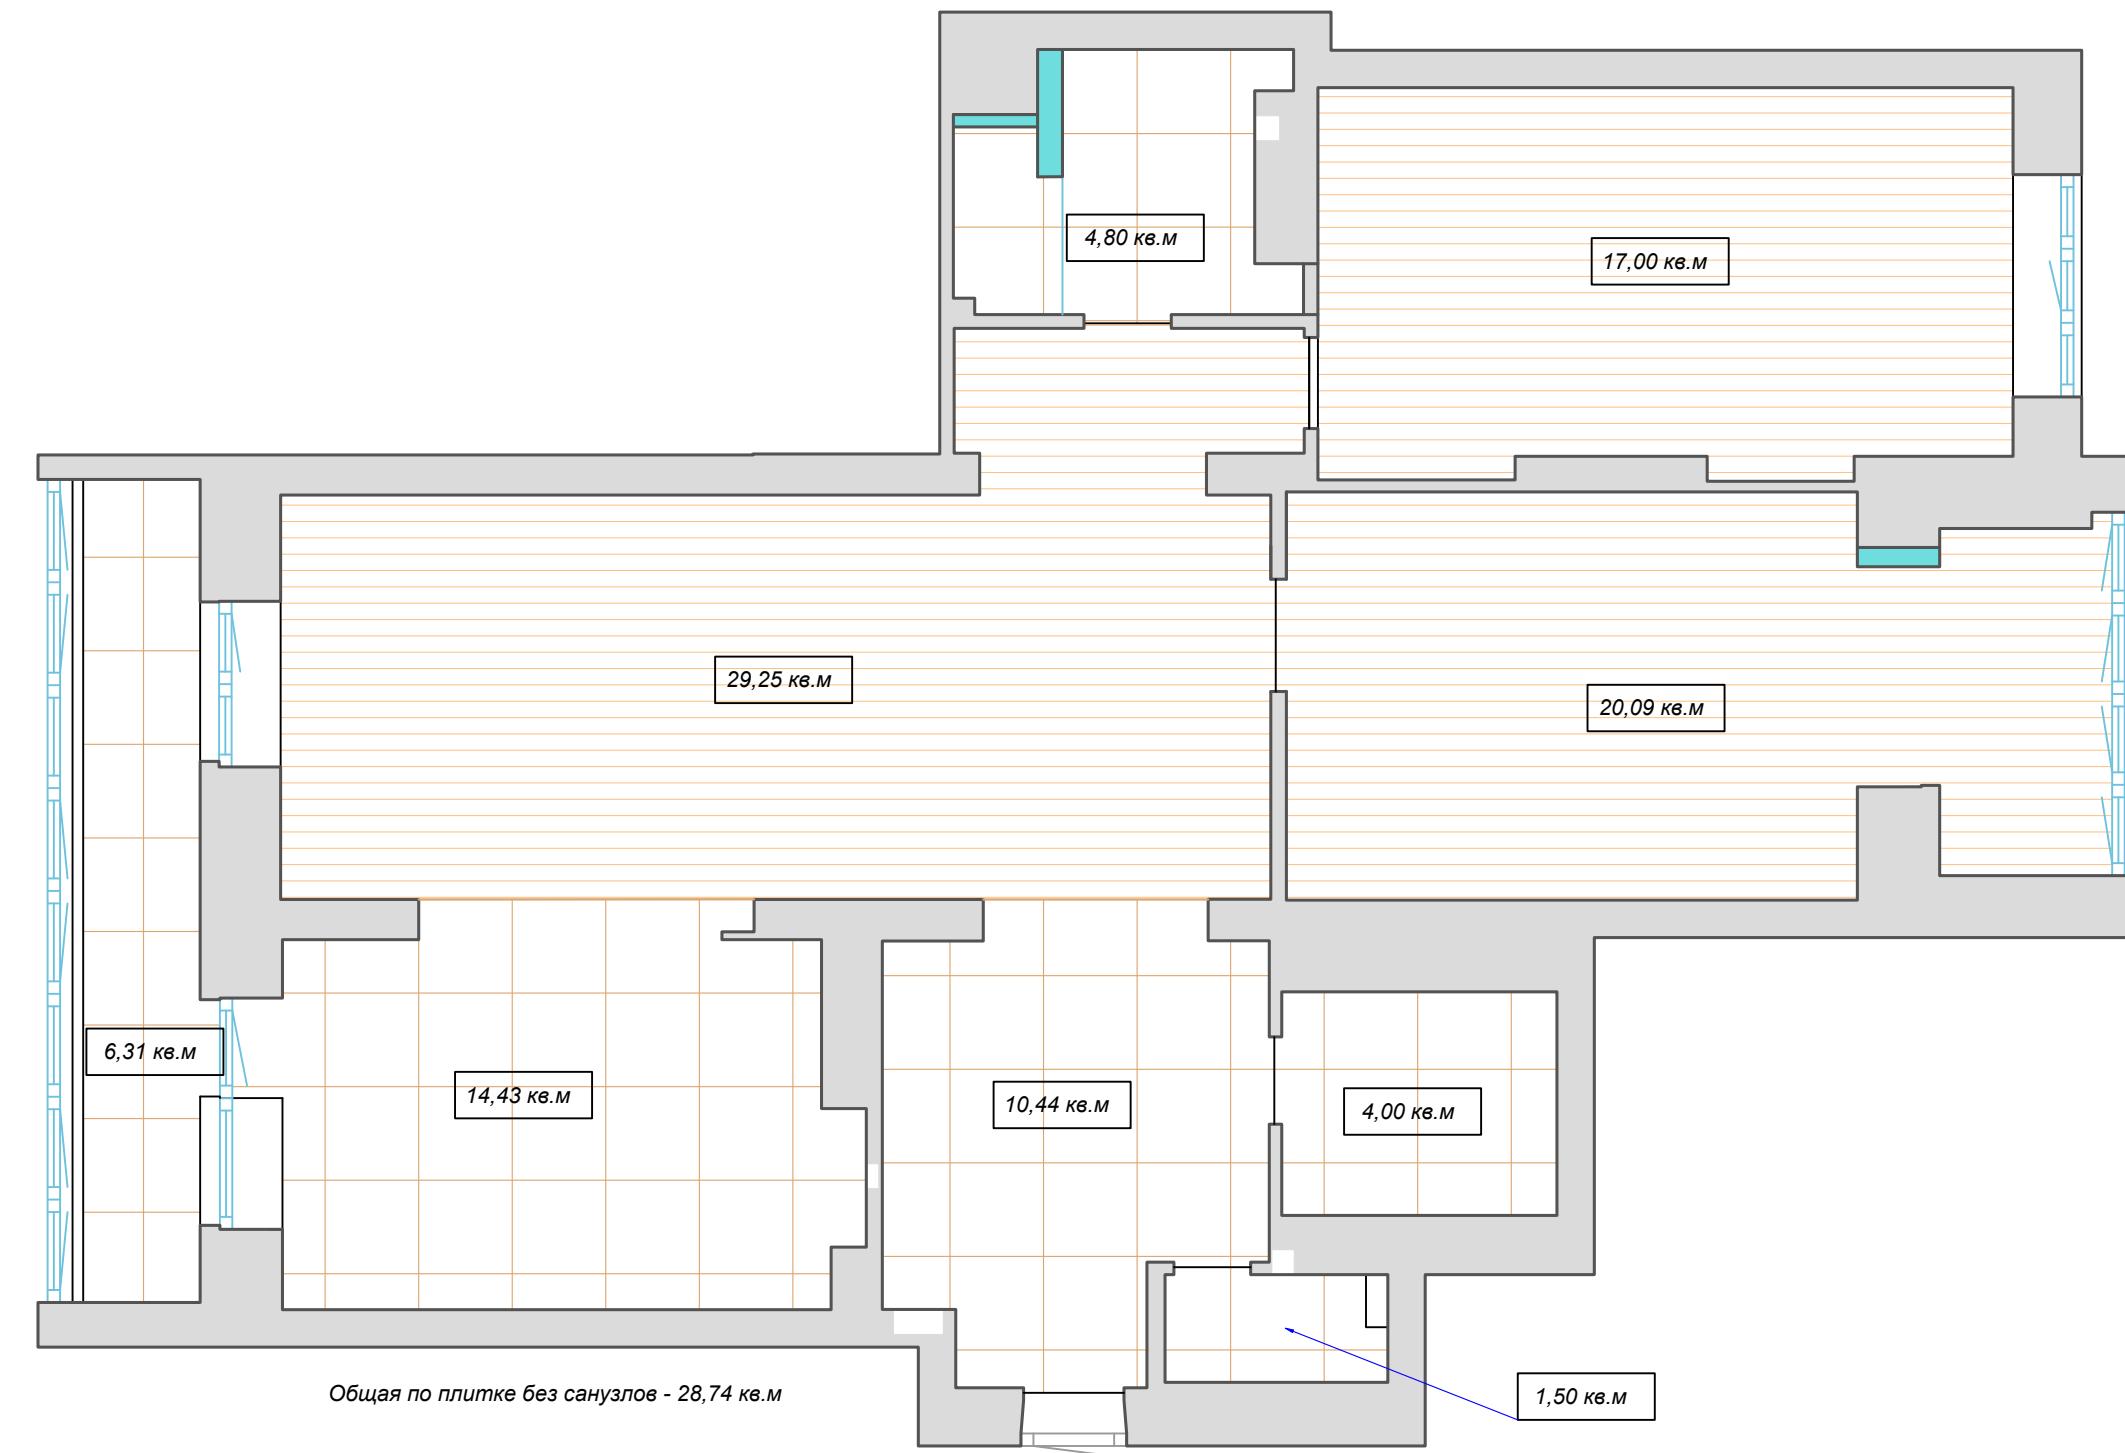


Примечания

*Соединение напольных покрытий под серединой дверного полотна

Условные обозначения

15,12 кв.м		- плитка
		- паркетная доска

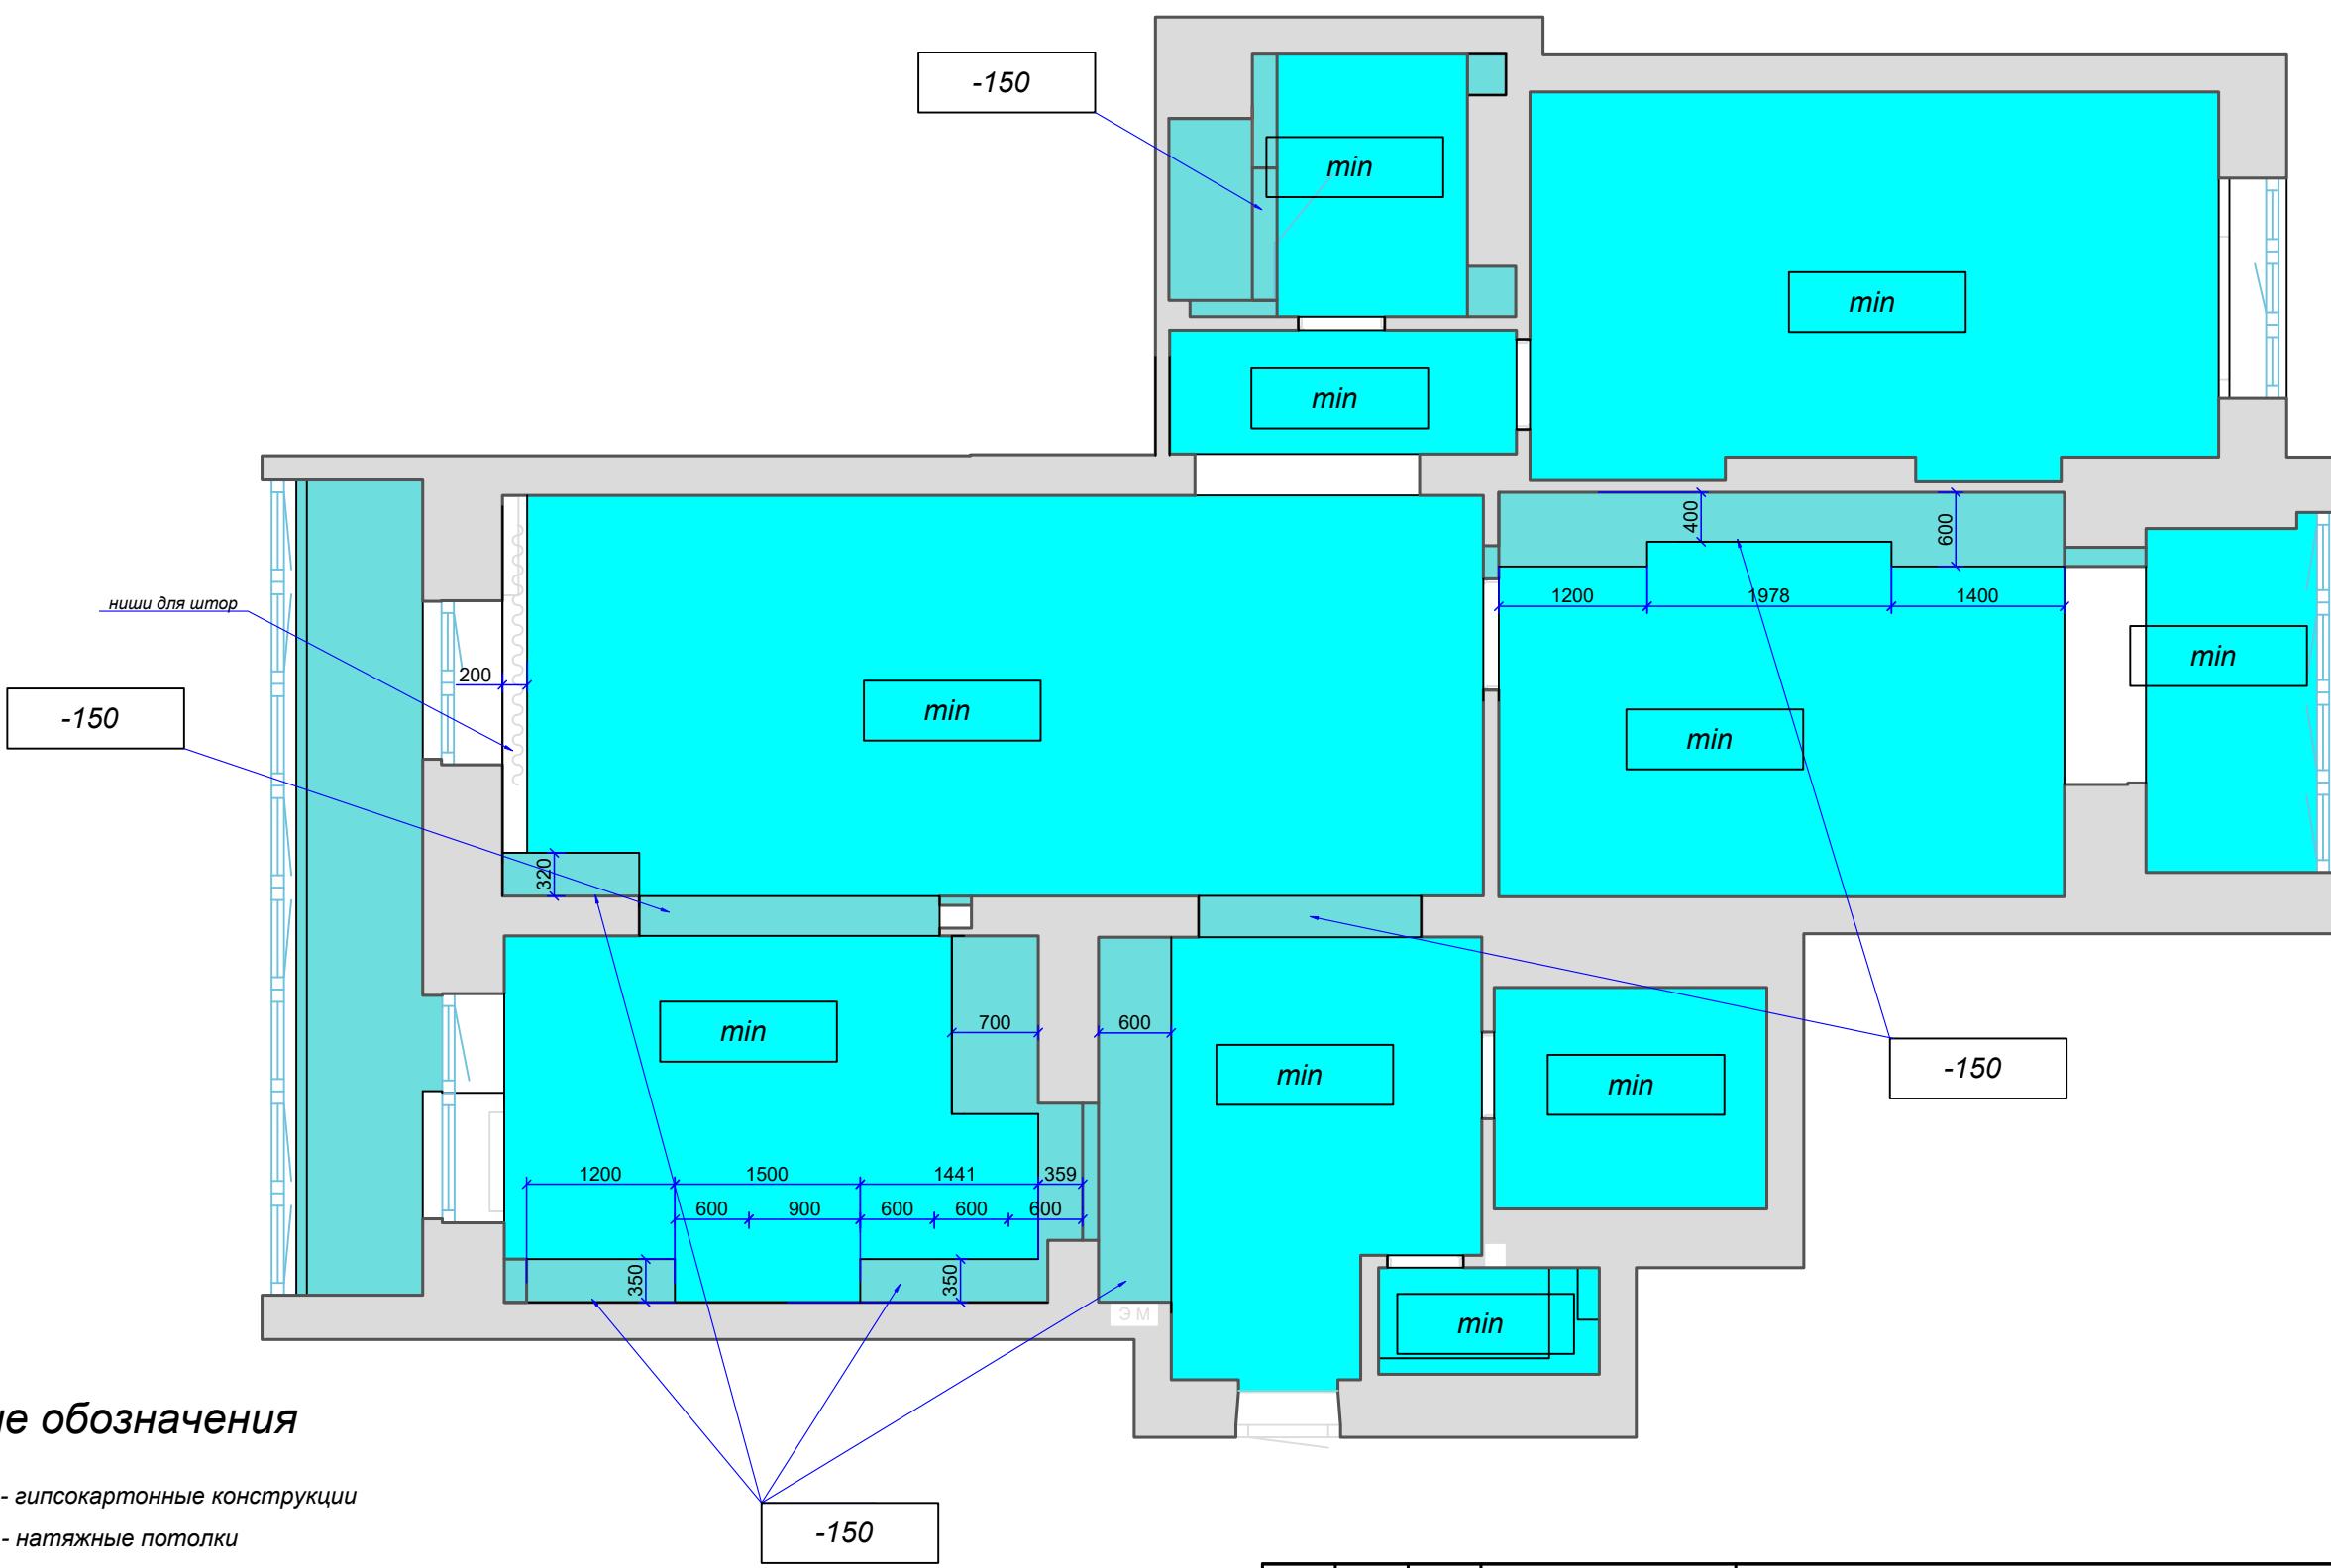

Условные обозначения

- гипсокартонные конструкции
 - натяжные потолки

-100 - отступ от уровня существующего потолка

min


Примечание

Отступ потолка со встроенными точечными светильниками согласовать с глубиной их встраивания

Изм.	Кол.уч	Лист	№док	Подпись Дата
Н.контр				

План потолочных конструкций

Квартира	СТАДИЯ	ЛИСТ	ЛИСТОВ
	Р.П.	28	40
План			

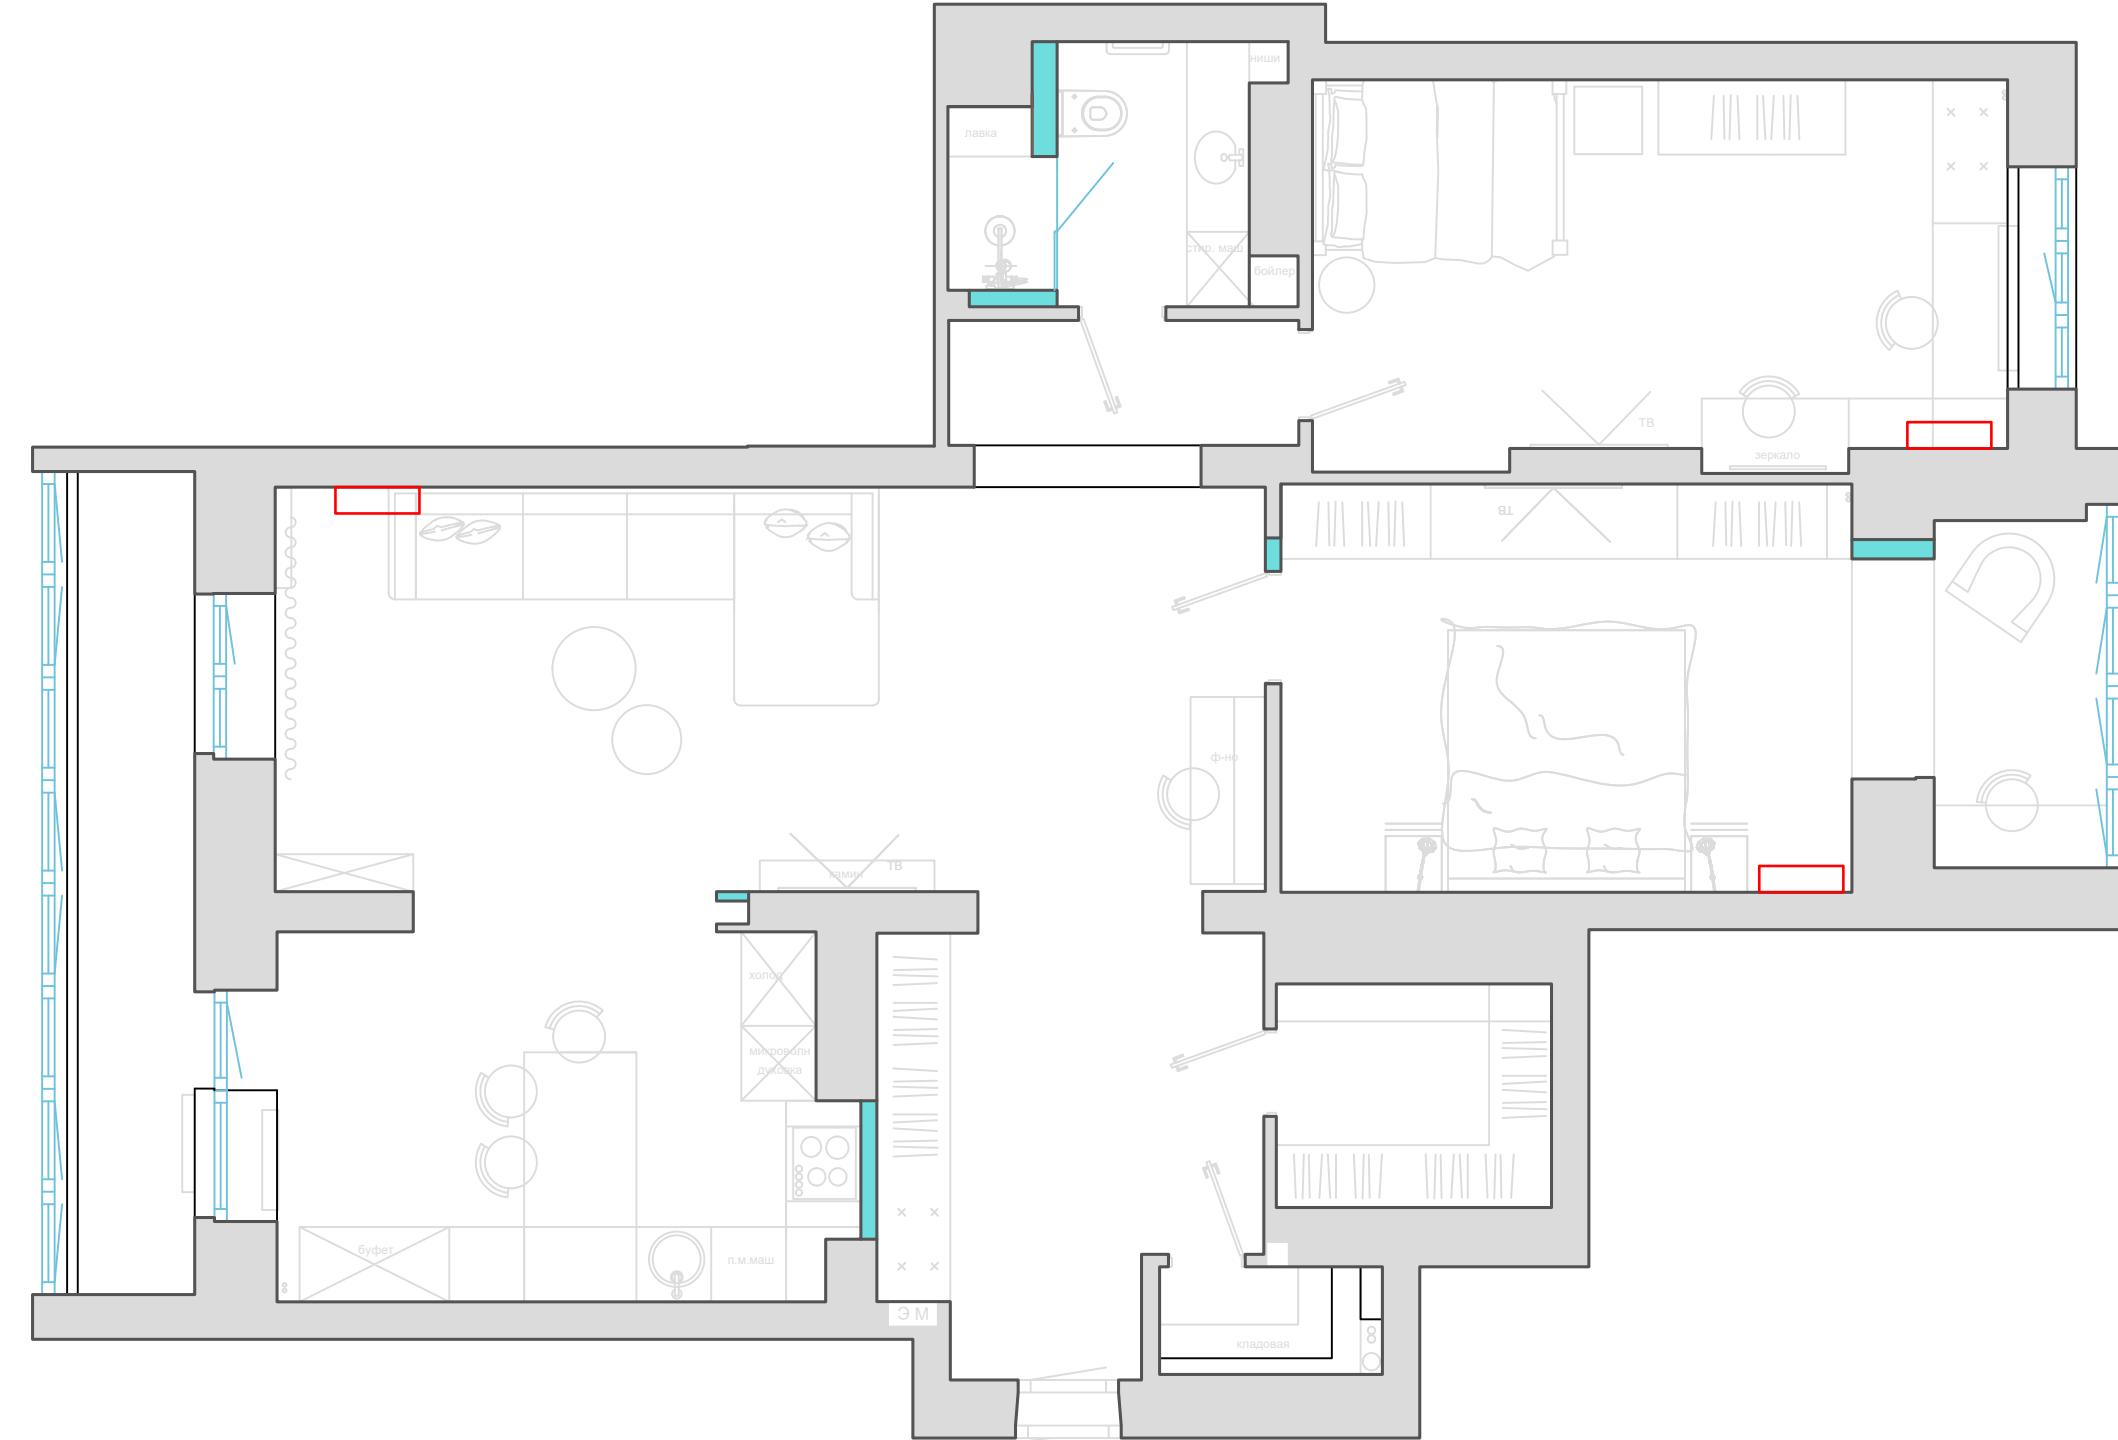

Условные обозначения


- внутренний блок кондиционера

Изм.	Кол.уч	Лист	№док	Подпись Дата
<i>Н.контр</i>				

План размещения кондиционеров

	Квартира	СТАДИЯ	ЛИСТ	ЛИСТОВ
		<i>R.П.</i>	29	40
	План			



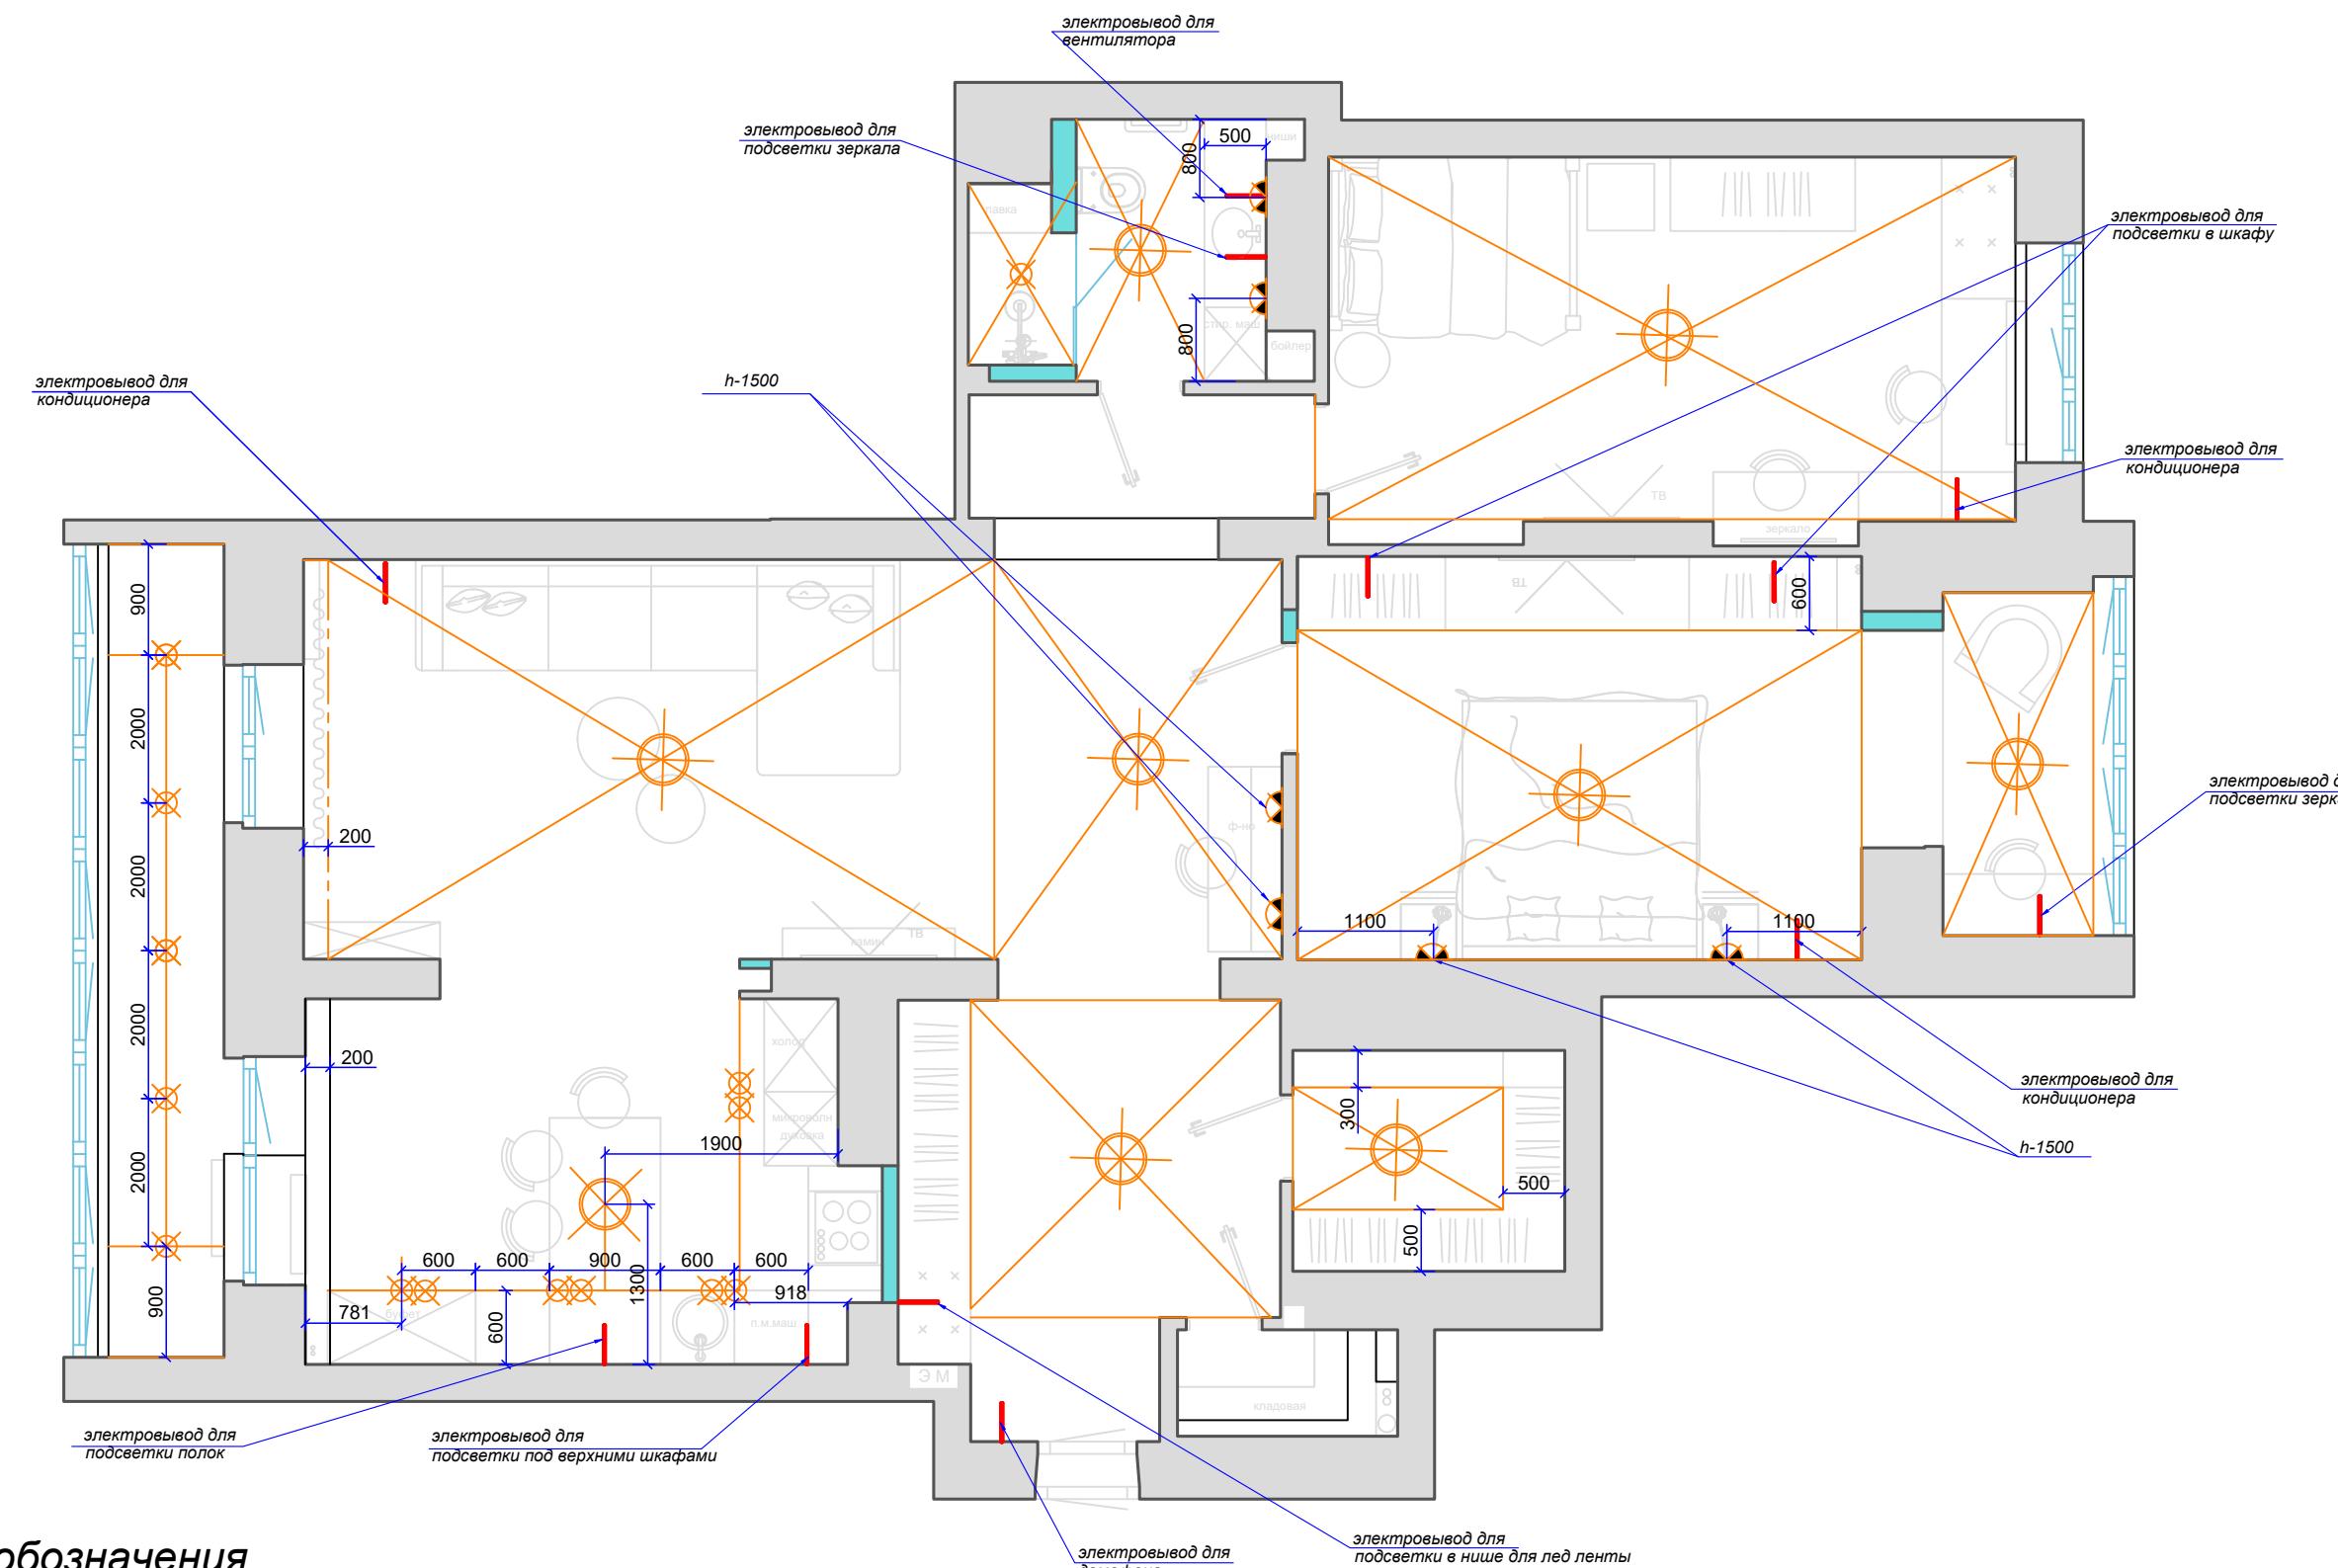

Условные обозначения



- накладной светильник или люстр



Соответствия между областями




- настенный светильник



- электровы

Условные обозначения

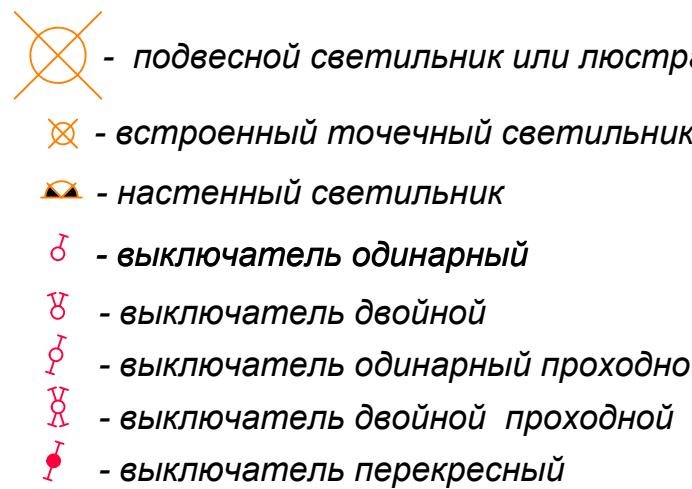


Согласовано

- n** - выключатель проходной
- 1,2 - нумерация выключателей
- 1,2 - нумерация источников освещения
- n`* - выключатель на источнике

Примечание

h до центра выключателей 900 мм от чистого пола, 150 мм от края проема и 200 от края дверного проема если не указано другое
h выключателей над кухней и в зоне шкафов согласовать с производителями мебели

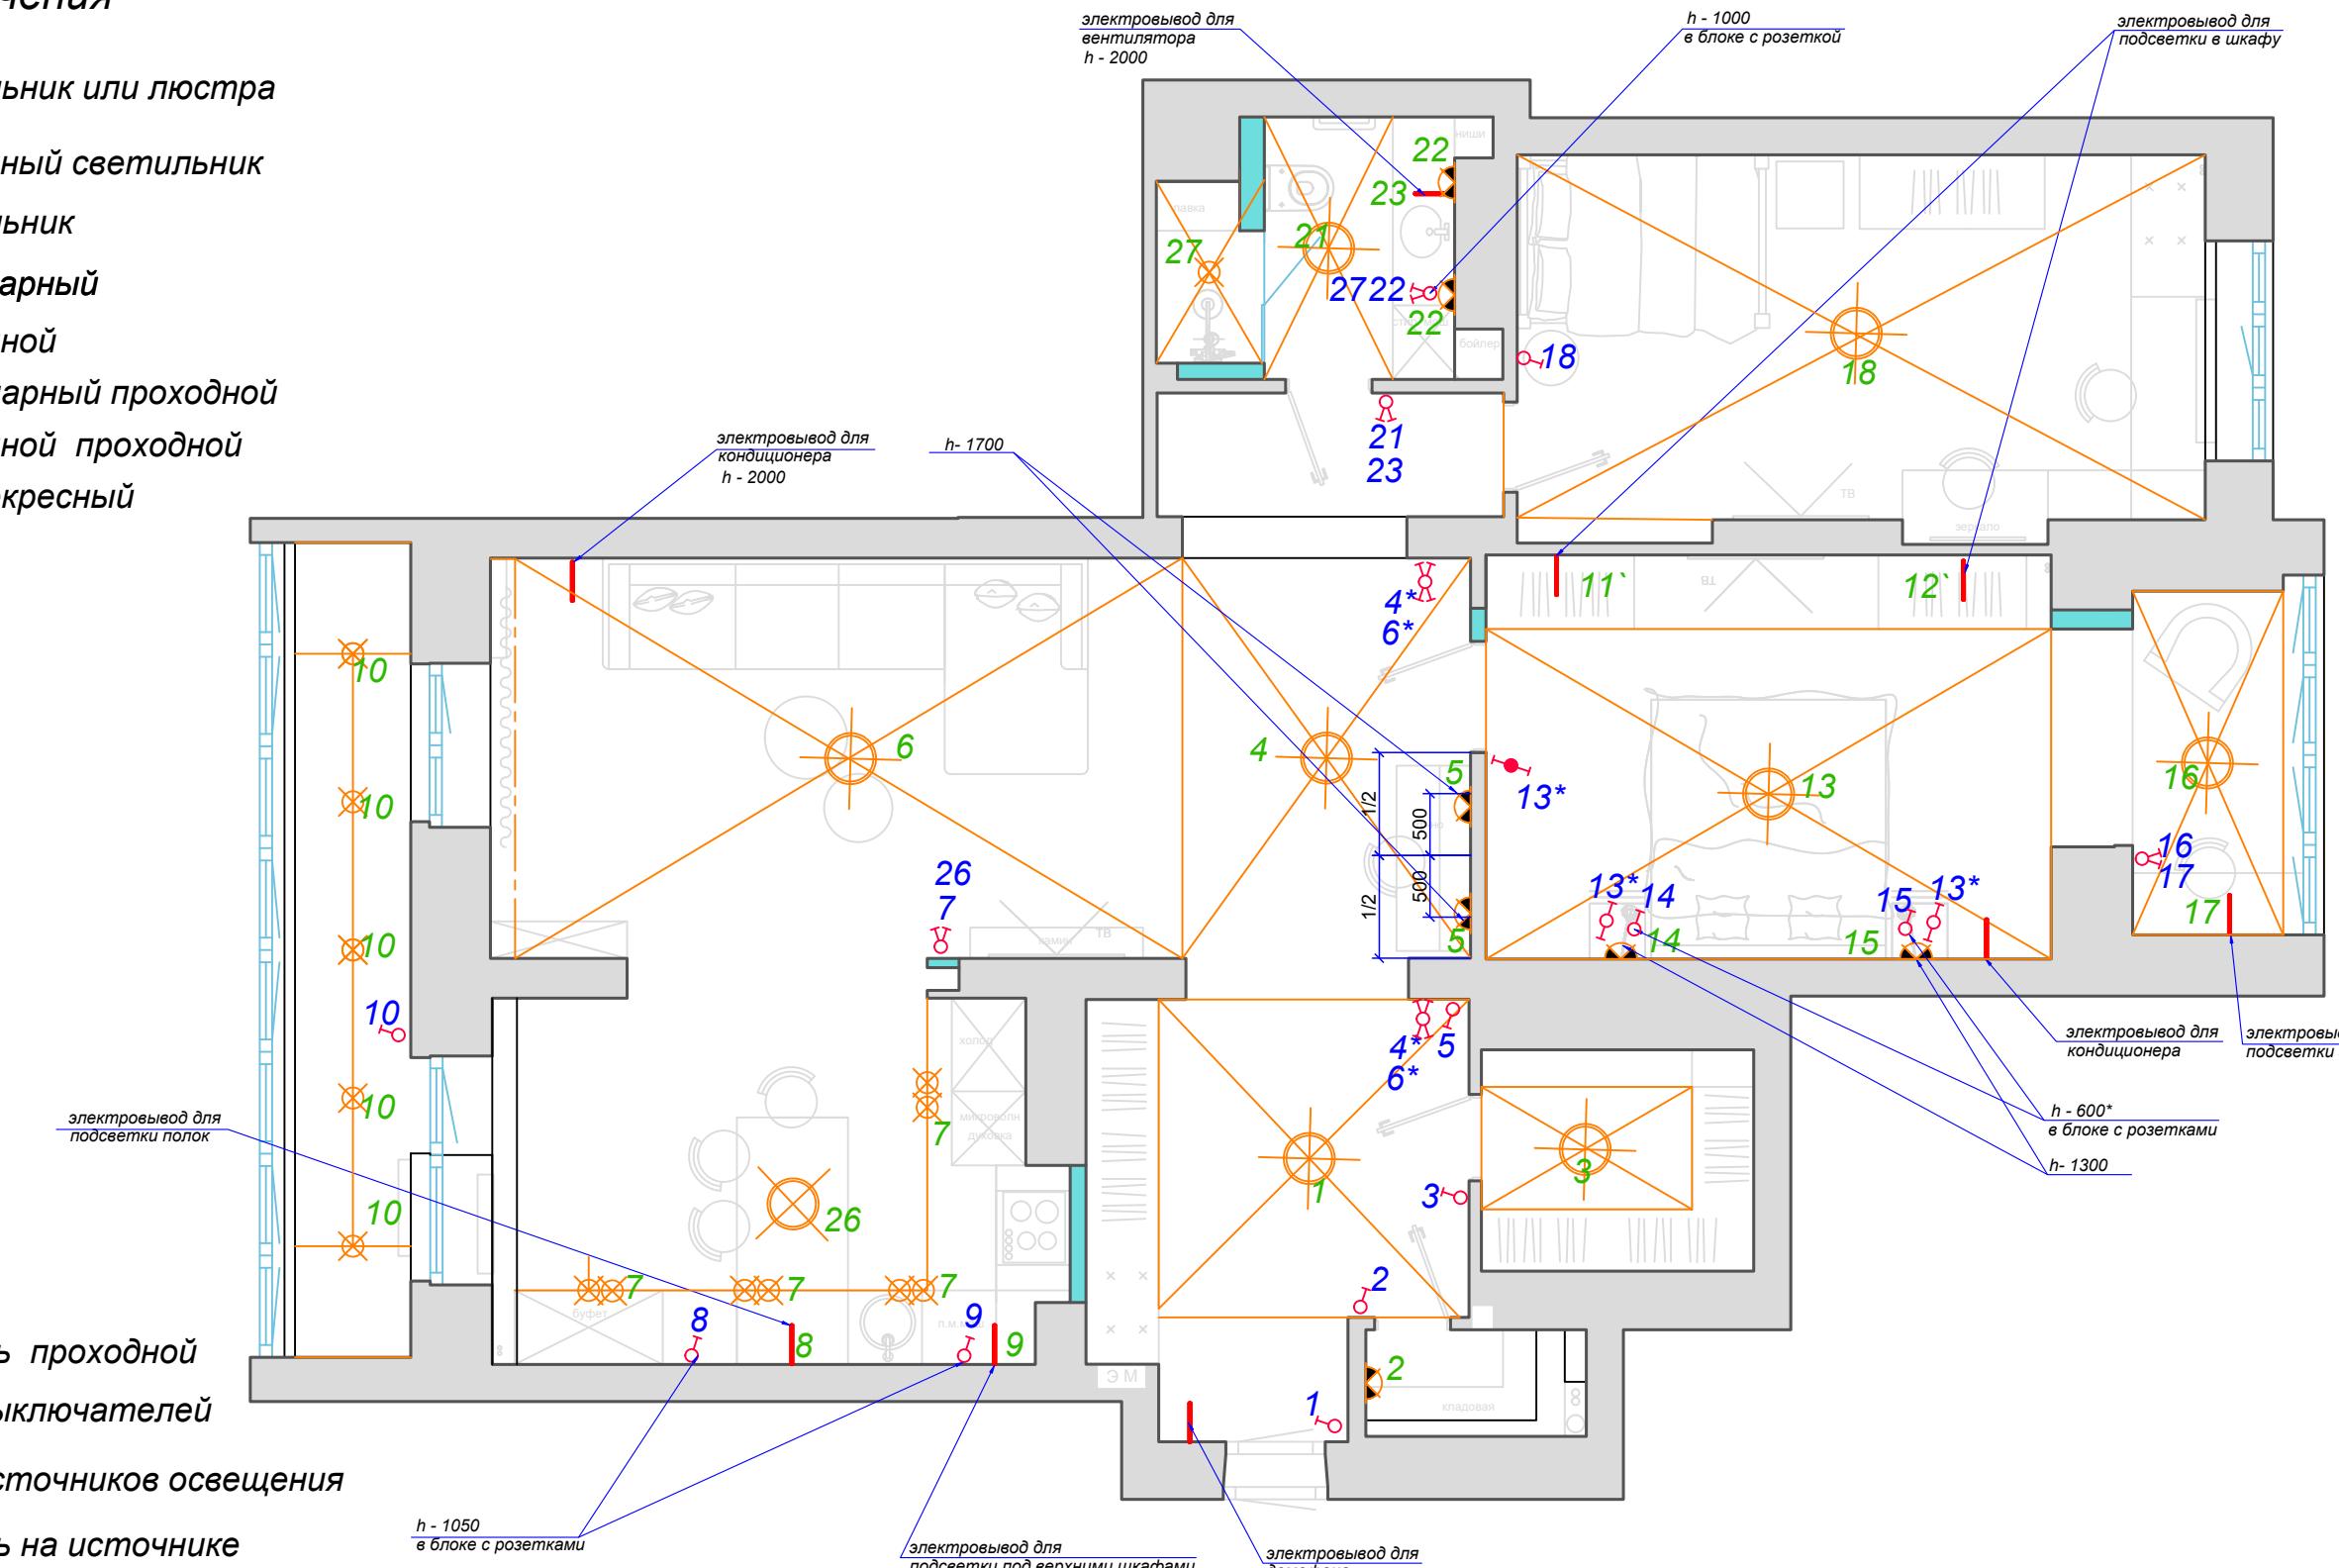


Согласовано		
Инв. № подл.	Подп. и дата	Взам.инв.№

Условные обозначения

- розетки электрические
 - розетки сантехнические
 - розетки телевизионные
 - розетки компьютерные
 - электровывод

Примечание

- *h* до центра розеток 300 мм от чистого пола, 150 мм от края проема или угла 200 от края дверного проема если не указано другое
 - *h* розеток под кухонное оборудование и в зоне шкафов согласовать с производителями мебели

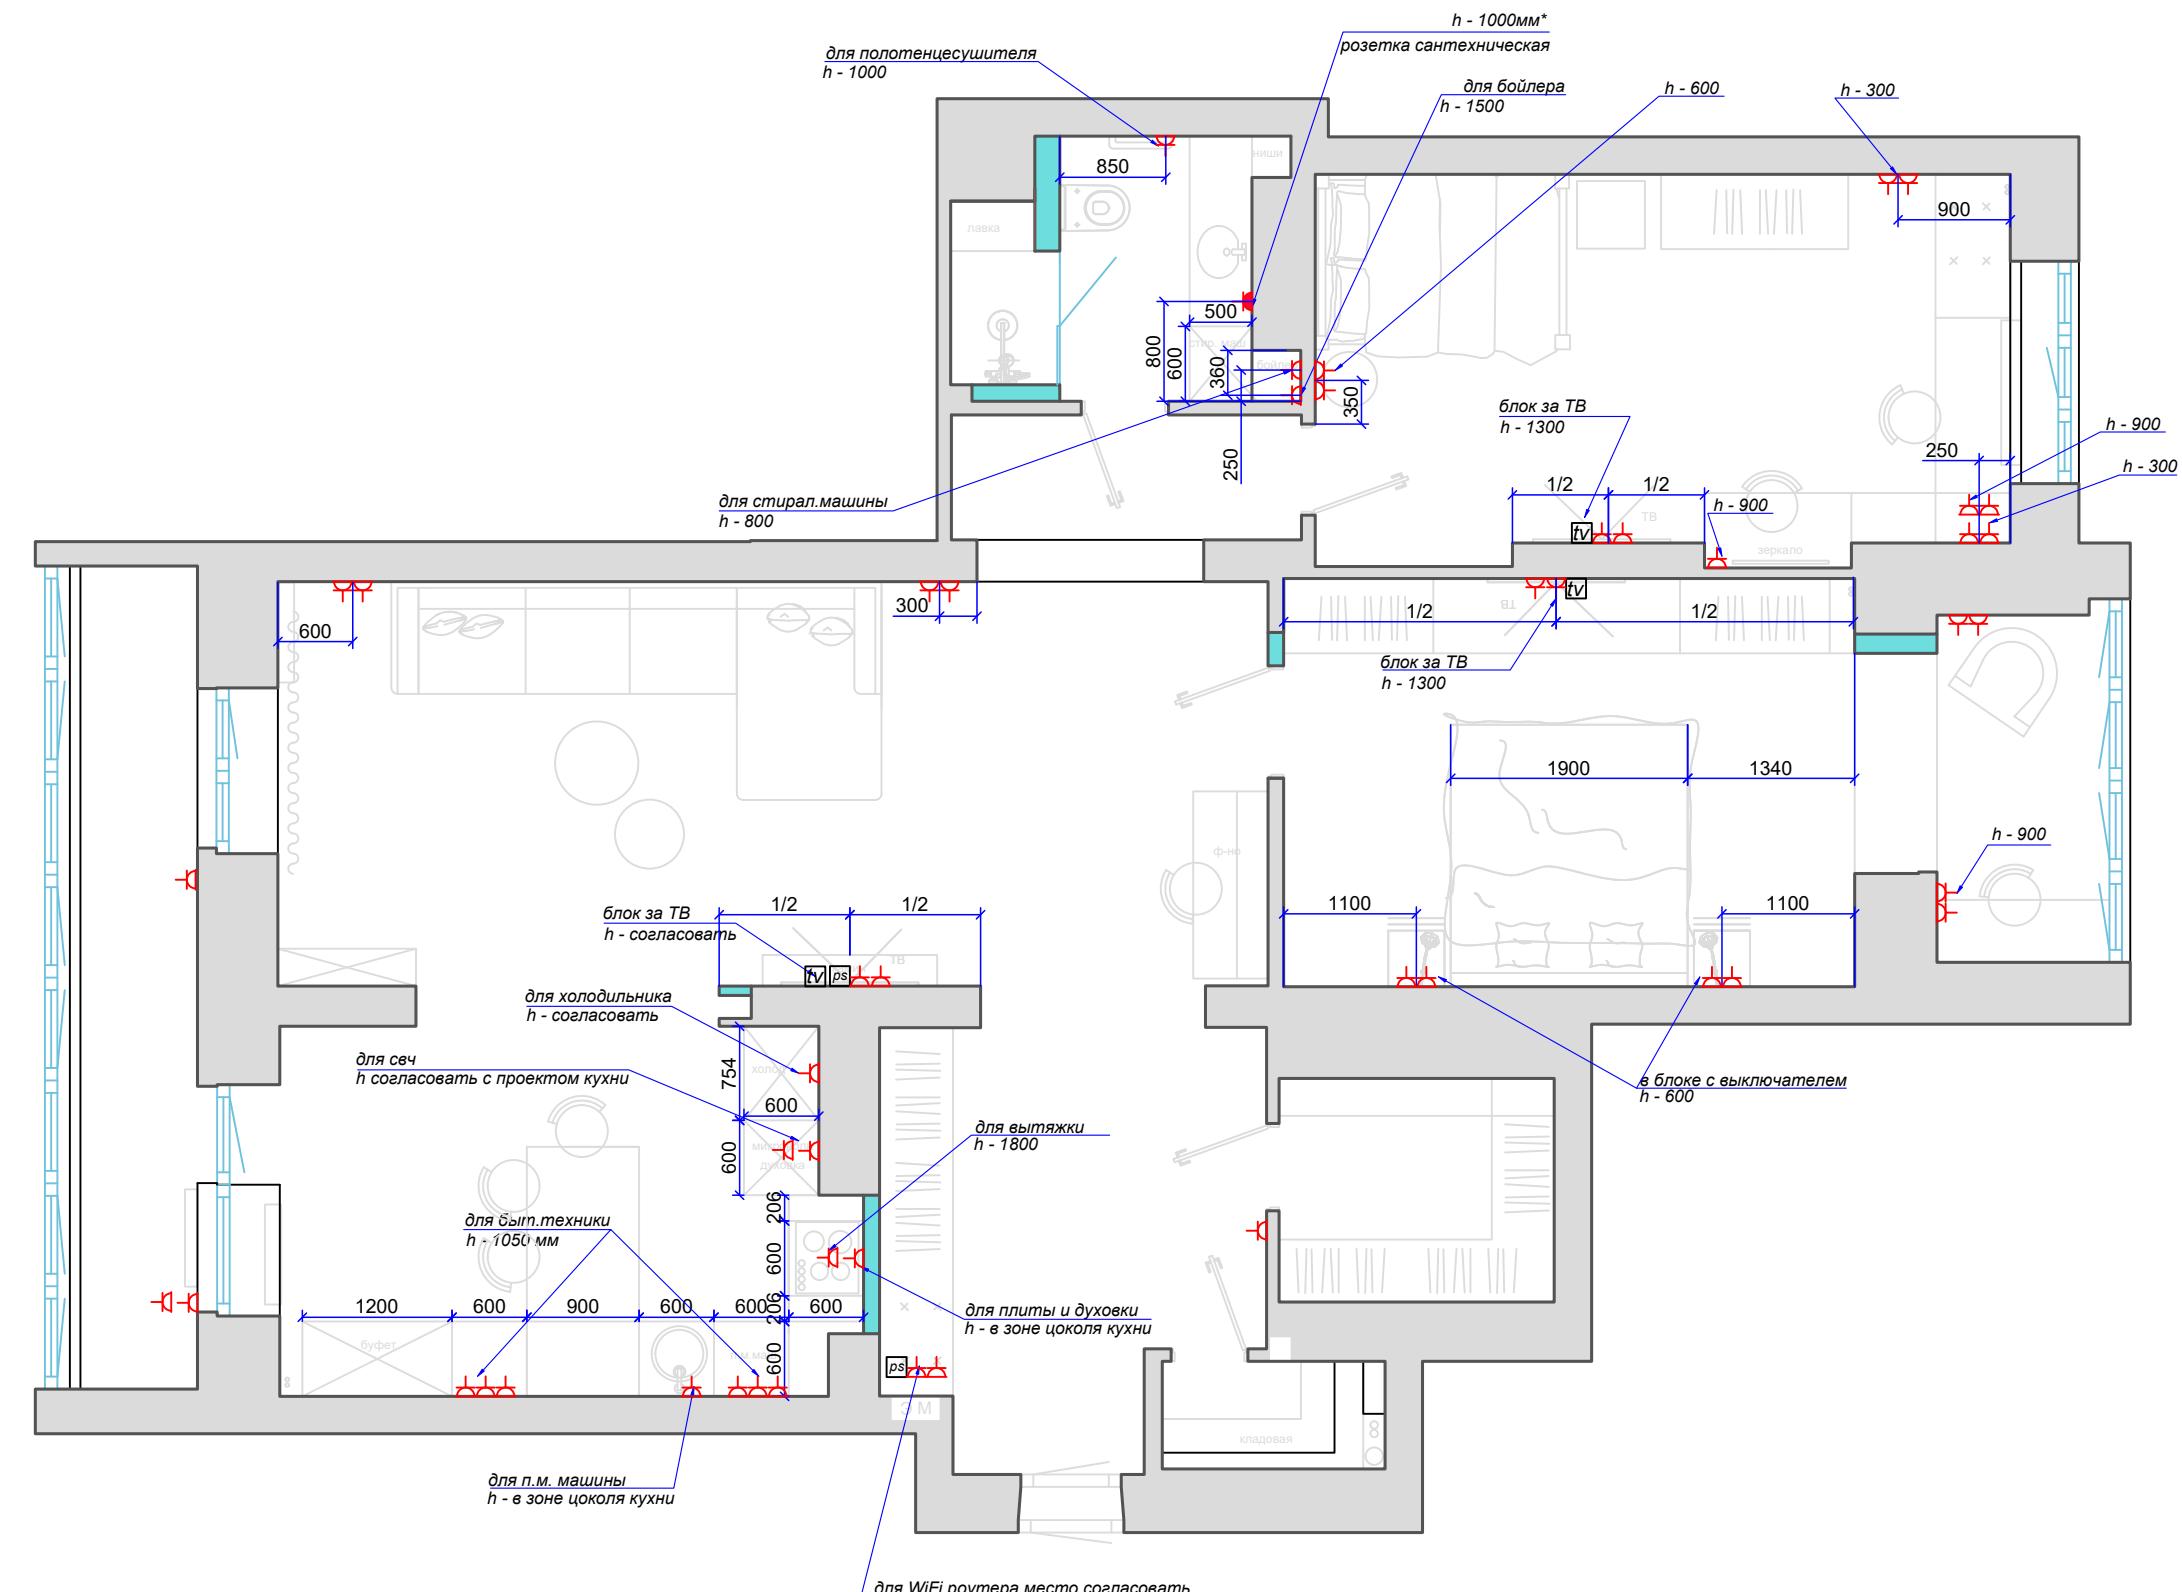


Согласовано					

Условные обозначения

цвет потолков - белый

- покраска Тип1
 - покраска Тип2
 - покраска Тип3
 - Обои Тип1
 - Обои Тип2
 - керамическая плитка настенная Тип1
 - керамическая плитка настенная Тип2

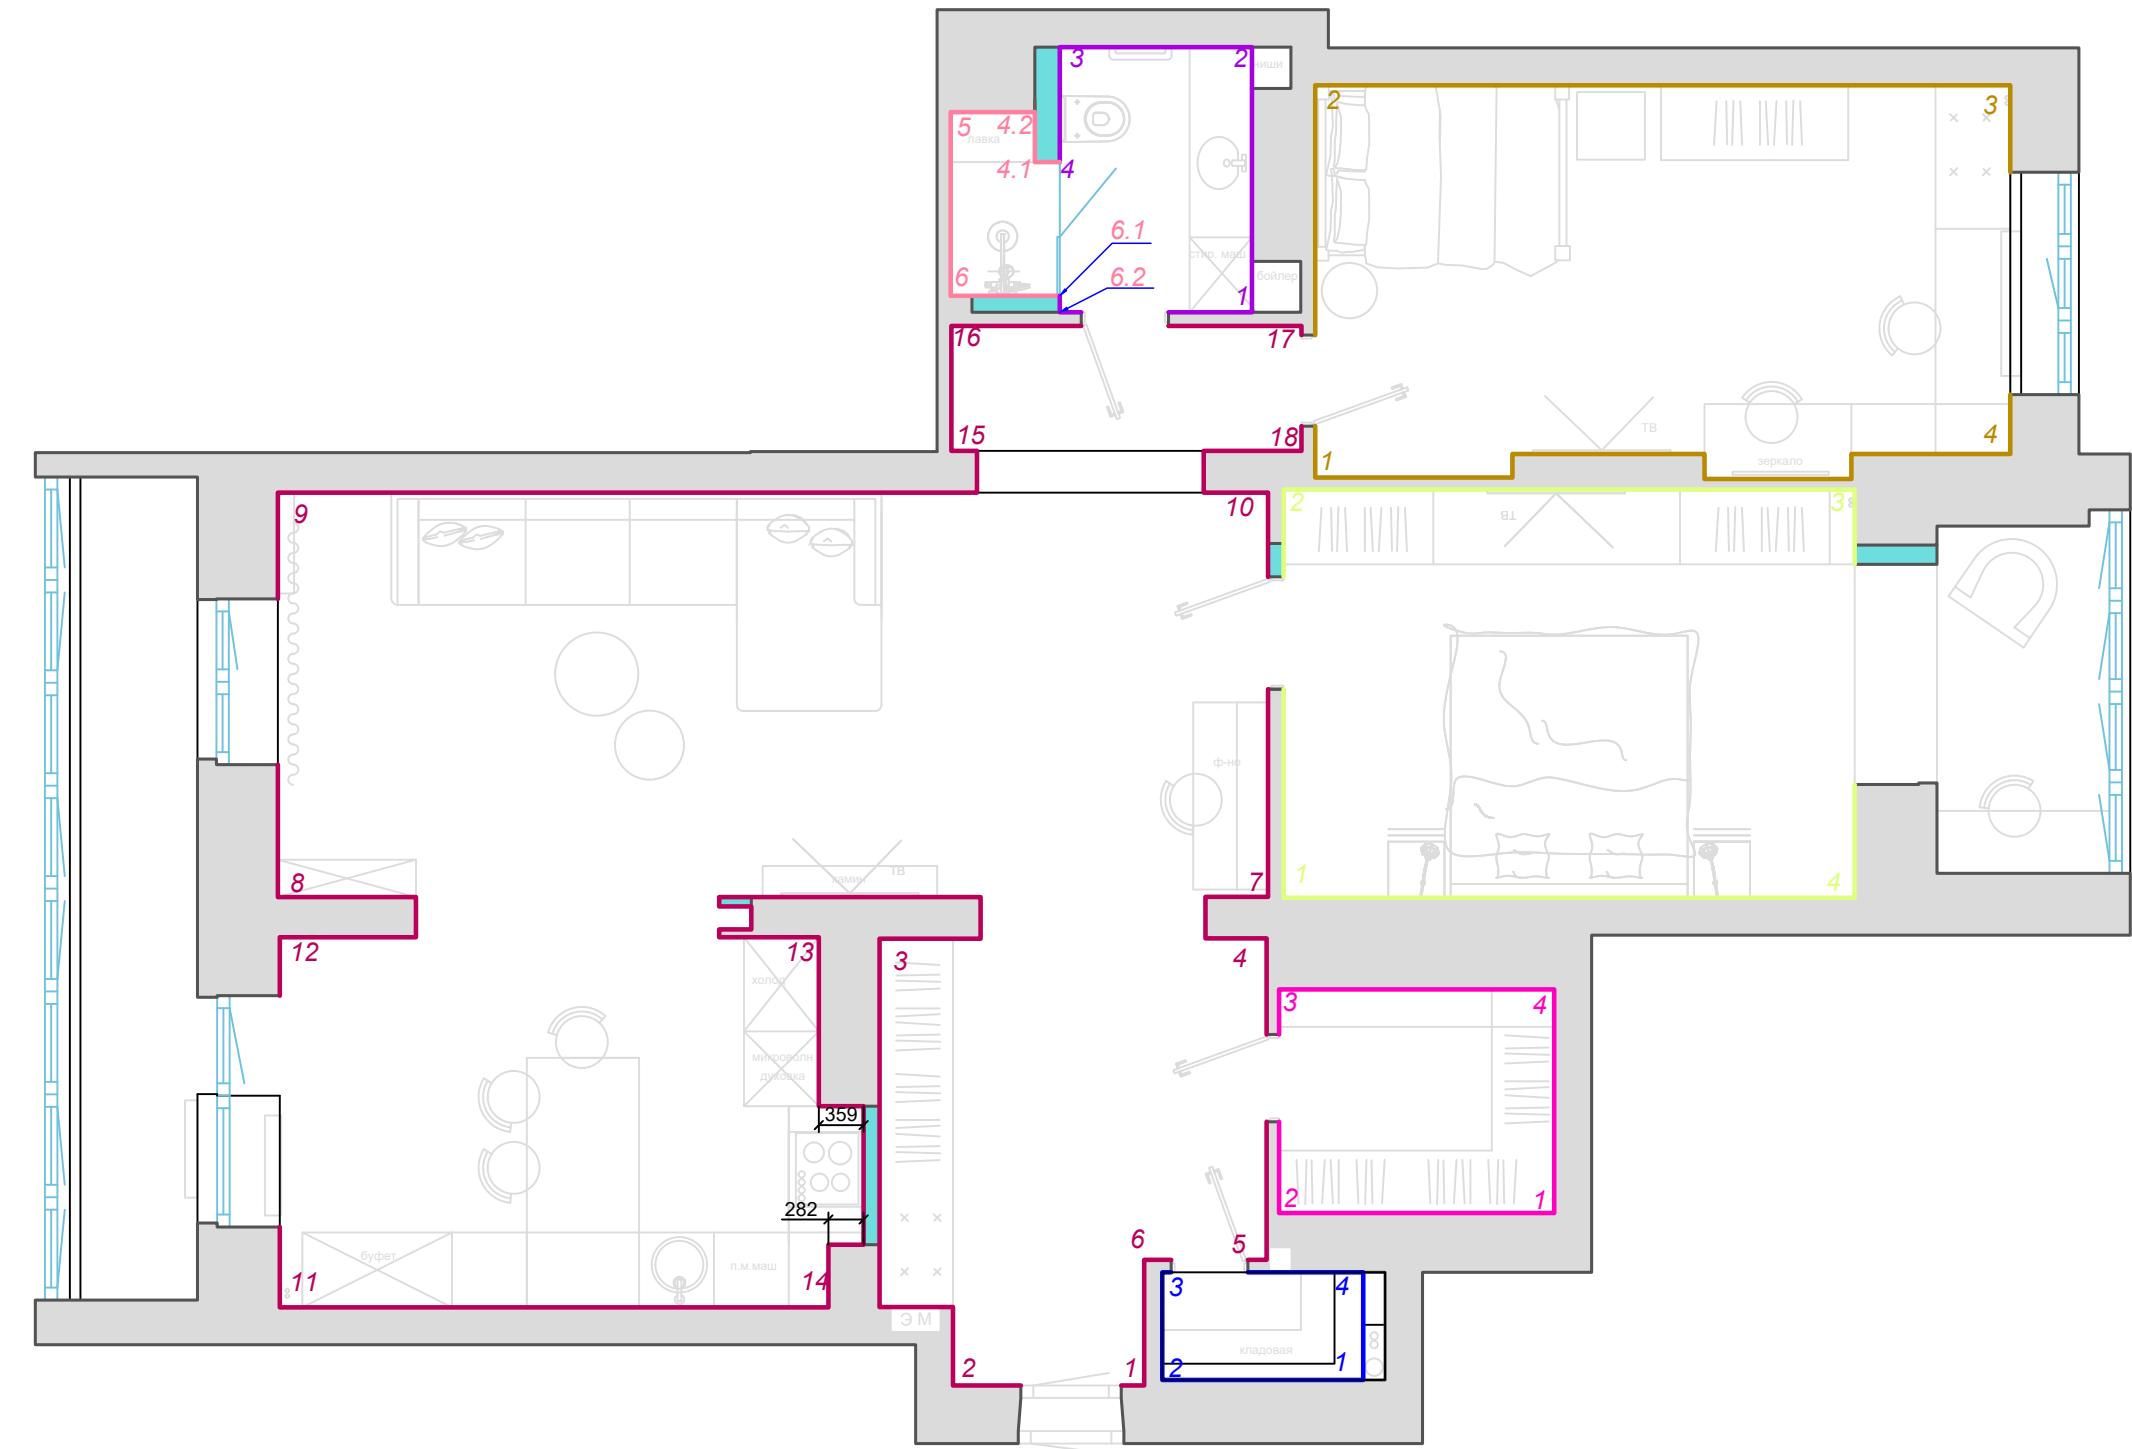

План-схема отделочных материалов

						План-схема отделочных материалов
Изм.	Кол.уч	Лист	№док	Подпись	Дата	
Квартира						СТАДИЯ
Р.П.						ЛИСТ
33						ЛИСТОВ
План						
clear line						
Н.контр						

Инв. № подл.	Побл. и дата	Взам. инв. №
--------------	--------------	--------------

Согласовано

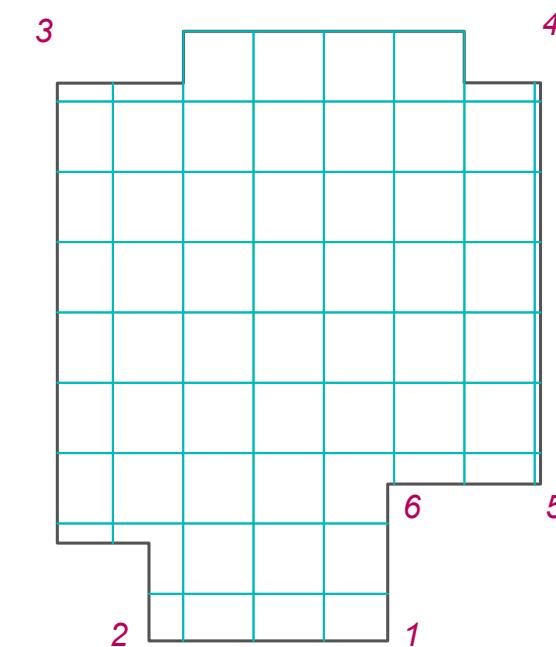
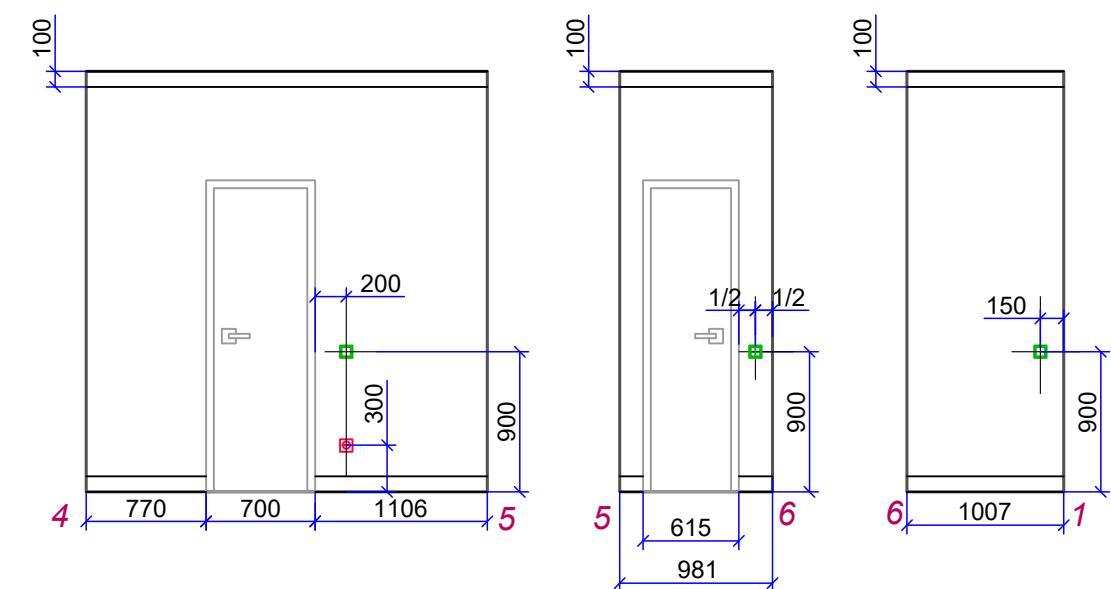
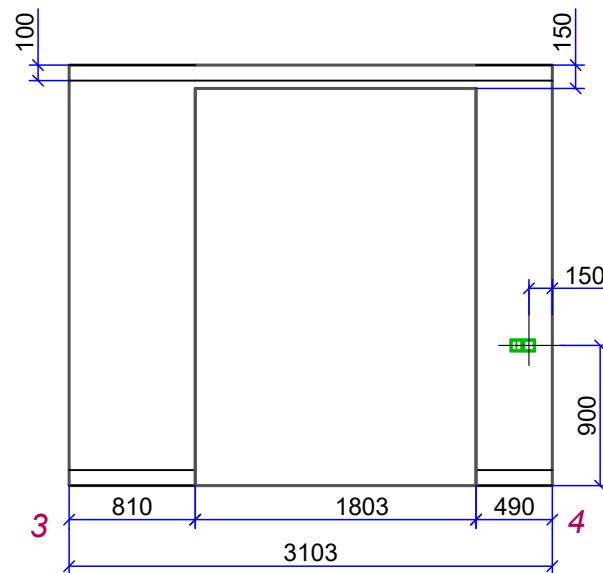
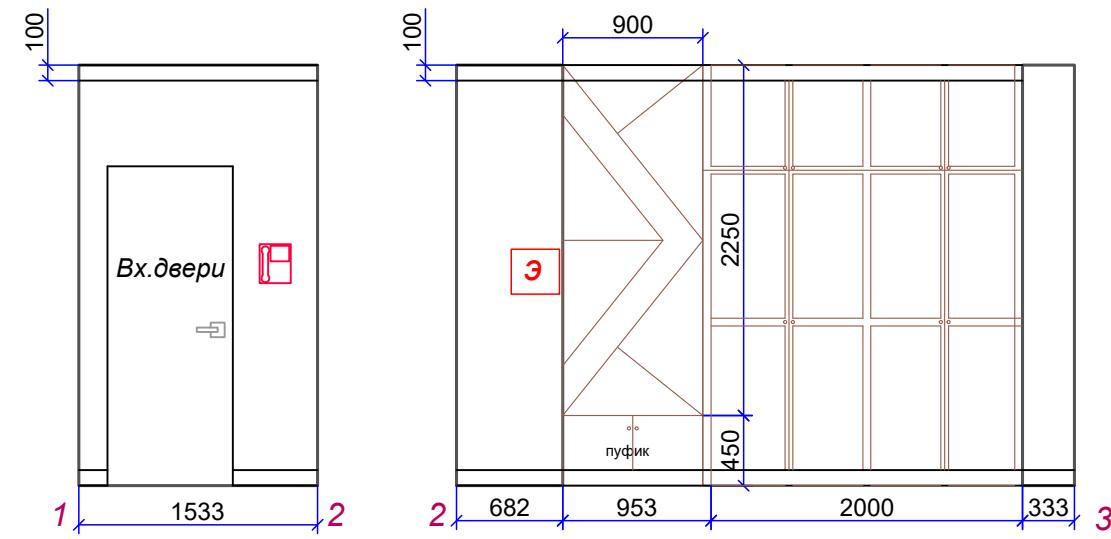


Таблица площадей стен		
Стена	Площадь, м ²	Примечание
1-2	2,49	
2-3	13,45	
3-4	3,85	
4-5	5,56	
5-6	1,42	
6-1	2,72	
Общая:	29,49	

Примечание

Нумерация стен на странице 13.

Условные обозначения

- домофон
- розетка электрическая
- выключатель 1-о клавишный
- выключатель 2-х клавишный

Условные обозначения

- | | |
|--|-----------------------------------|
| | плитка напольная тип 2
450x450 |
|--|-----------------------------------|






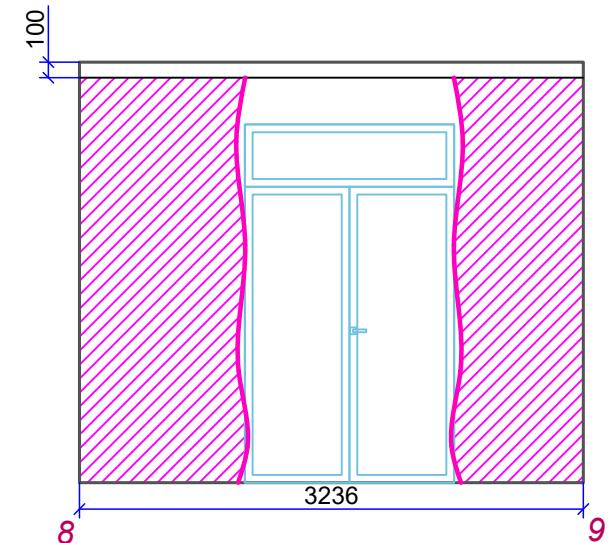


Таблица площадей стен		
Стена	Площадь, м2	Примечание
7-8	10,64	
8-9	5,43	
9-10	16,80	
10-7	6,95	
15-16	2,70	
16-17	6,18	
17-18	1,30	
18-15	3,22	
Общая:	53,20	

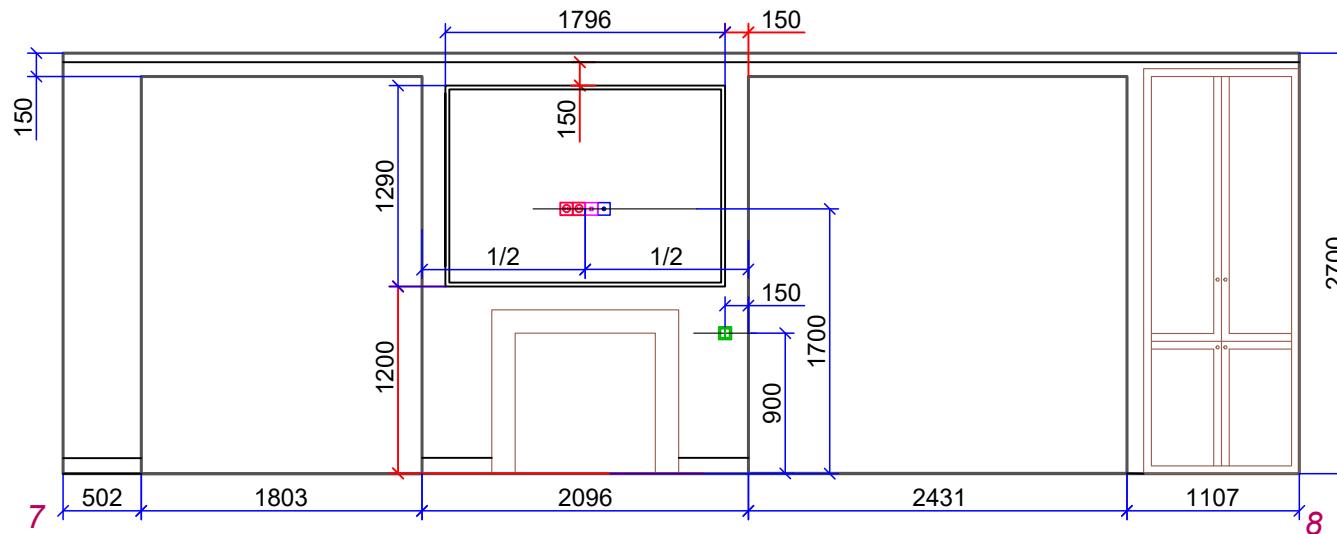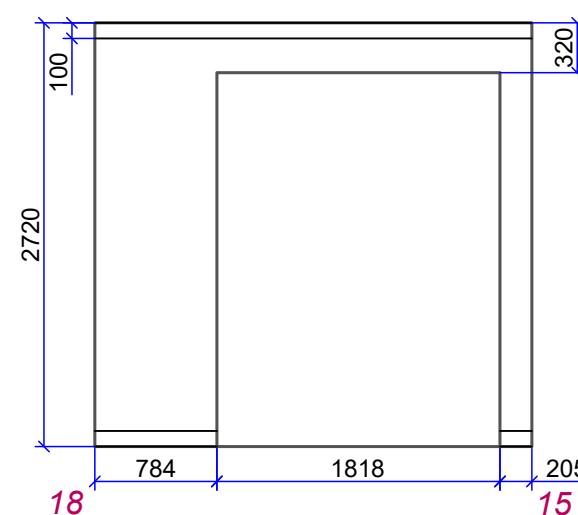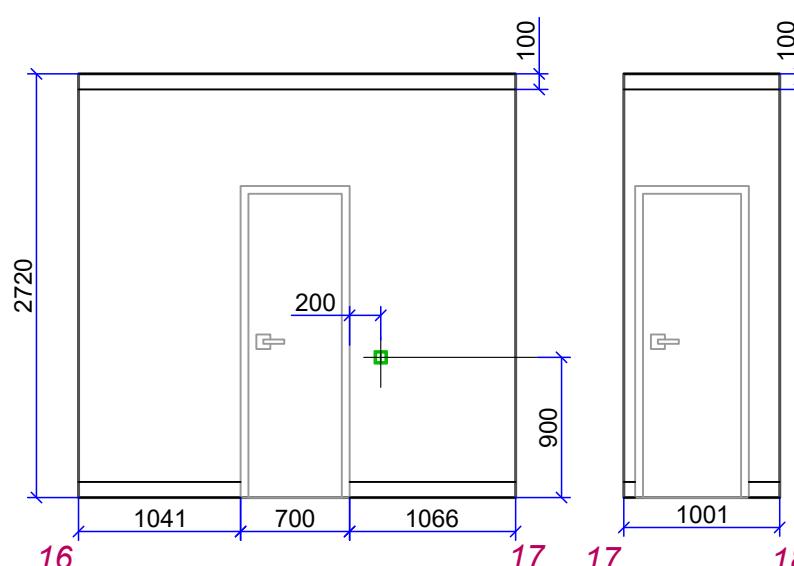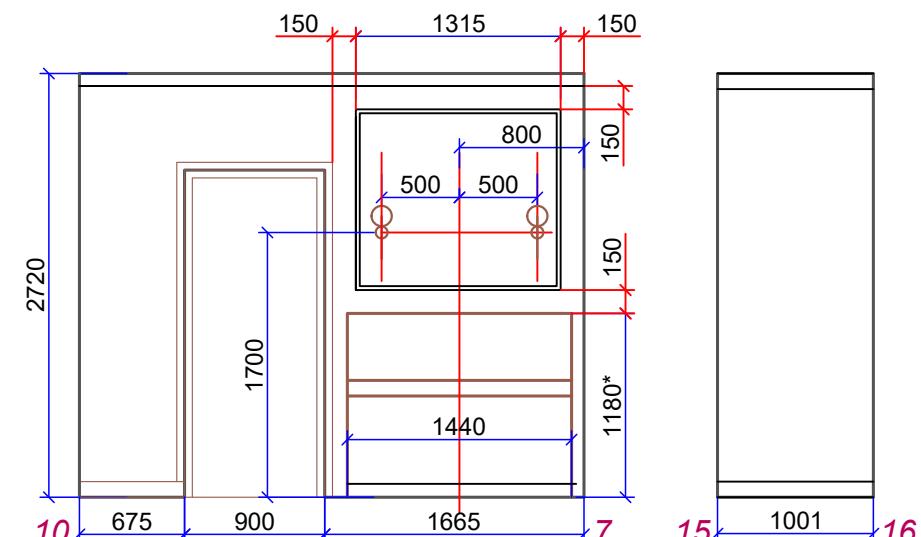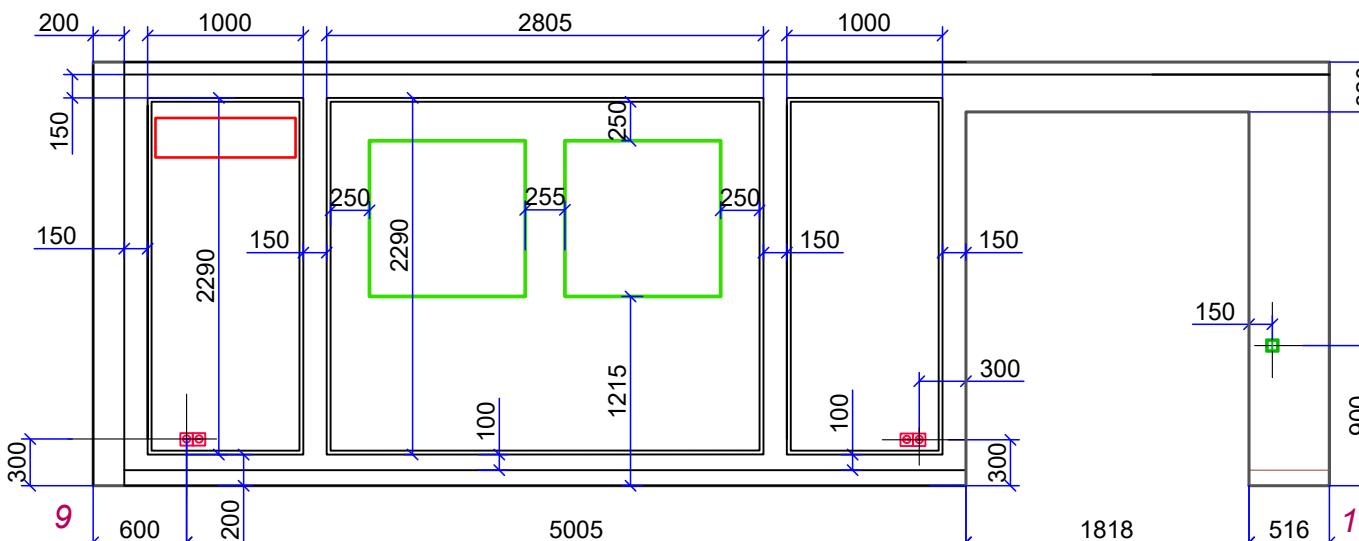

Условные обозначения


- розетка электрическая
- розетка tv
- розетка интернет
- розетка usb
- выключатель 1-о клавишный
- выключатель 2-х клавишный

Примечание

Нумерация стен на странице 13.

Раскладка стен. Гостиная

лист
35

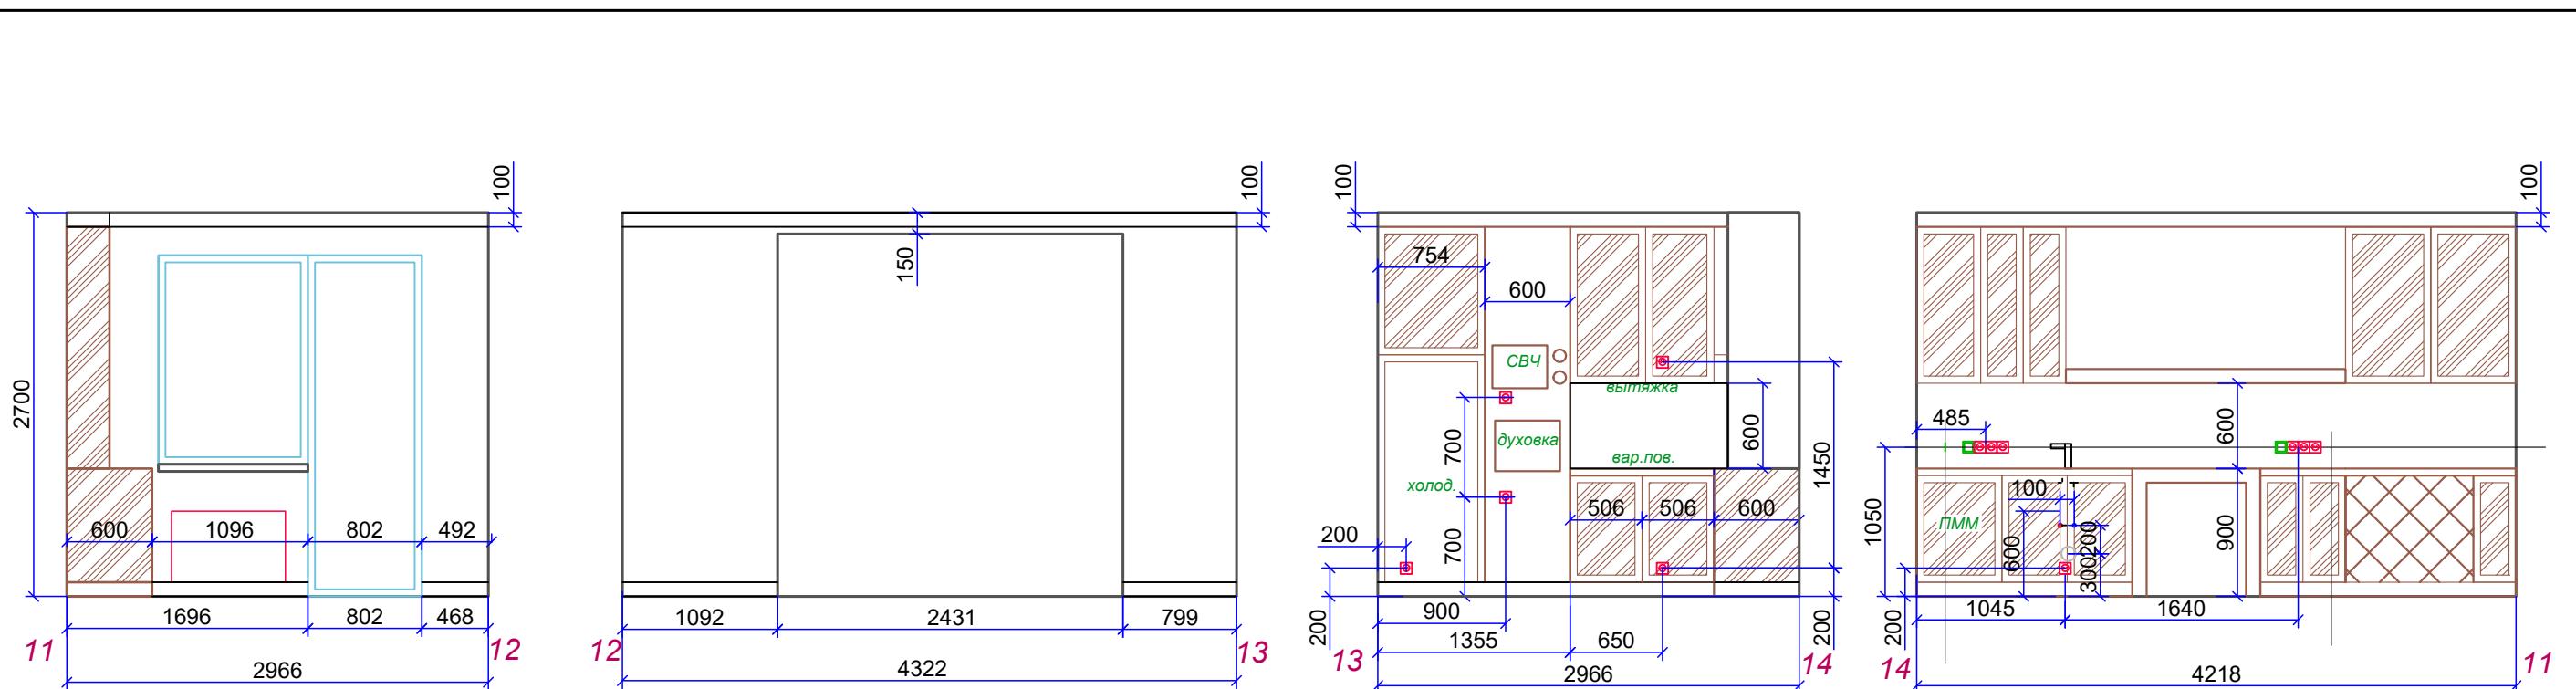

Сообщество

Инв. № по дате	Подп. и дата	Взам. инв.№

Таблица площадей стел

Стена	Площадь, м ²	Примечание
11-12	4,54	
12-13	5,47	
13-14	11,09	
14-11	12,20	
Общая:	33,30	

Примечание

Нумерация стен на странице 13.

Условные обозначения

	плитка настенная тип 1 1200x600
	плитка напольная тип 2 450x450

Условные обозначения

- розетка электрическая
 - выключатель 1-о клавишный
 - вывод горячей воды
 - вывод холодной воды
 - слив воды

Инв. № подл.	Площ. и дата	Взам. инв. №

Согласовано

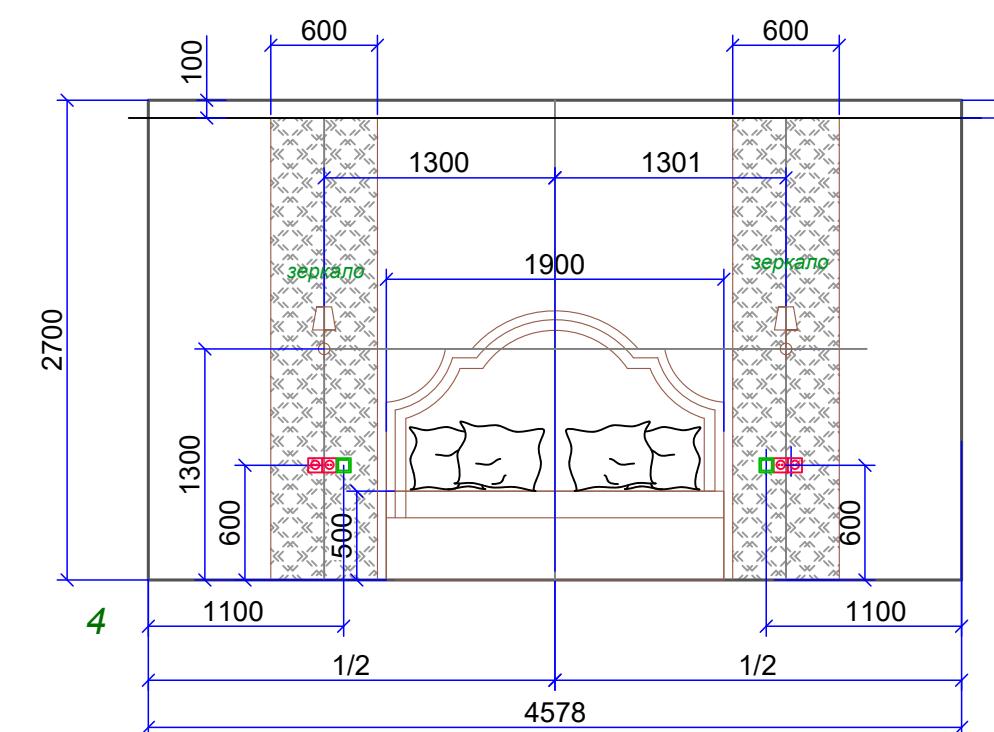
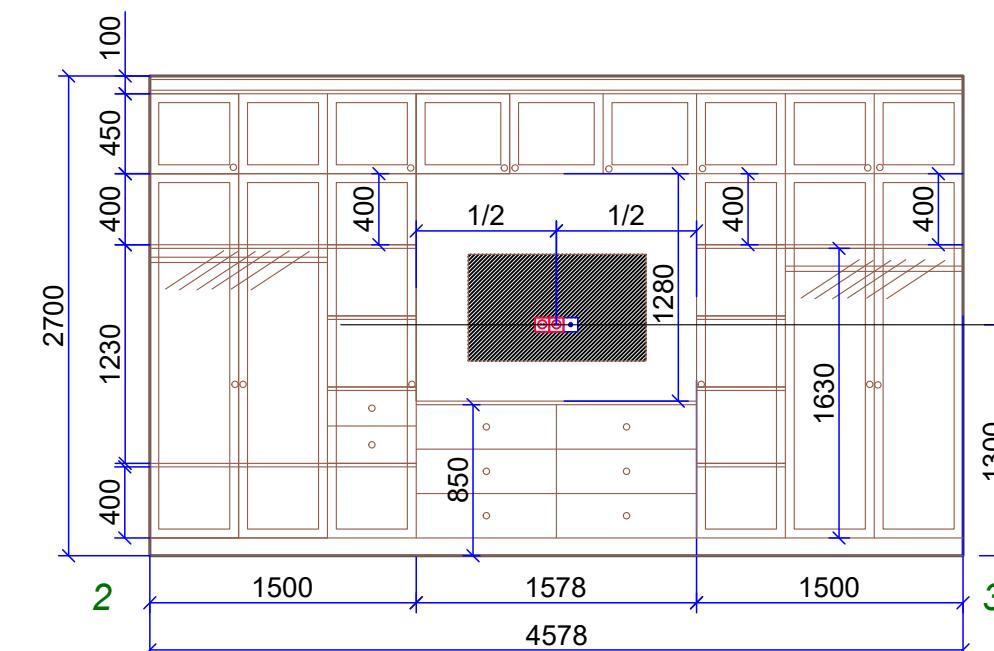
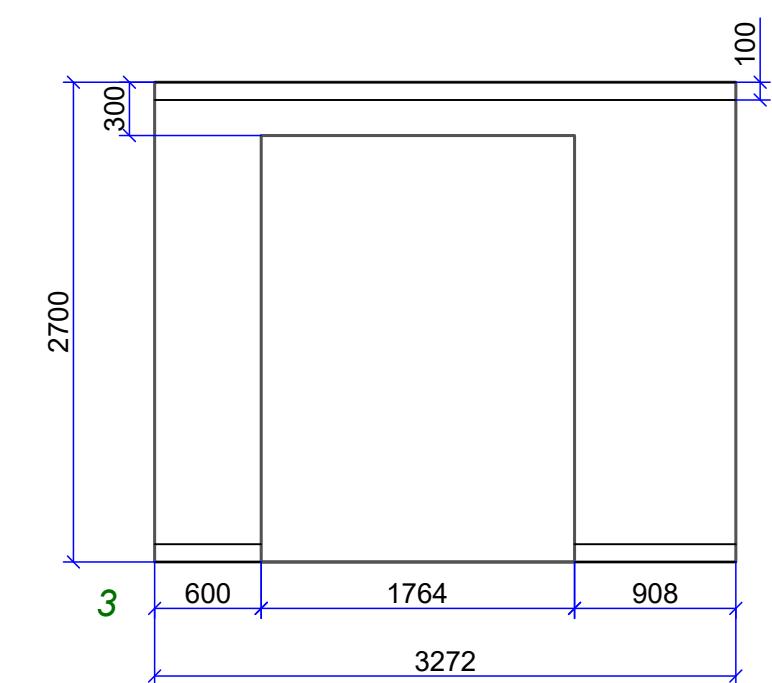
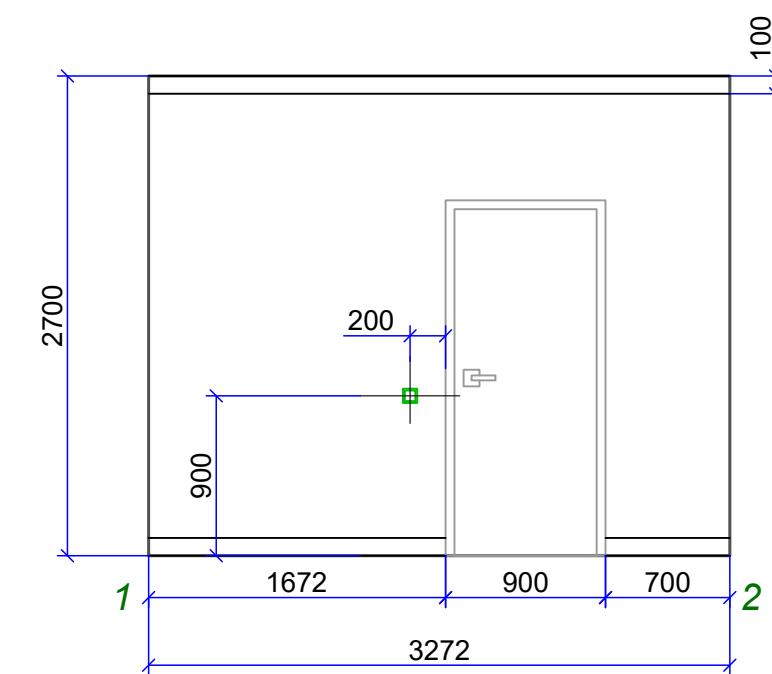


Таблица площадей стен		
Стена	Площадь, м ²	Примечание
1-2	7,03	
2-3	12,36	
3-4	4,60	
4-1	12,36	
Общая:	36,35	

Примечание

Нумерация стен на странице 13.

Условные обозначения

- розетка электрическая
- розетка tv
- выключатель 1-о клавишный
- выключатель 2-х клавишный

Раскладка стен. Спальня

Инв. № подл.	Площ. и дата	Взам. инв. №

Согласовано

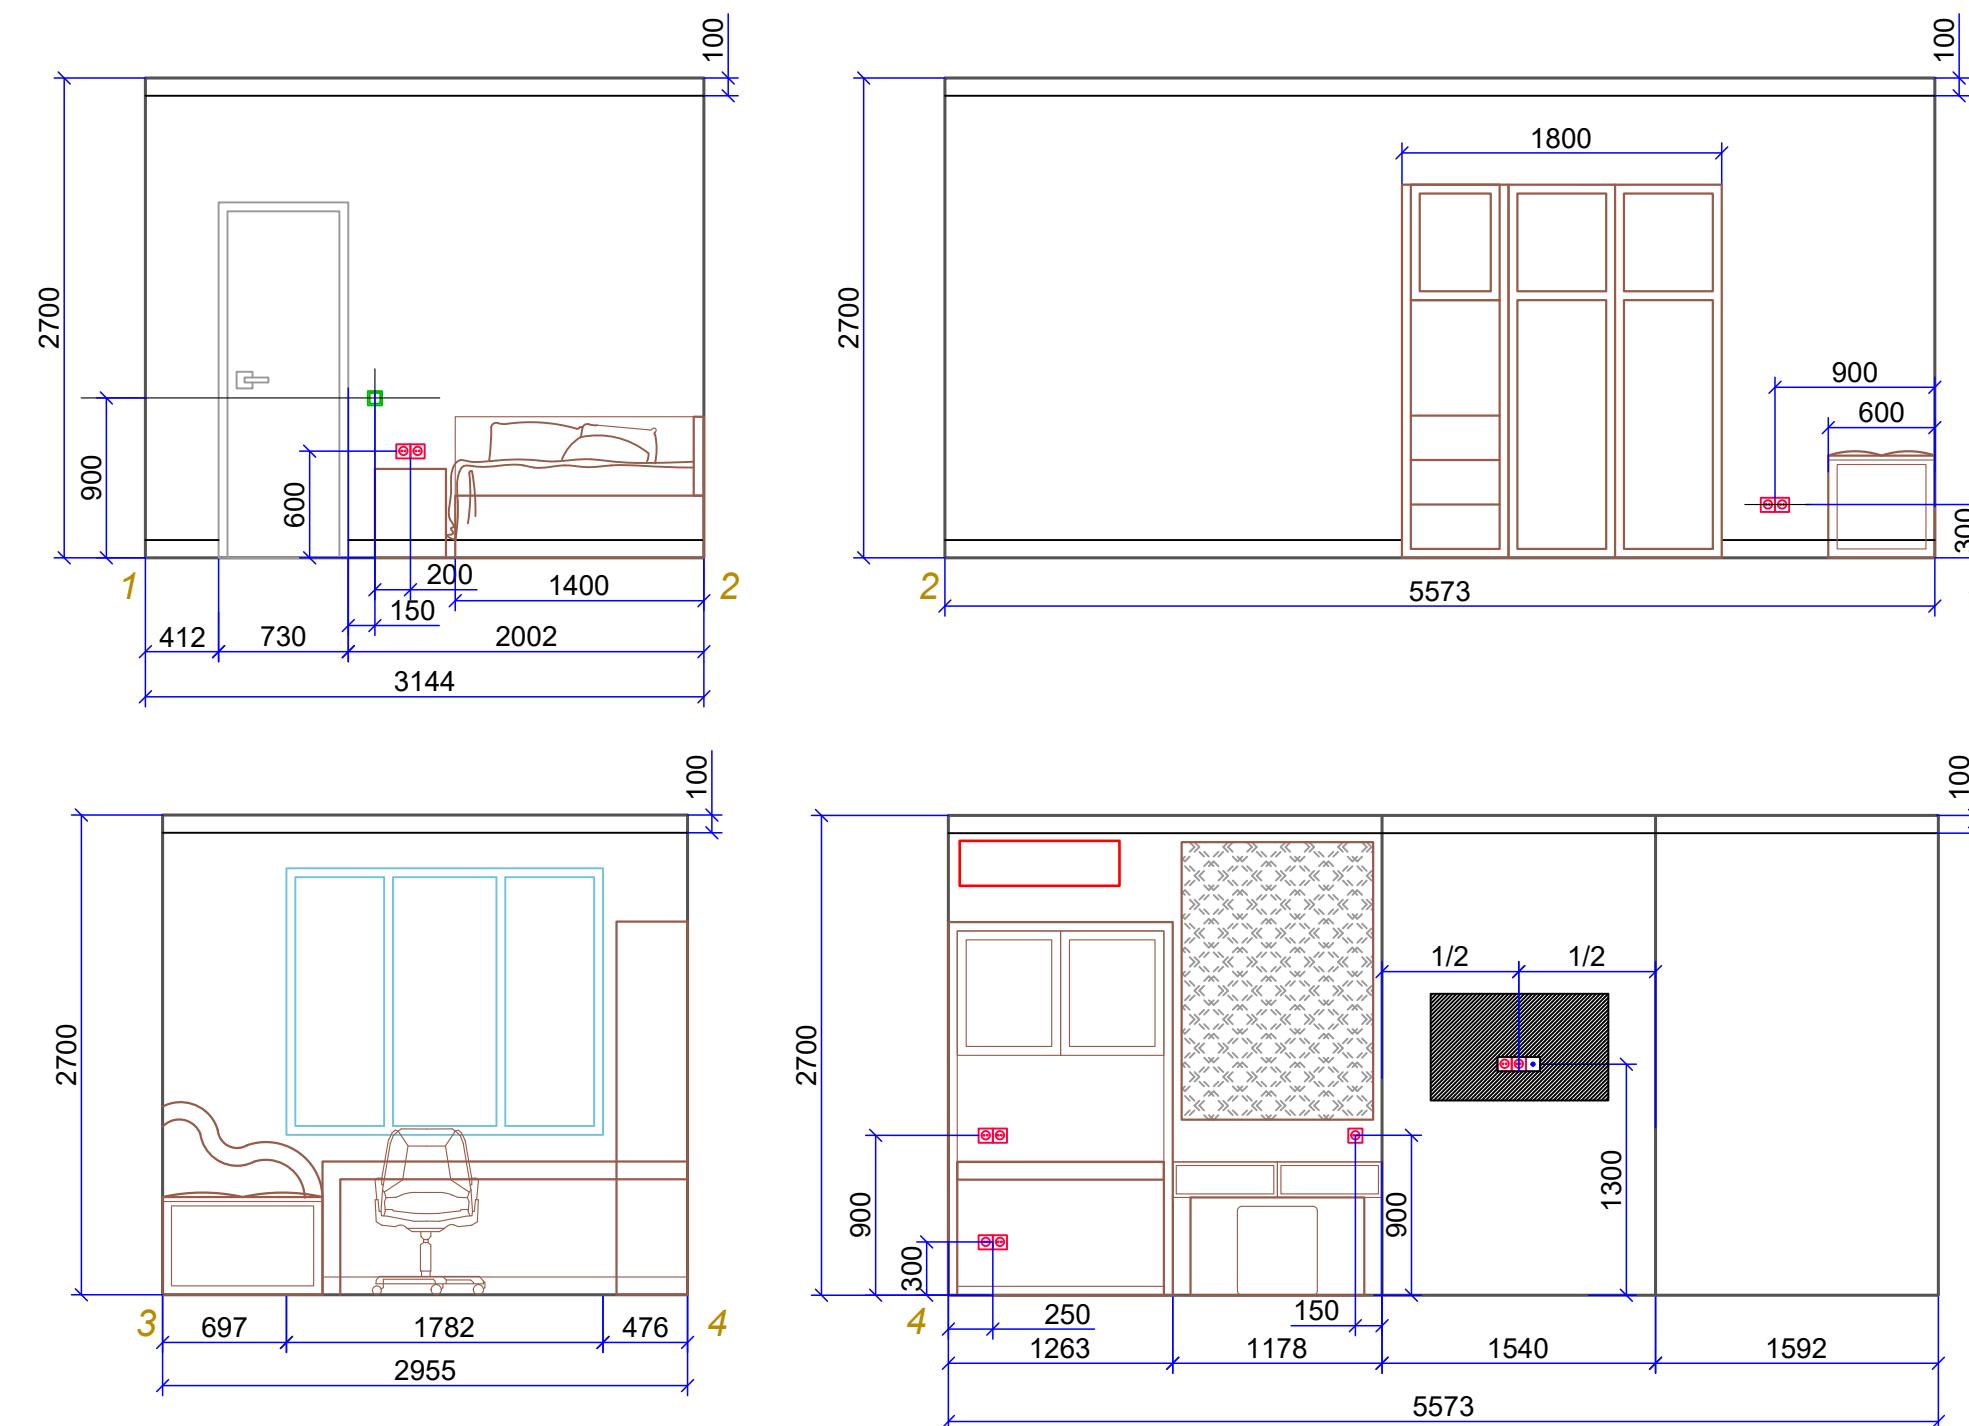


Таблица площадей стен

Стена	Площадь, м ²	Примечание
1-2	7,03	
2-3	15,04	
3-4	5,30	
4-1	16,63	
Общая:	44,00	

Примечание

Нумерация стен на странице 13.

Условные обозначения

- (◎) - розетка электрическая
- (□) - розетка интернет
- (■) - выключатель 1-о клавишный

Раскладка стен. Детская

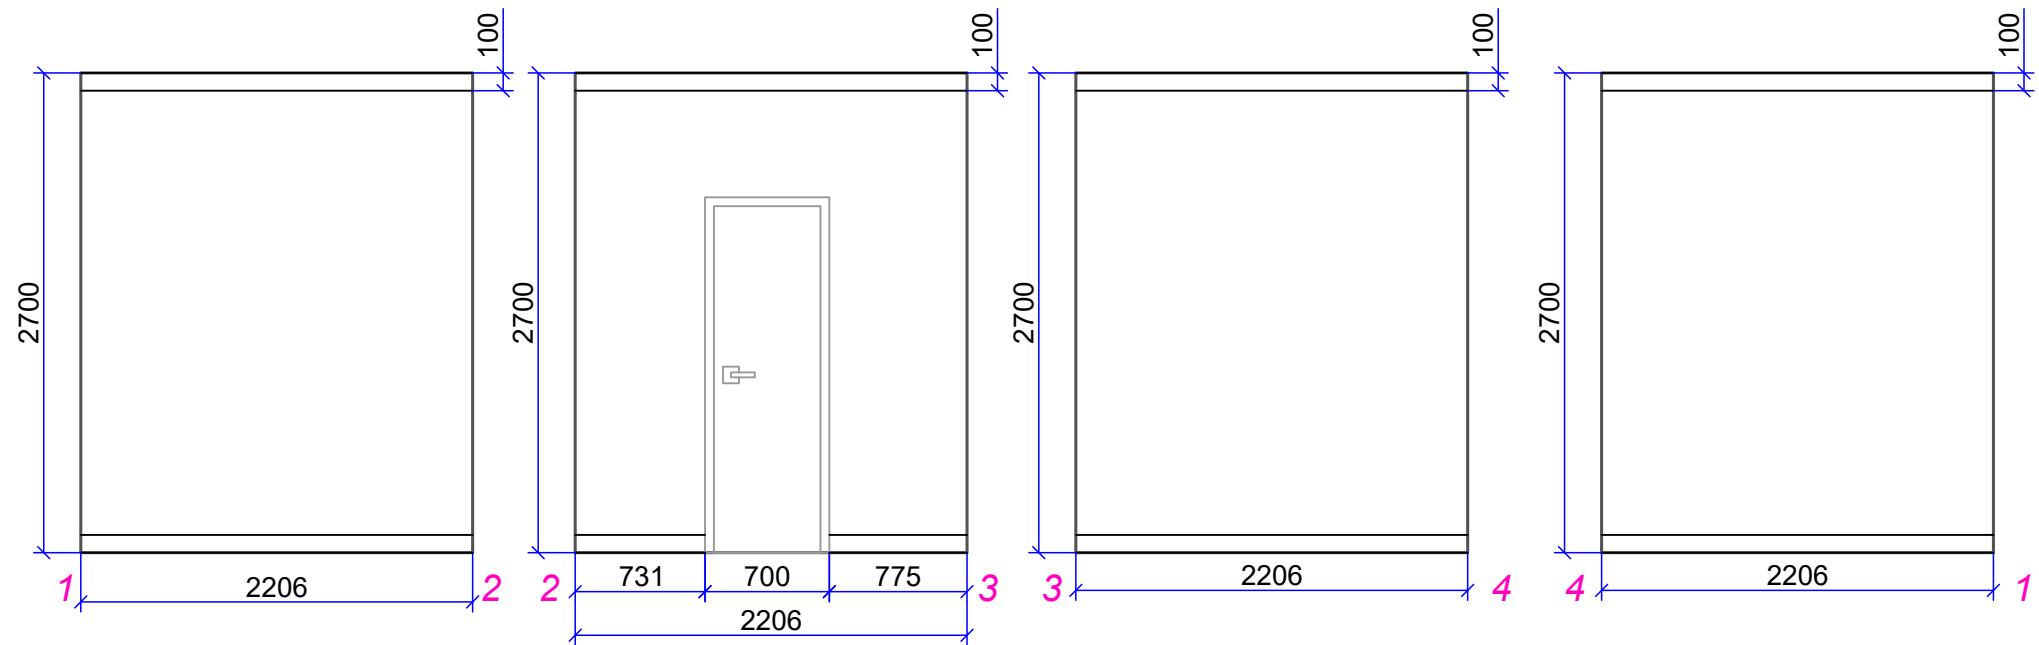


Таблица площадей стен

Стена	Площадь, м ²	Примечание
1-2	5,96	
2-3	4,56	
3-4	5,96	
4-1	5,96	
Общая:	22,44	

Условные обозначения



плитка напольная тип 2
450x450

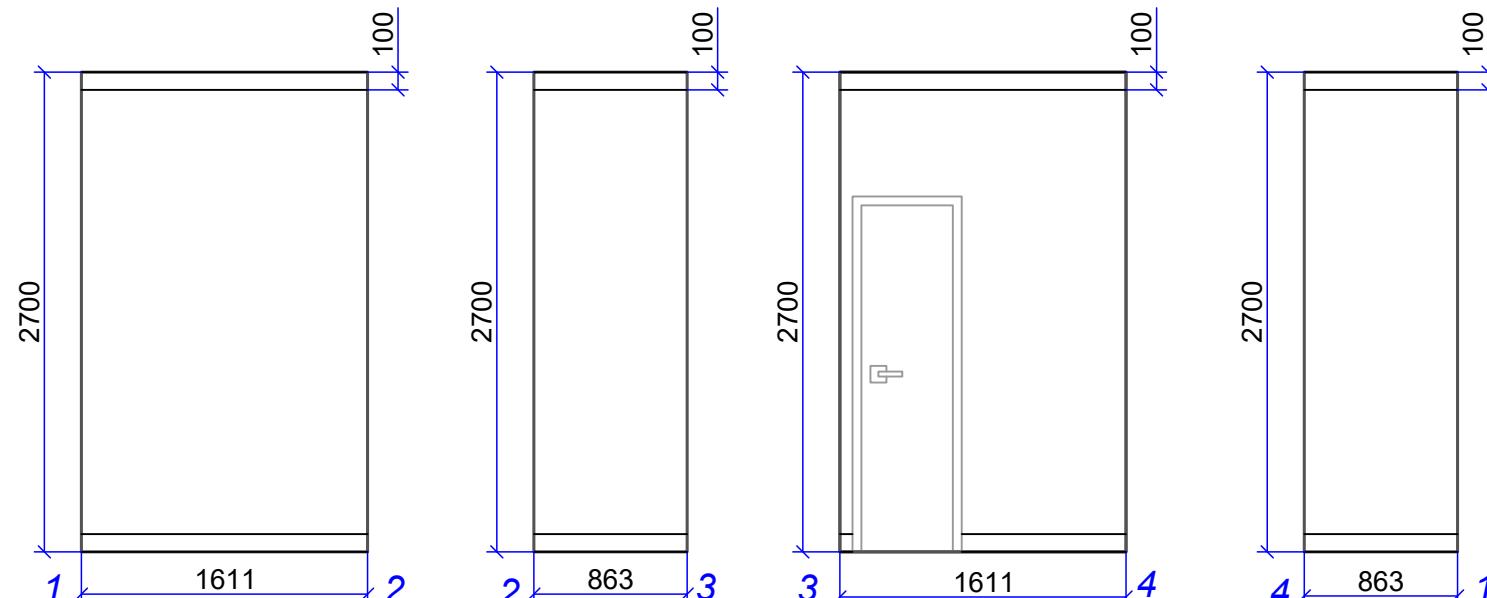


Таблица площадей стен

Стена	Площадь, м ²	Примечание
1-2	4,35	
2-3	2,33	
3-4	2,95	
4-1	2,33	
Общая:	11,96	












Примечание
Нумерация стен на странице 13.

Раскладка стен. Раскладка пола. Гардеробная-Кладовка


Инв. № подп.	Площд. и дата	Взам.инв.№

Таблица площадей стен		
Стена	Площадь, м ²	Примечание
2-1	7,83	
3-2	5,00	
4-3	2,49	
4.1-4	0,54	
4.2-4.1	1,08	
5-4.2	1,82	
6-5	3,97	
1-6.2	3,82	
6.2-6.1	0,46	
6.1-6	2,36	
Общая:	29,37	

Примечание
Нумерация стен на странице 13.

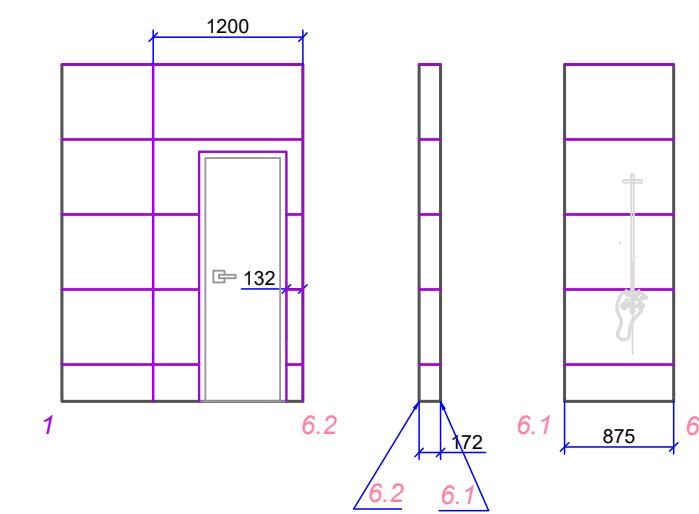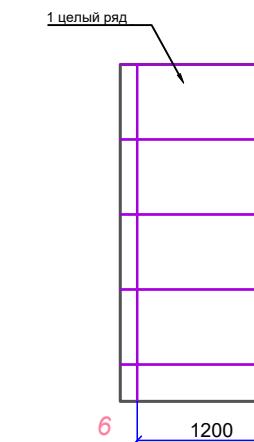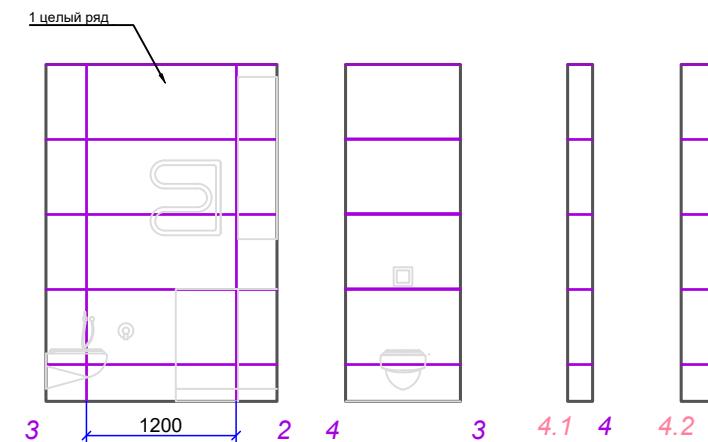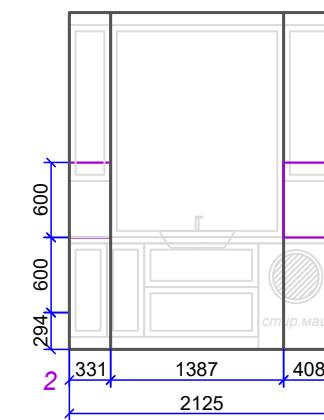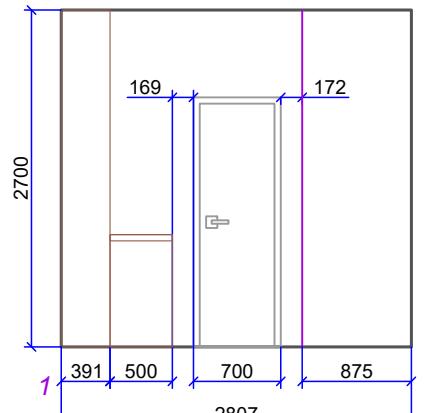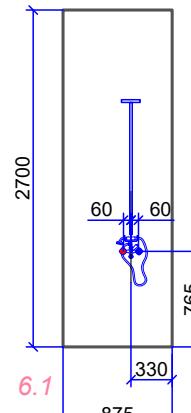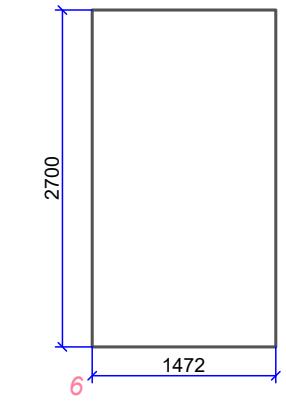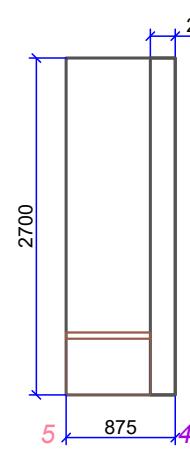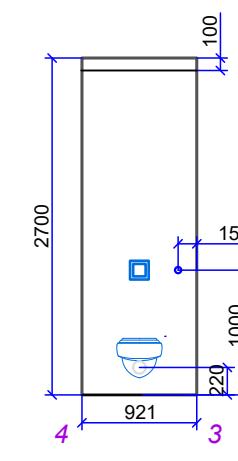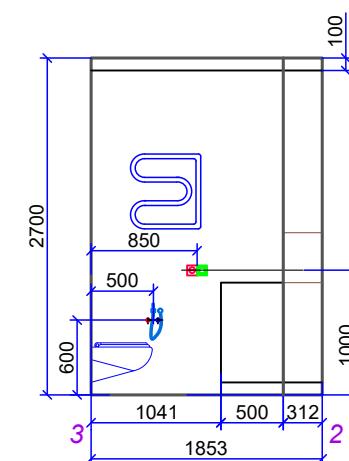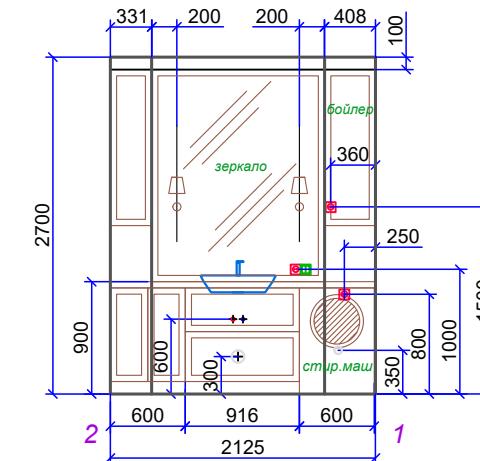

Расстояние между плитками 1,5 мм *

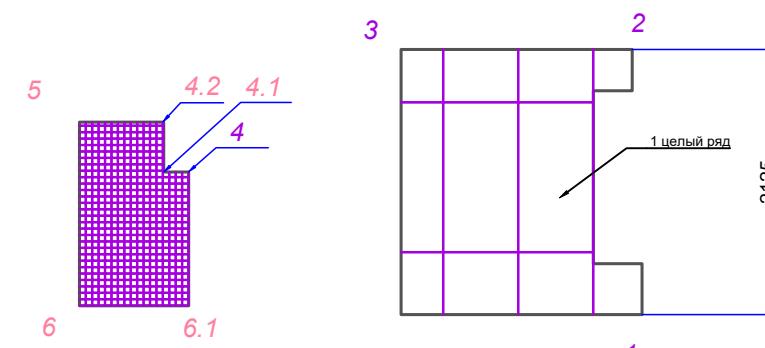

Расстояние между плитками 1,5 мм *

Условные обозначения	
	плитка напольная тип 1 1200x600
	плитка настенная тип 2 1200x600
	плитка напольная тип 3 50x50

- Условные обозначения**
- розетка электрическая
 - розетка интернет
 - розетка usb
 - выключатель 1-о клавишиный
 - выключатель 2-х клавишиный
 - терморегулятор
 - вывод горячей воды
 - вывод холода воды
 - слив воды

* - размеры по согласованию

Раскладка стен. Раскладка полов. Санузел